




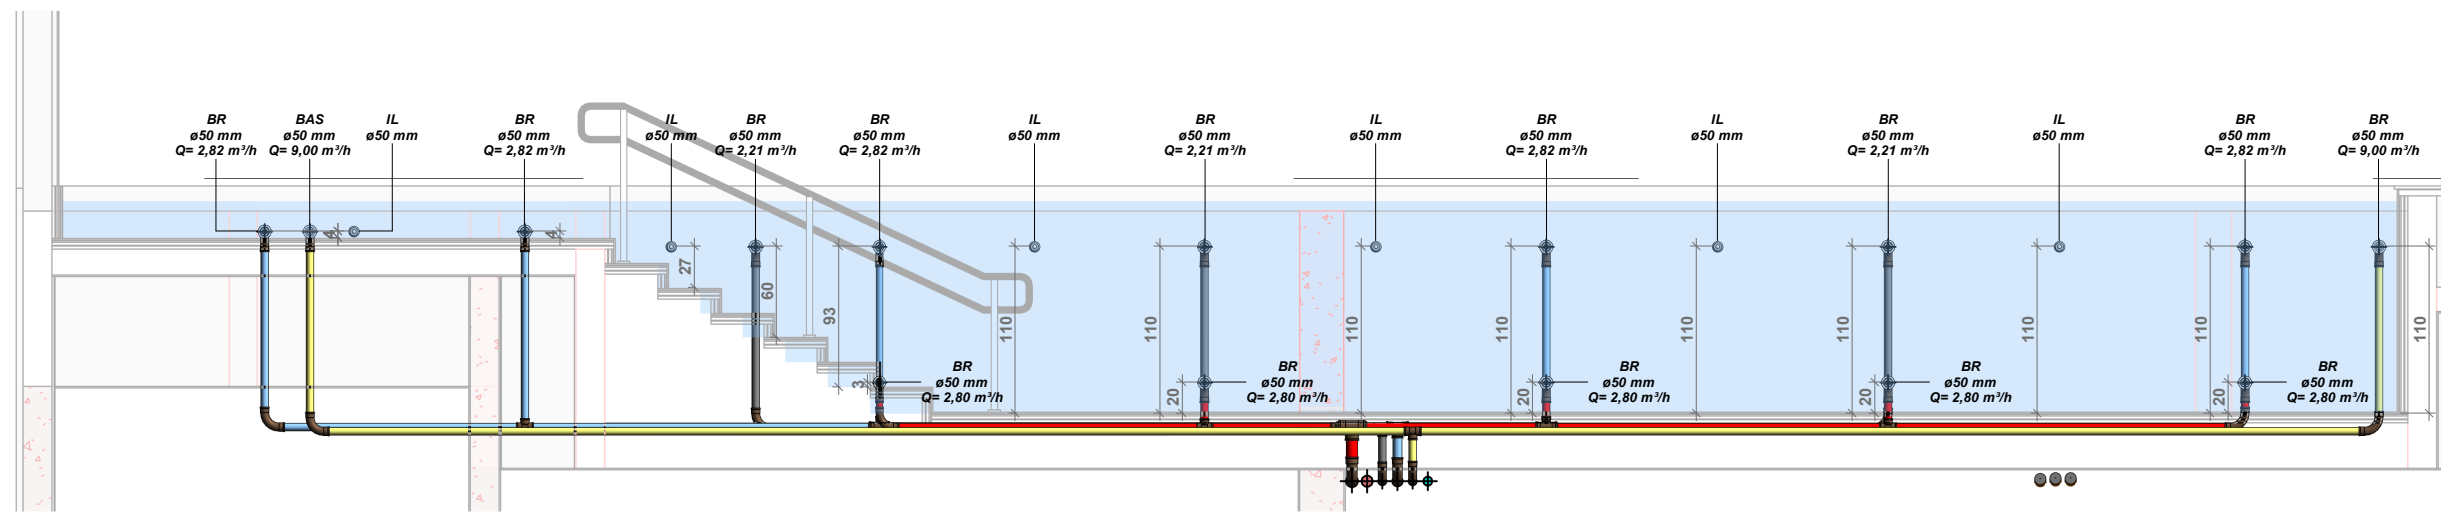


CORTE AA - FRIENDS & POOL
1:50

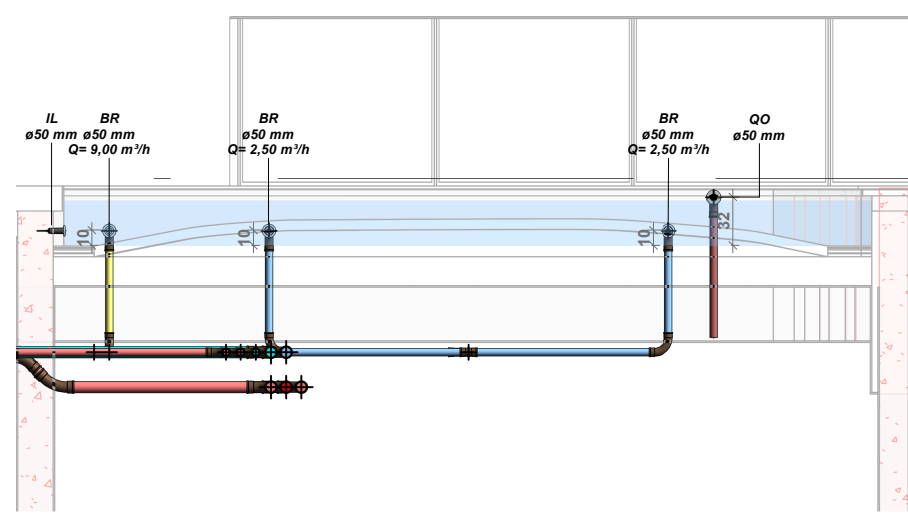


CORTE BB - SPLASH KIDS
1:50

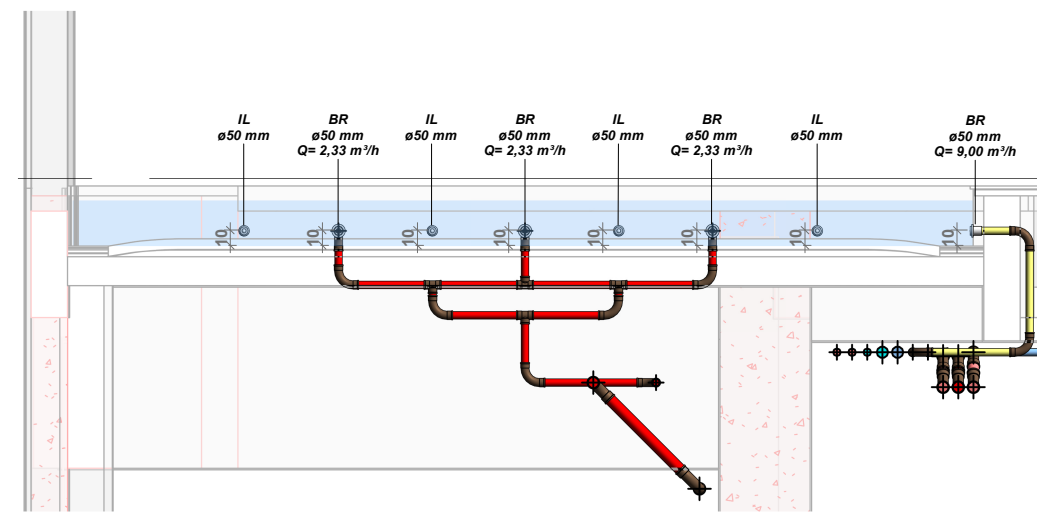


CORTE CC - SPLASH KIDS
1:50

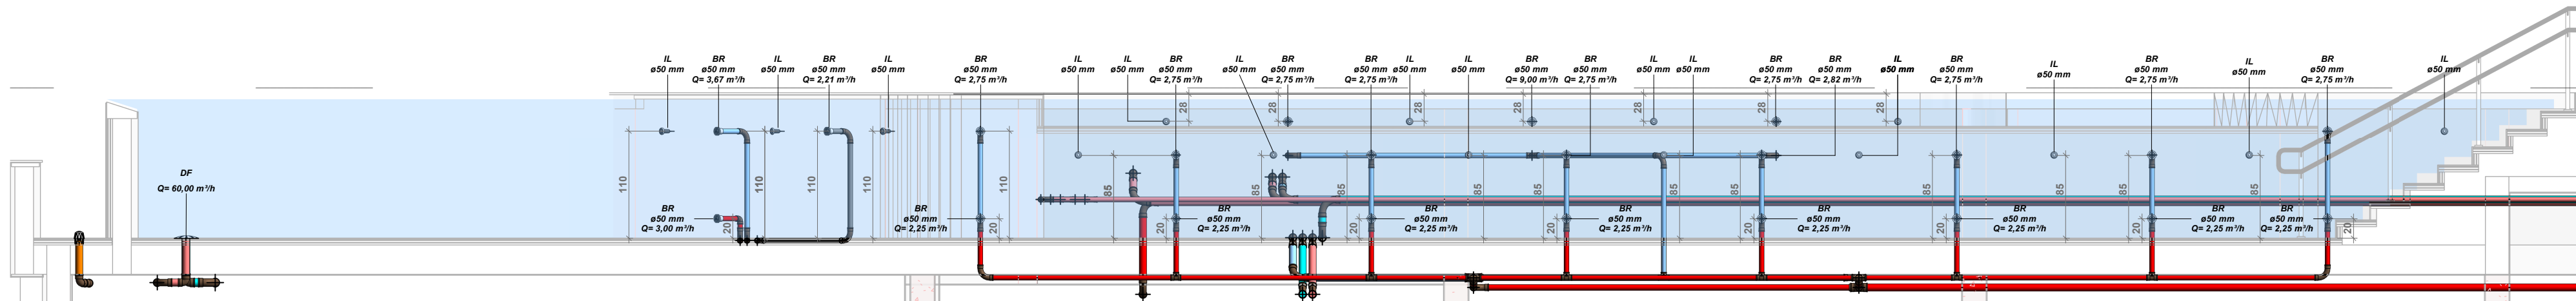


CORTE DD - PISCINA ADULTO
1:50

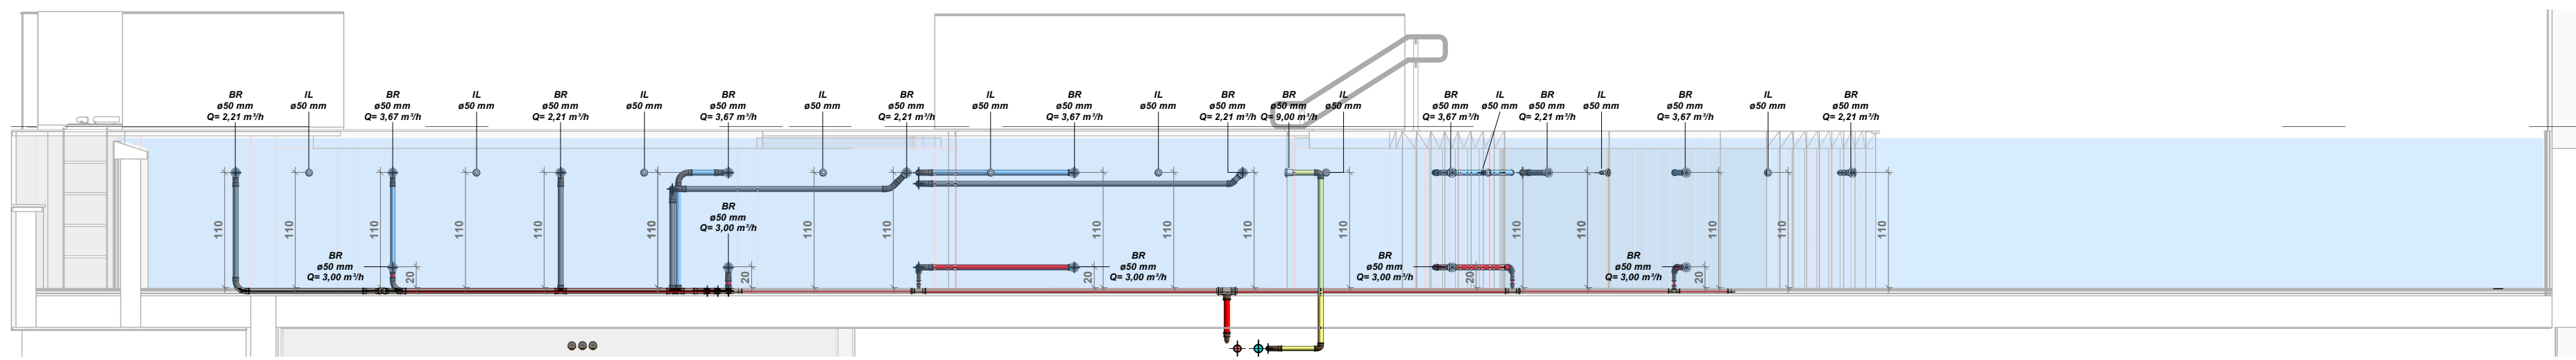

CORTE EE - PISCINA ADULTO
1:50

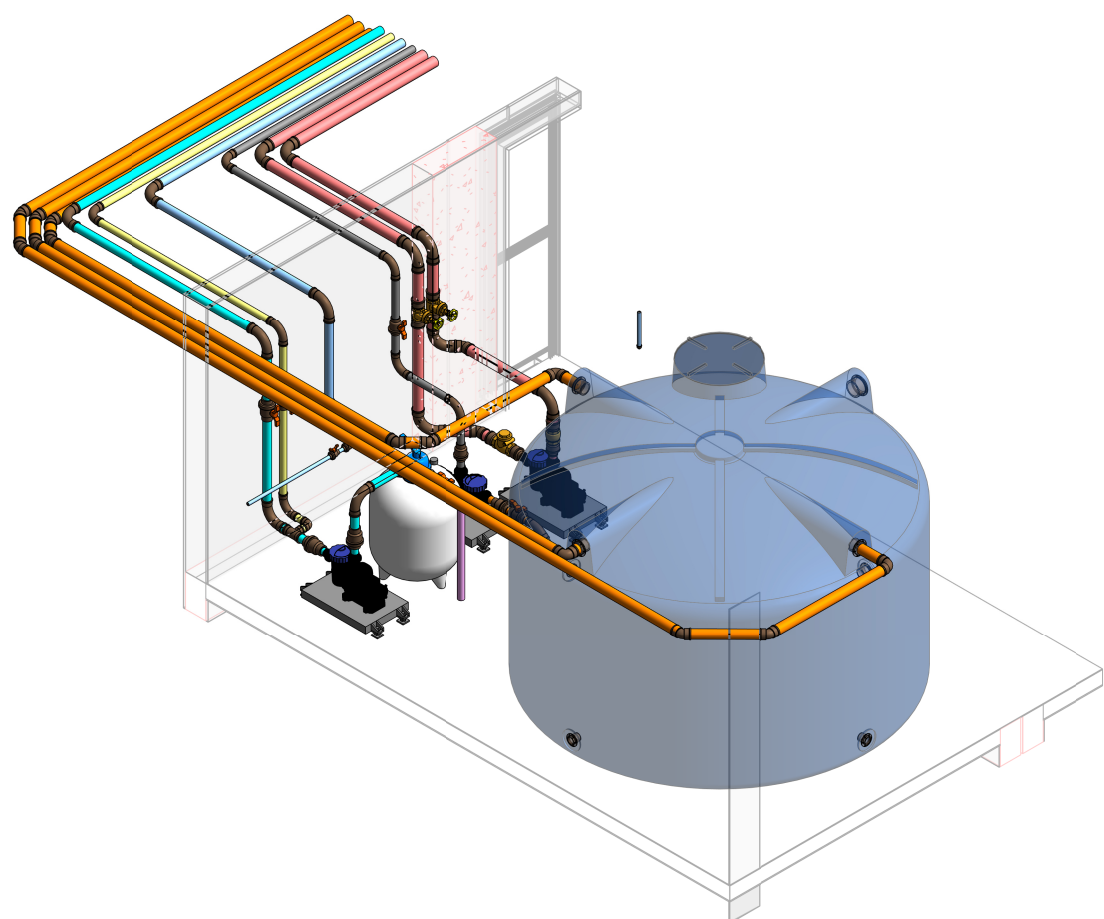


CASA DE BOMBAS - FRIENDS & POOL
1:50

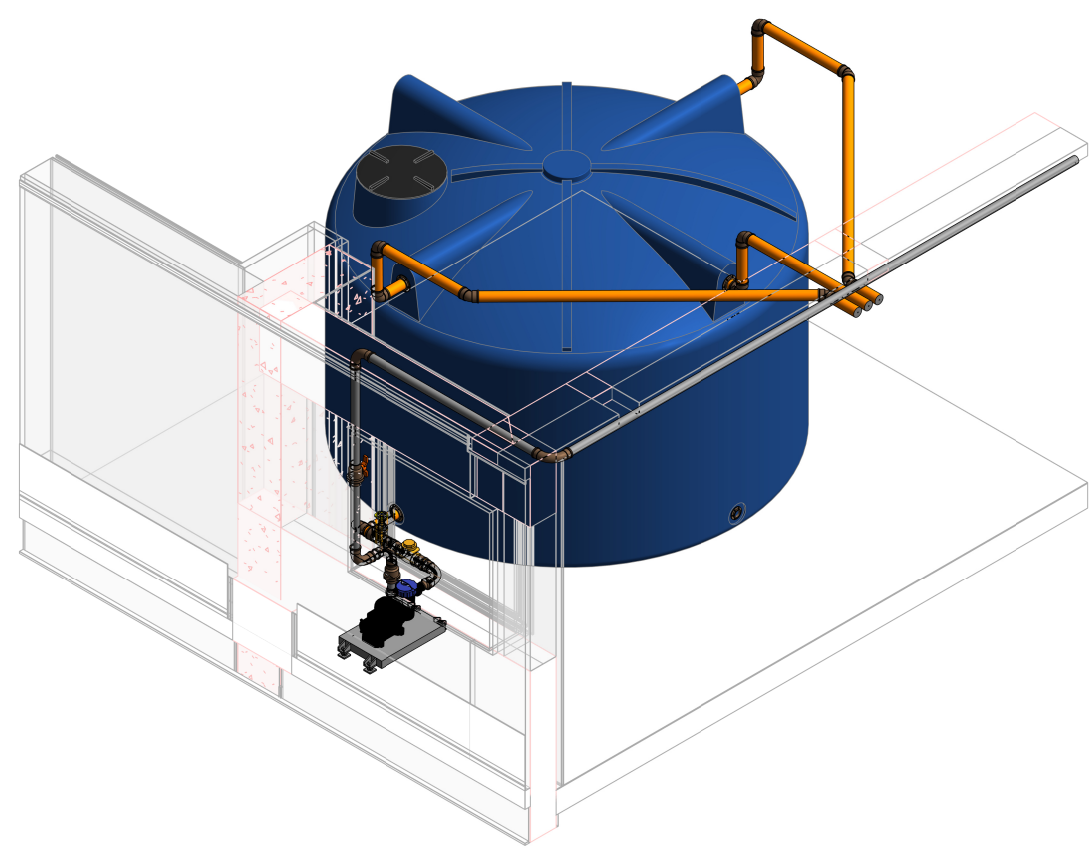

ÁREA TÉCNICA RESERVATÓRIO BORDA INFINITA - PISCINA ADULTO
1:50


BOMBAS DE CALOR - SPLASH KIDS E ADULTO
1:50

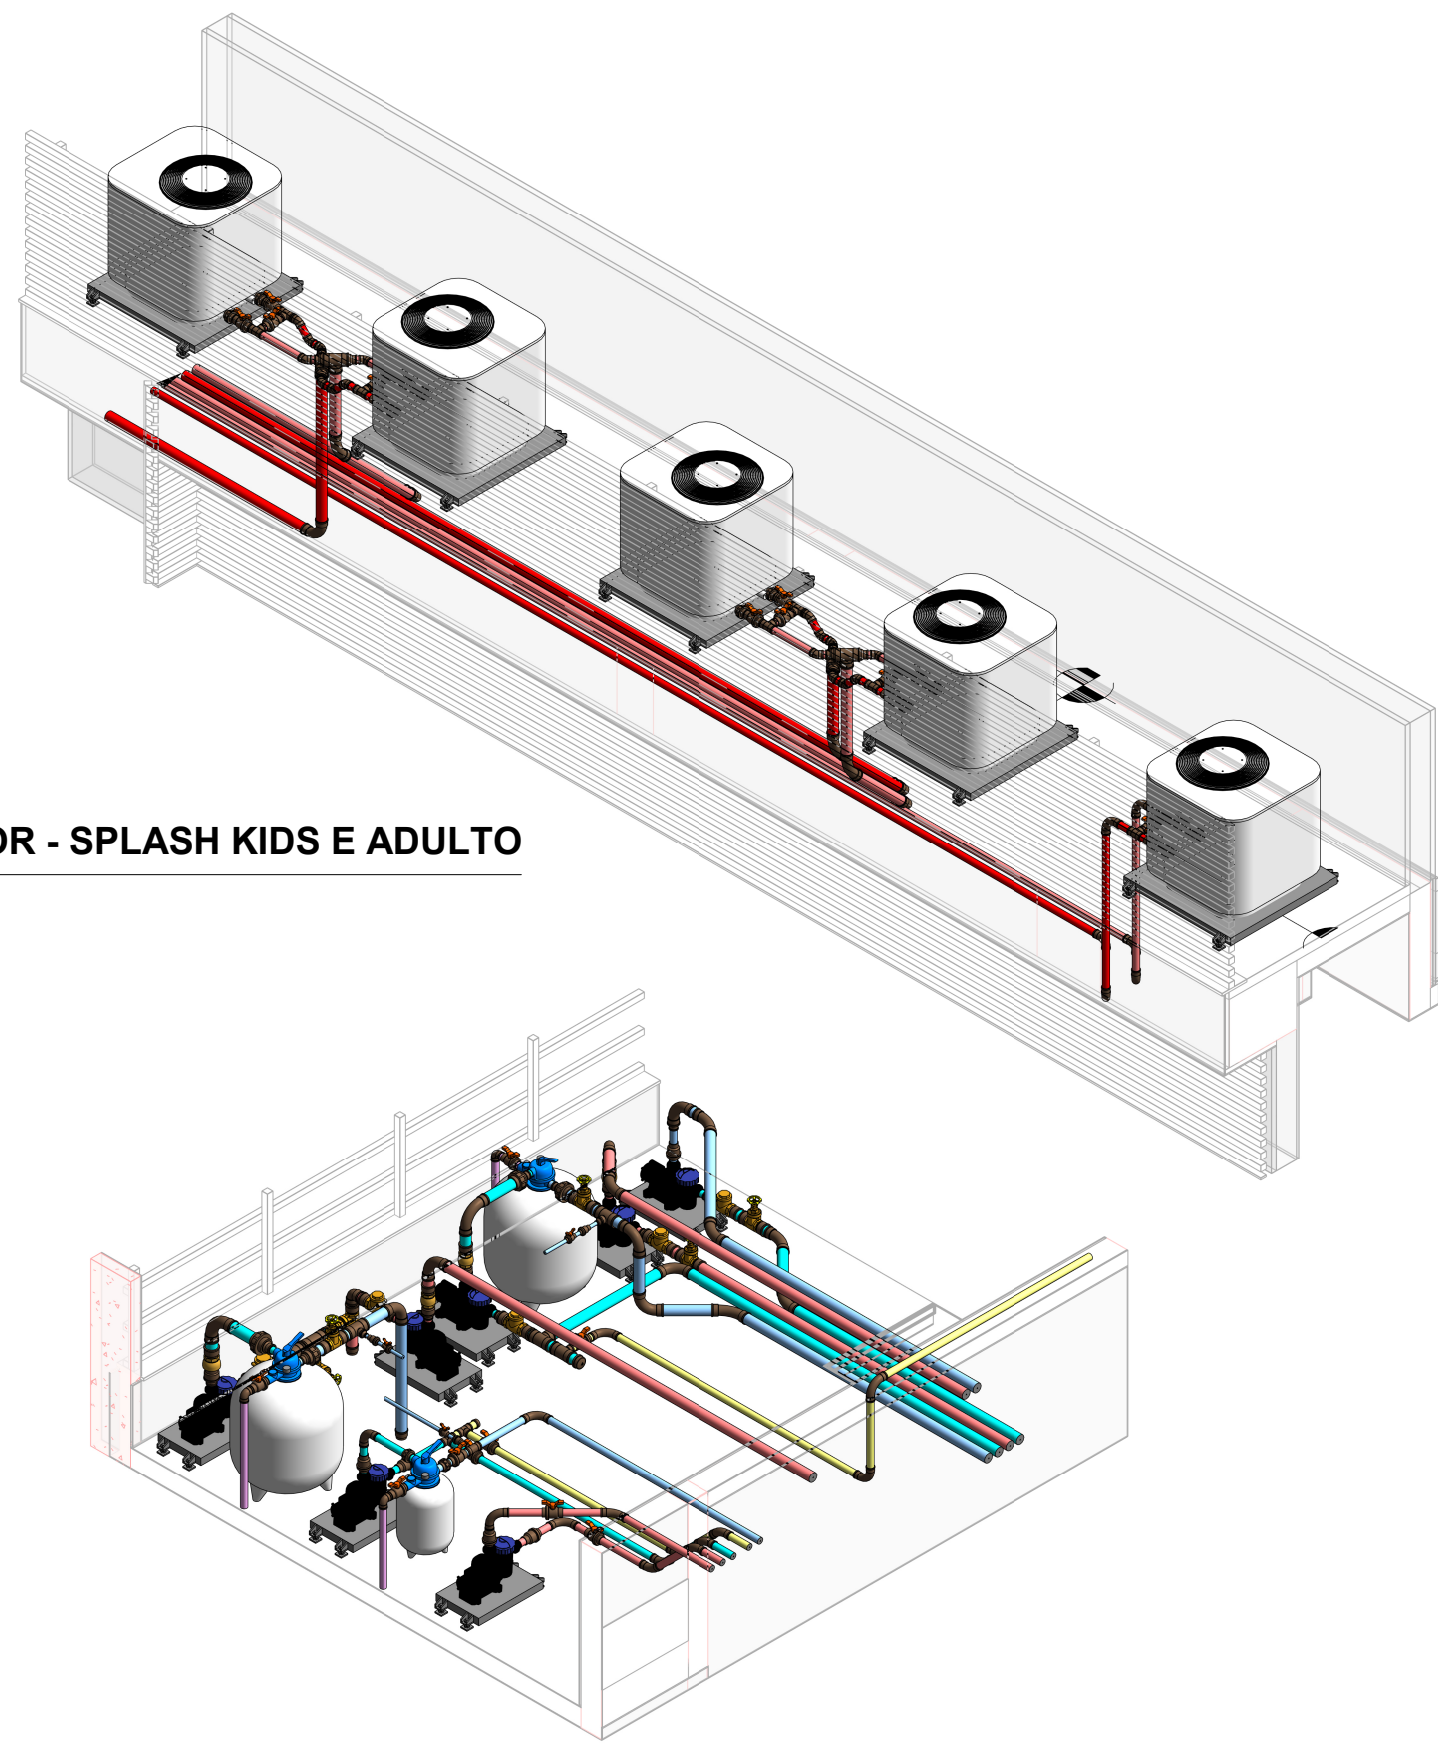


CASA DE BOMBAS - SPLASH KIDS E ADULTO
1:50

NOTAS ABNT NBR 10339:2018
Os sistemas de sucção devem ser executados de forma a proporcionar segurança ao usuário.
Para tanto, devem ser executados atendendo um dos seguintes requisitos:

- montar o sistema de sucção com no mínimo dois drenos de fundo equipados com grelha antiaprissonamento, interligados entre si, distantes no mínimo de 1,5 m de centro a centro, equilibrados hidráulicamente;
- dimensionar a captação de água pela superfície por meio de coadeira (skimmer) ou canaletas, com vazão adequada para a sucção da bomba instalada. Em tanque onde a sucção for feita somente pela coadeira, dimensionar no mínimo duas coadeiras para que não ocorra risco de aprisionamento nele;
- montar o sistema de sucção com um dreno de fundo equipado com grelha antiaprissonamento instalada com tanque intermediário de sucção indireta;
- montar o sistema de sucção com um dreno de fundo, contanto que seja com grelha antiaprissonamento não bloqueável

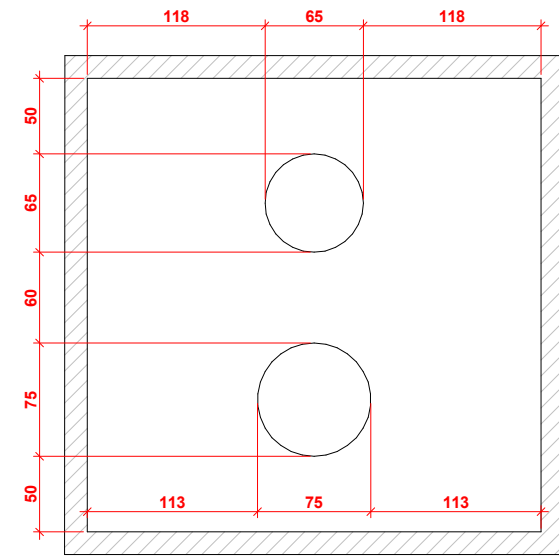

PLANTA BAIXA

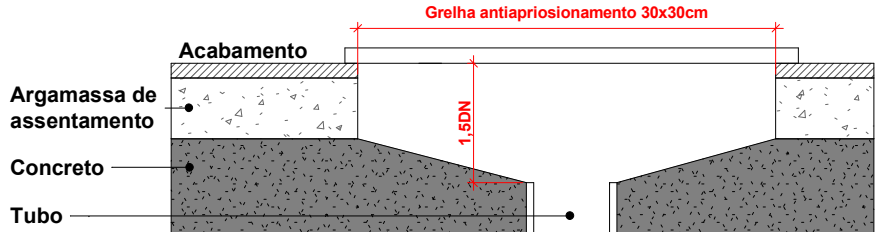


CORTE


DETALHE RALO DE FUNDO - CONFORME NBR 10339
PISCINA FRIENDS & POOL
SEM ESCALA

NOTAS ABNT NBR 10339:2018
Os sistemas de sucção devem ser executados de forma a proporcionar segurança ao usuário.
Para tanto, devem ser executados atendendo um dos seguintes requisitos:

- montar o sistema de sucção com no mínimo dois drenos de fundo equipados com grelha antiaprissonamento, interligados entre si, distantes no mínimo de 1,5 m de centro a centro, equilibrados hidráulicamente;
- dimensionar a captação de água pela superfície por meio de coadeira (skimmer) ou canaletas, com vazão adequada para a sucção da bomba instalada. Em tanque onde a sucção for feita somente pela coadeira, dimensionar no mínimo duas coadeiras para que não ocorra risco de aprisionamento nele;
- montar o sistema de sucção com um dreno de fundo equipado com grelha antiaprissonamento instalada com tanque intermediário de sucção indireta;
- montar o sistema de sucção com um dreno de fundo, contanto que seja com grelha antiaprissonamento não bloqueável

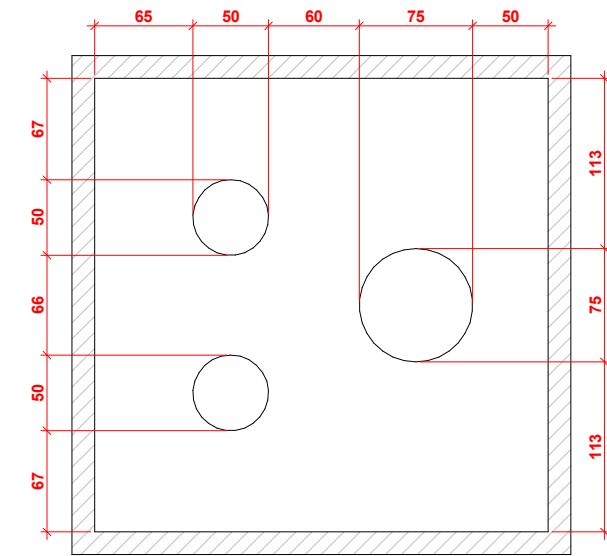

PLANTA BAIXA

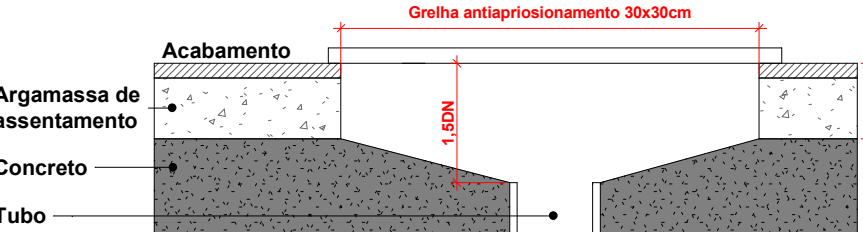


CORTE


DETALHE RALO DE FUNDO - CONFORME NBR 10339
PISCINA SPLASH KIDS
SEM ESCALA

NOTAS ABNT NBR 10339:2018
Os sistemas de sucção devem ser executados de forma a proporcionar segurança ao usuário.
Para tanto, devem ser executados atendendo um dos seguintes requisitos:

- montar o sistema de sucção com no mínimo dois drenos de fundo equipados com grelha antiaprissonamento, interligados entre si, distantes no mínimo de 1,5 m de centro a centro, equilibrados hidráulicamente;
- dimensionar a captação de água pela superfície por meio de coadeira (skimmer) ou canaletas, com vazão adequada para a sucção da bomba instalada. Em tanque onde a sucção for feita somente pela coadeira, dimensionar no mínimo duas coadeiras para que não ocorra risco de aprisionamento nele;
- montar o sistema de sucção com um dreno de fundo equipado com grelha antiaprissonamento instalada com tanque intermediário de sucção indireta;
- montar o sistema de sucção com um dreno de fundo, contanto que seja com grelha antiaprissonamento não bloqueável

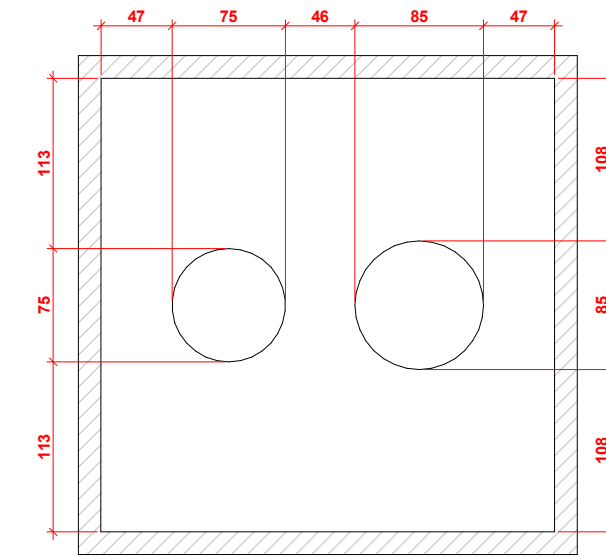

PLANTA BAIXA

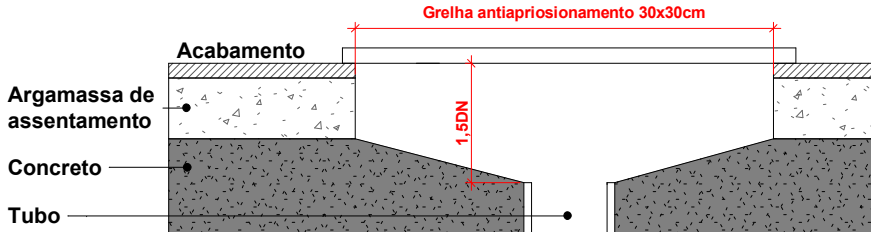

CORTE

DETALHE RALO DE FUNDO - CONFORME NBR 10339
PISCINA ADULTO
SEM ESCALA

LEGENDA			
INSTALAÇÕES PISCINA			
BOCAL DE RETORNO (AQ)	BR	QUEBRA ONDA - EXTRAVASOR	QO
BOCAL DE RETORNO (AF)	BR	DRENO DE FUNDO	DF
BOCAL DE ASPIRAÇÃO	BAS	COADEIRA	CO
BOCAL DE HIDROMASSAGEM	BH	ILUMINAÇÃO	IL
TUBULAÇÃO			
TUBULAÇÃO DE SUÇÃO FILTRO			
TUBULAÇÃO DE SUÇÃO ÁGUA QUENTE			
TUBULAÇÃO DE SUÇÃO HIDROMASSAGEM			
TUBULAÇÃO DE SUÇÃO CASCATA			
TUBULAÇÃO DE SUÇÃO BORDA INFINITA			
TUBULAÇÃO DE RETORNO DE ÁGUA FRIA			
TUBULAÇÃO DE RETORNO DE ÁGUA QUENTE			
TUBULAÇÃO DE RETORNO HIDROMASSAGEM			
TUBULAÇÃO DE RETORNO CASCATA			
TUBULAÇÃO DE RETORNO BORDA INFINITA			
TUBULAÇÃO DE ASPIRAÇÃO			
TUBULAÇÃO DE COADEIRA			
TUBULAÇÃO DE EXTRAVASOR			
TUBULAÇÃO DE LIMPEZA			

- NOTAS**
- TODAS TUBULAÇÕES NÃO INDICADAS DEVERÃO SER EXECUTADAS COM DIÂMETRO DE 50 mm;
 - A TUBULAÇÃO DO AQUECIMENTO DEVERÁ SER REVESTIDA COM ISOLANTE TÉRMICO A BASE DE POLIETILENO EXPANDIDO, NO MÍNIMO COM 10MM DE ESPESURA.
 - SÓ USAR JOELHO QUANDO ESPECIFICADO EM PROJETO.
 - AS MEDIDAS DOS DISPOSITIVOS TEM COMO BASE O CONTRA PISO DO CONTORNO DA PISCINA ATÉ A METADE DO TUBO
 - A IMPERMEABILIZAÇÃO NÃO PODE ENTRAR DENTRO DOS TUBOS, DEVERÁ SER FEITO CIRCUNDANDO A PARTE EXTERNA DO MESMO PARA EVITAR VAZAMENTO.
 - OS TUBOS DEVEM SER AFIXADOS COM CINTA PERFORADA DE INOX E PARAFUSOS DE INOX OU SIMILAR QUE SEJAM ANTICORROSIVOS
 - AS INSTALAÇÕES ELÉTRICAS E O SEU ATERRAMENTO DEVEM SER DIMENSIONADOS DE ACORDO COM A NBR 5410, SENDO QUE OS QUADROS DE FORÇA E DE COMANDO DEVEM SER INSTALADOS PRÓXIMOS A PORTA DE ACESSO.

MODELO ARQUITETURA / ESTRUTURA			
ARQUITETURA 017-ARQ-EX-0000-000-GER-T00-R02		ESTRUTURA 017-EST-EX-0001-000-MOD-T00-R03	
QUADRO DE REVISÕES			
REVISÃO	DESCRIÇÃO	AUTOR	DATA
R00	EMIÇÃO LIBERADO OBRA	GUSTAVO H.	07/05/2025

ASSINATURAS	
RESPONSÁVEL PELA EXECUÇÃO	CARIMBO ORÇÃO PÚBLICO
EXECUÇÃO	

RESPONSÁVEL(S) TÉCNICO(S) PELO PROJETO

HØYT / ENGENHARIA INTEGRADA

HOYT ENGENHARIA INTEGRADA LTDA - CREA-SC 169005-2 - CNPJ 31.634.971/0001-17
Rua Antônio Da Veiga, 256 - Edifício Kollinas, Sala 07 E 08 - Itoupava Seca, Blumenau / SC - CEP: 89030-103
www.hoyt.eng.br | (47) 3035-6905

EMPREENDIMENTO	
PARADISE BAY	
AVENIDA NEREU RAMOS Nº 3487, CENTRO - BALNEÁRIO PIÇARRAS/SC	
PROPRIETÁRIO	
VETTER EMPREENDIMENTOS SPE LTDA	
CNPJ: 39.610.171/0001-78	

PROJETO PISCINA			
PROJETADO POR IGOR P.	DETALHADO POR IGOR P.	REVISADO POR ALAN M.	PRIMEIRA
CONTEÚDO			
CORTES E ISOMÉTRICOS			
ARQUIVO 017-PIS-LO-0003-004-DET-T00-R00	ESCALA 1:50	REFERÊNCIA 181	0003-DET EXECUTIVO (LIBERADO PARA OBRA)