



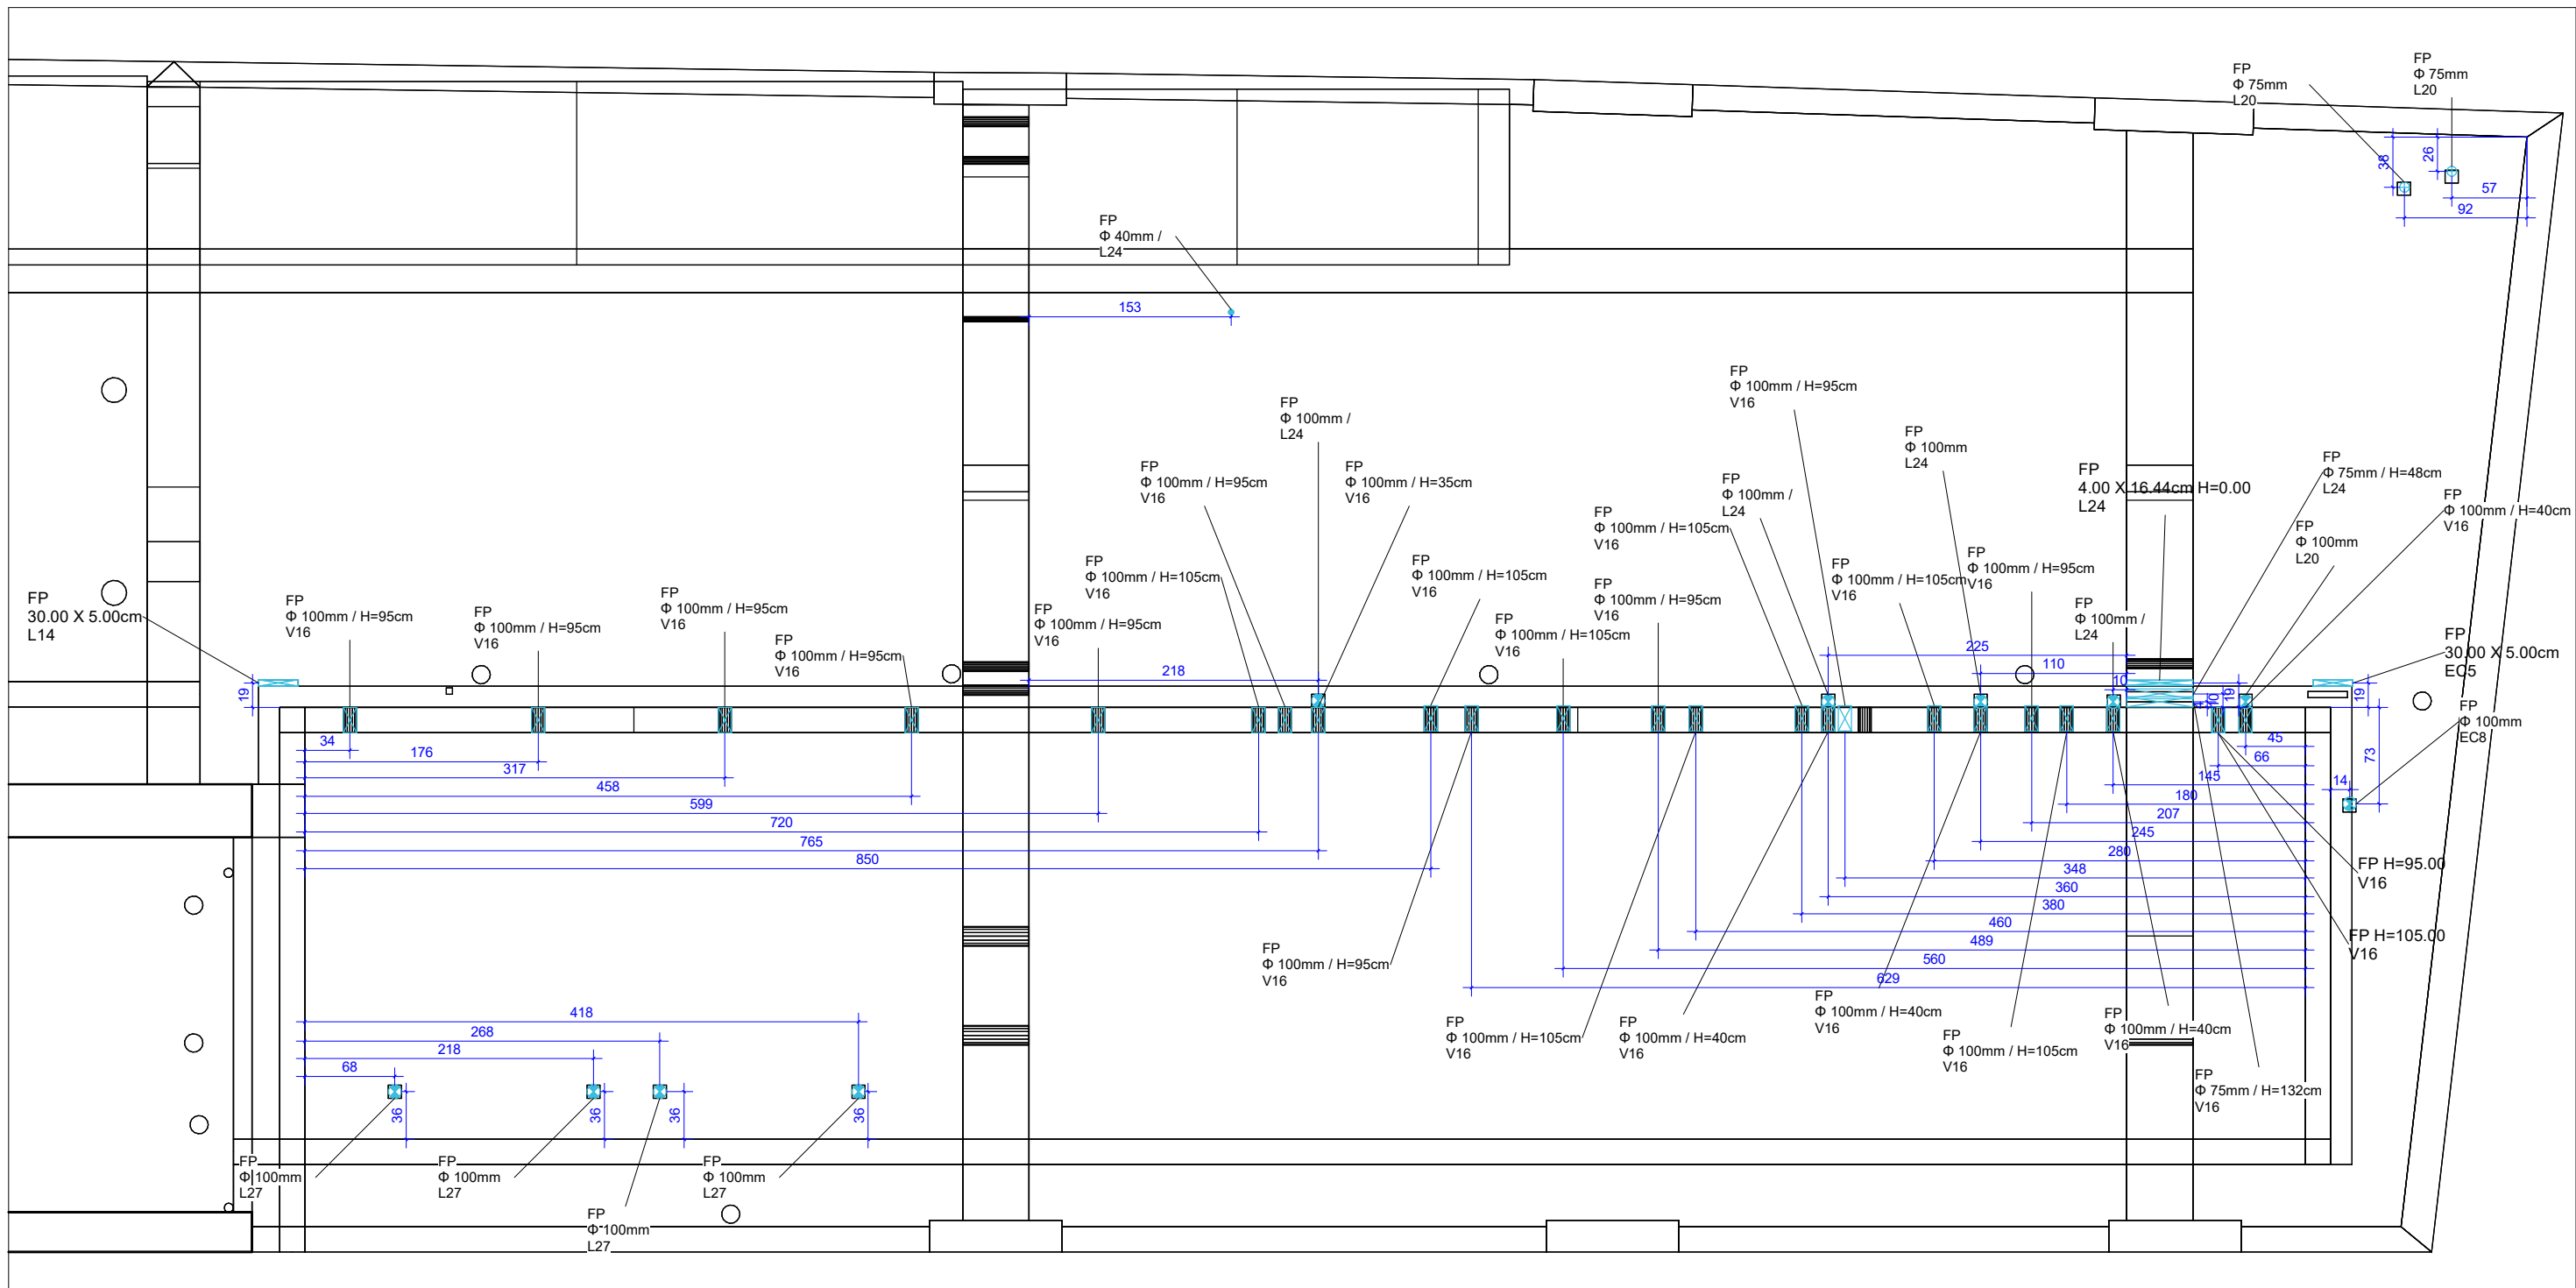

PAVTO. LAZER - MARCAÇÃO FUROS
ESCALA 1:50

QUADRO DE COMANDO PISCINA - FILTRAGEM, AQUECIMENTO E ILUM.

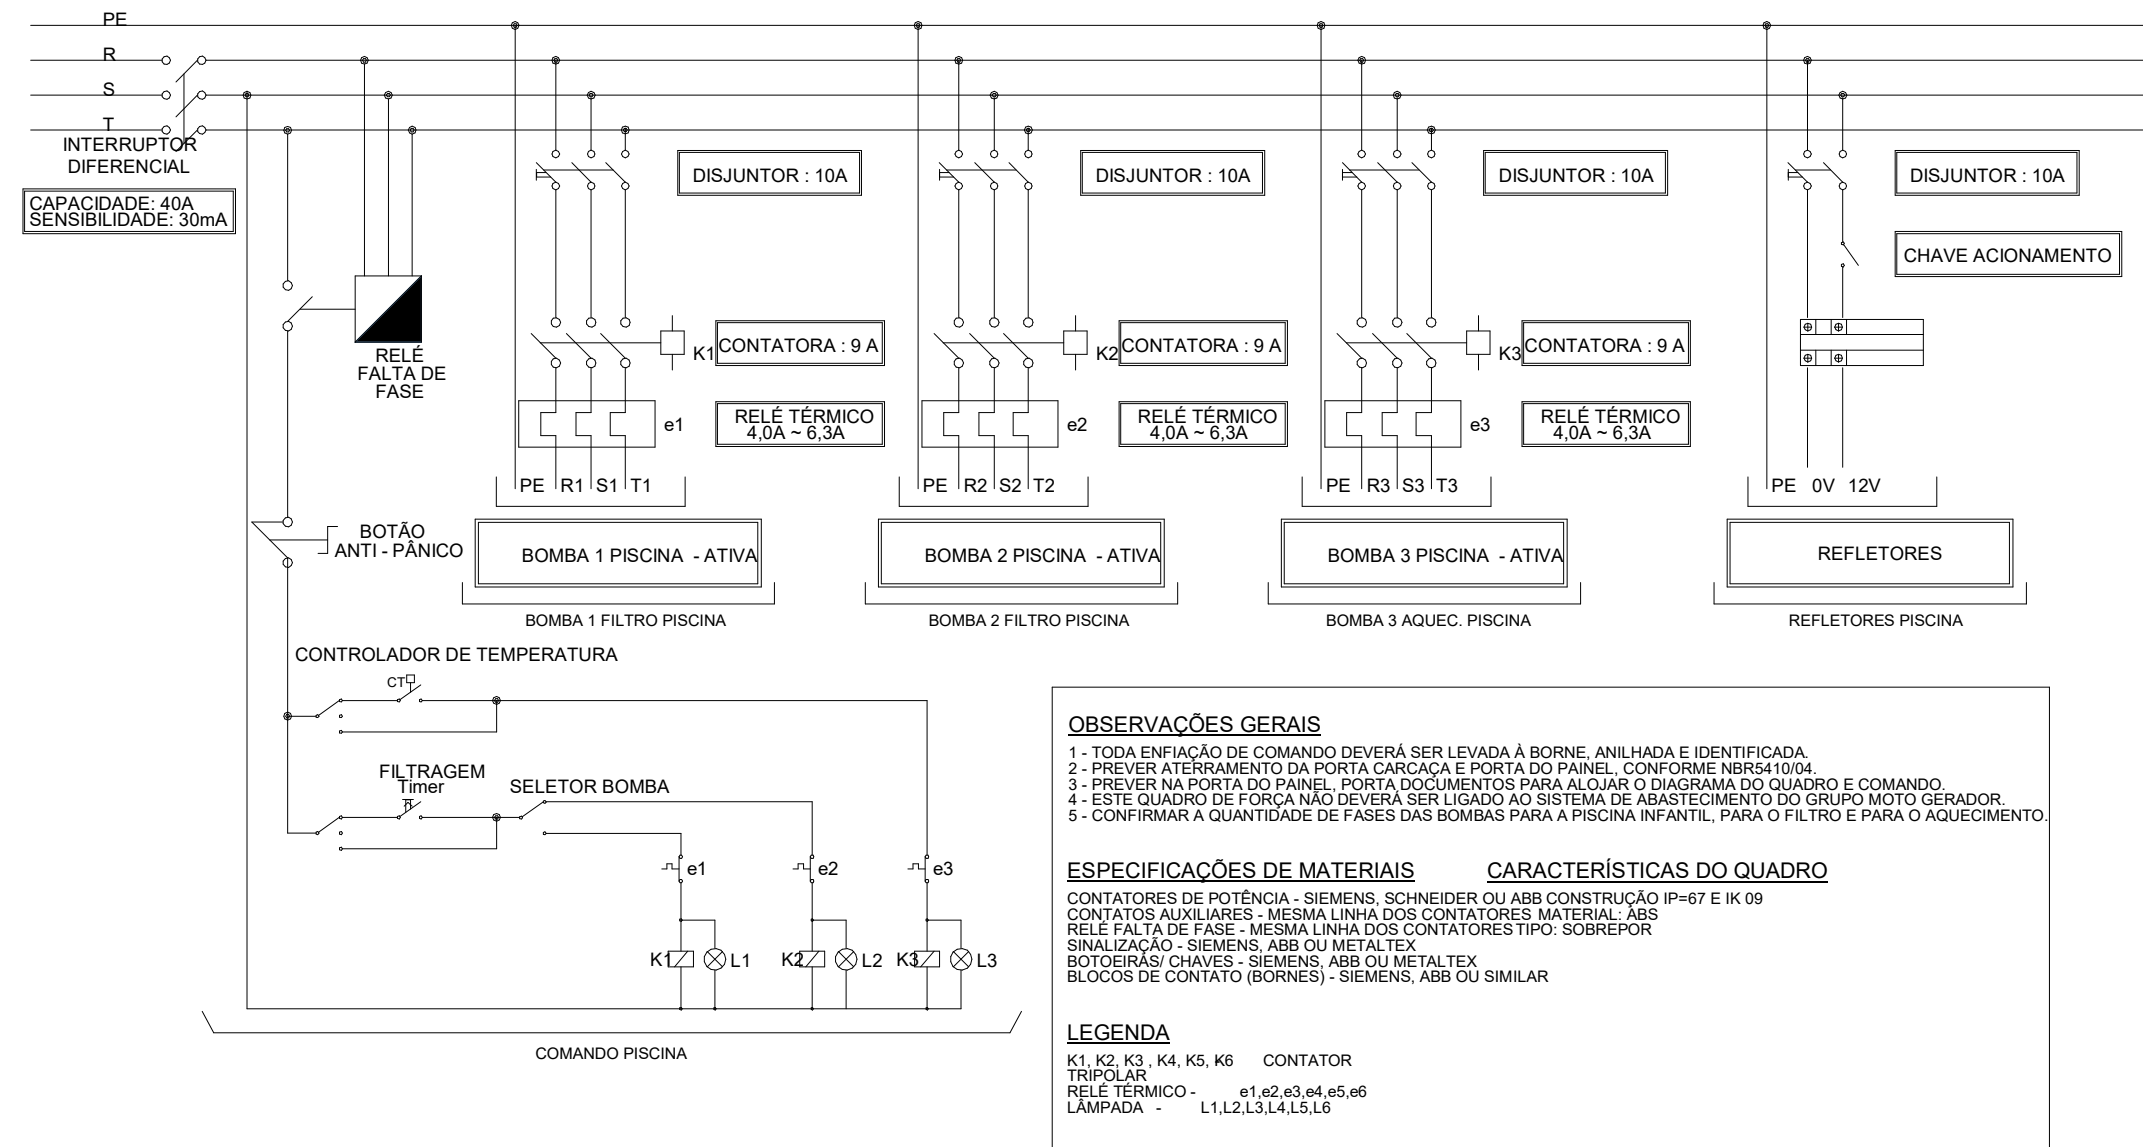

OBSERVAÇÕES GERAIS

- 1 - TODA ENFAIXAÇÃO DE COMANDO DEVERÁ SER LEVADA À BORNÉ, ANILHADA E IDENTIFICADA.
- 2 - PREVER ATERRAMENTO DA PORTA CARCAÇA E PORTA DO PAINEL, CONFORME NBR 10004.
- 3 - PREVER NA PORTA DO PAINEL, PORTA DOCUMENTOS PARA ALIAR O DIAGRAMA DO QUADRO E COMANDO.
- 4 - ESTE QUADRO DE FORÇA NÃO DEVERÁ SER LIGADO AO SISTEMA DE ABASTECIMENTO DO GRUPO MOTOR GERADOR.
- 5 - CONFIRMAR A QUANTIDADE DE FASES DAS BOMBAS PARA A PISCINA INFANTIL, PARA O FILTRO E PARA O AQUECIMENTO.

ESPECIFICAÇÕES DE MATERIAIS


CONTADORES DE POTÊNCIA - SIEMENS, SCHNEIDER OU ABB CONSTRUÇÃO IP-67 E IK-09
CONTATOS AUXILIARES - MESMA LINHA DOS CONTADORES MATERIAL ABB
RELE FALTA DE FASE - MESMA LINHA DOS CONTADORES TIPO: SOBRESOR
SINALIZAÇÃO - SIEMENS ABB OU METALTEX
BOTOEIRAS/CHAVES - SIEMENS, ABB OU METALTEX
BLOCOS DE CONTATO (BORNES) - SIEMENS, ABB OU SIMILAR

LEGENDA

K1, K2, K3, K4, K5, K6 CONTATOR
T1, T2, T3 TRIPOLAR
RELE TÉRMICO - e1, e2, e3, e4, e5, e6
LÂMPADA - L1, L2, L3, L4, L5, L6


ESQUEMA UNIFILAR QUADRO DE
SEM ESCALA

DETALHES DE FUROS EM VIGAS

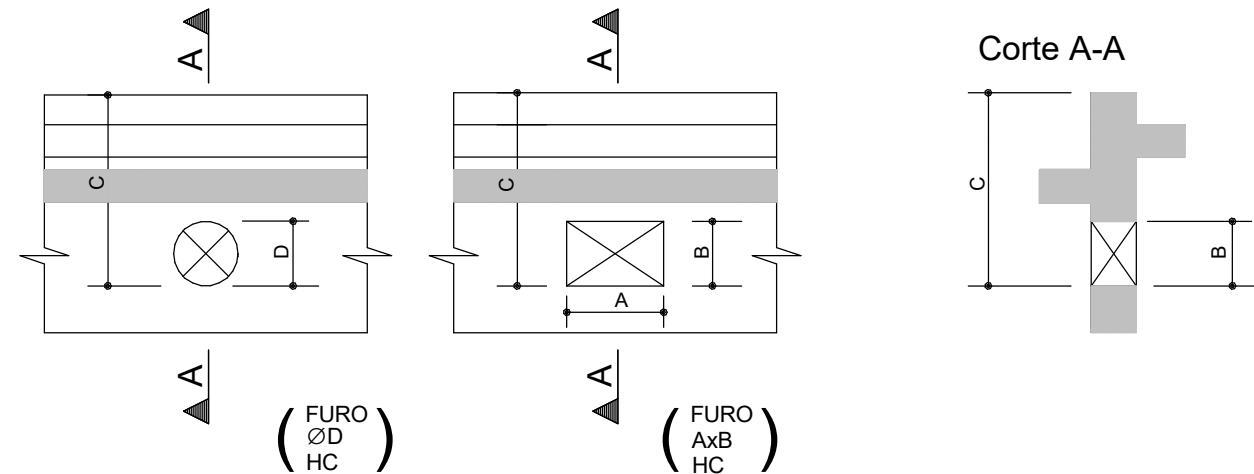


- A MEDIDA "C" REFERE-SE À DIFERENÇA ENTRE O NÍVEL SUPERIOR DA VIGA E O NÍVEL INFERIOR DO FURO.

7-NOTAS E DETALHES DE VIGAS

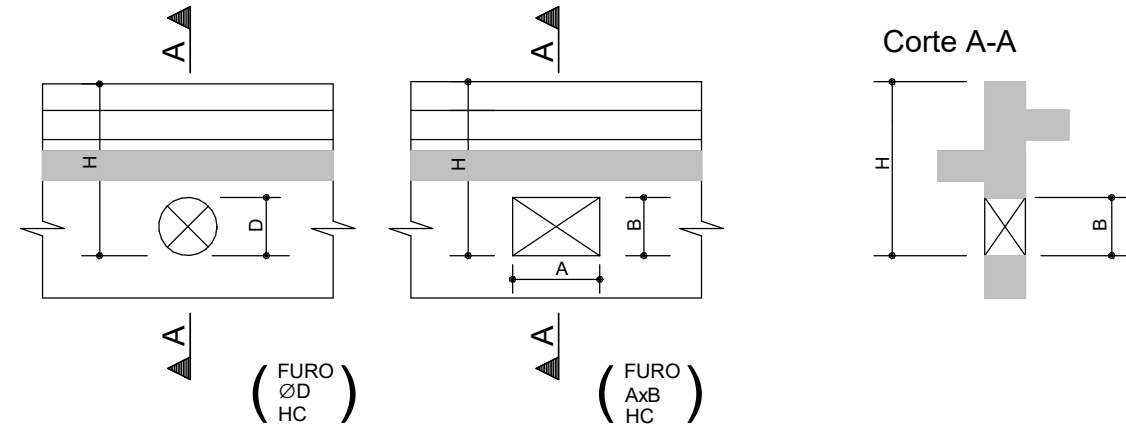

- A MEDIDA "H" REFERE-SE À DIFERENÇA ENTRE O NÍVEL SUPERIOR DA VIGA E O NÍVEL INFERIOR DO FURO.

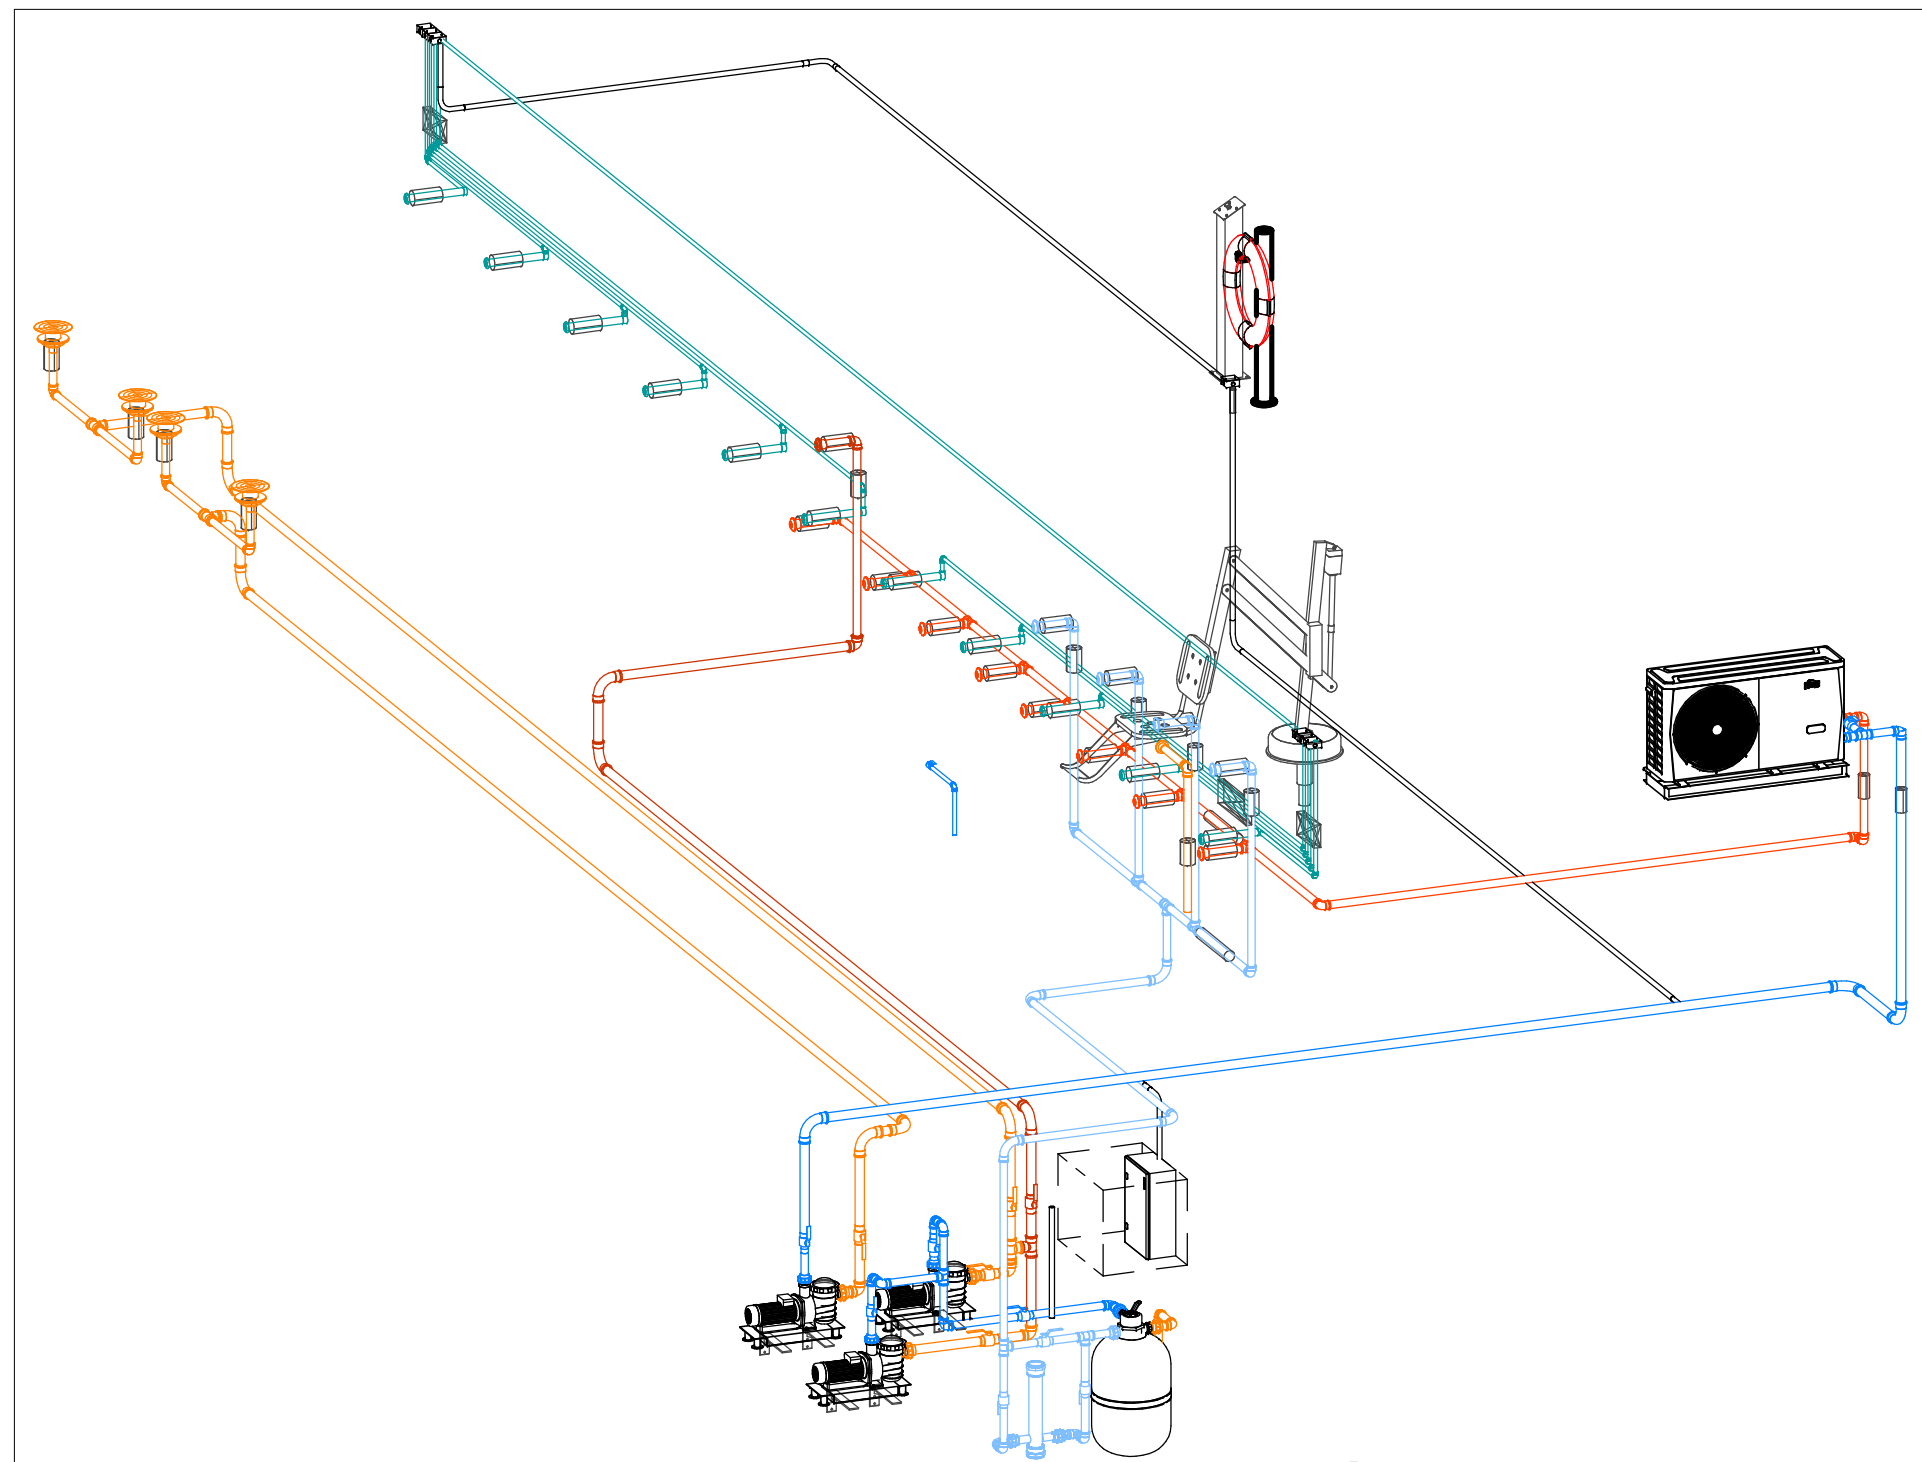

ISOMÉTRICO REDE PISCINA
ESCALA 1:50

FUROS PISCINA	
TIPO	SEÇÃO
•	ø40
•	ø50
•	ø75
•	ø100
•	ø150
•	ø200
•	ø300

R03	ATUALIZAÇÃO BASES, ALTERAÇÃO LOCAL CASA DE MÁQUINAS, AJUSTE TUBULAÇÕES, AJUSTE FUROS	B.K.	30/01/2026
R02	ATUALIZAÇÃO BASE ARQUITETURA E ESTRUTURA, AJUSTE FUROS E REDE	G.A.P.	04/12/2024
R01	ATUALIZAÇÃO BASES, AJUSTE REDE E DISPOSITIVOS	P. ENG.	22/10/2024
R00	EMIÇÃO EX - AJUSTE FUROS E REDE	P. ENG.	26/06/2024
REVISÃO	DESCRIÇÃO DAS ALTERAÇÕES	RESP.	DATA

VITREO

005

Nº DO PROJETO:

AV. NEREU RAMOS, ESQUINA COM RUA 271, MEIA PRAIA - ITAPEMA/ SC

ENDEREÇO:

VITREO 271 EMP. IMOB. SPE LTDA

Proprietário:

VITREO 271 EMP. IMOB. SPE LTDA

CONSTRUÇÃO:

ABC

Arquitetando o novo

PIANGERS

ENGENHARIA

Responsável pelo projeto: Eng. Gustavo André Piangers
CREA RS-234.304

WWW.PIANGERS.ENG.BR

PROJETO PISCINA

PISCINA EXTERNA - MARCAÇÃO FUROS

EMIÇÃO:	ESCALA:	DESENHO:	FASE:	PRANCHA E REVISÃO:
20/05/2024	INDICADA	INDICADA		
TÍTULO:	005-EX-PIS-PB-003-LAZ-R04			EX 003 R03