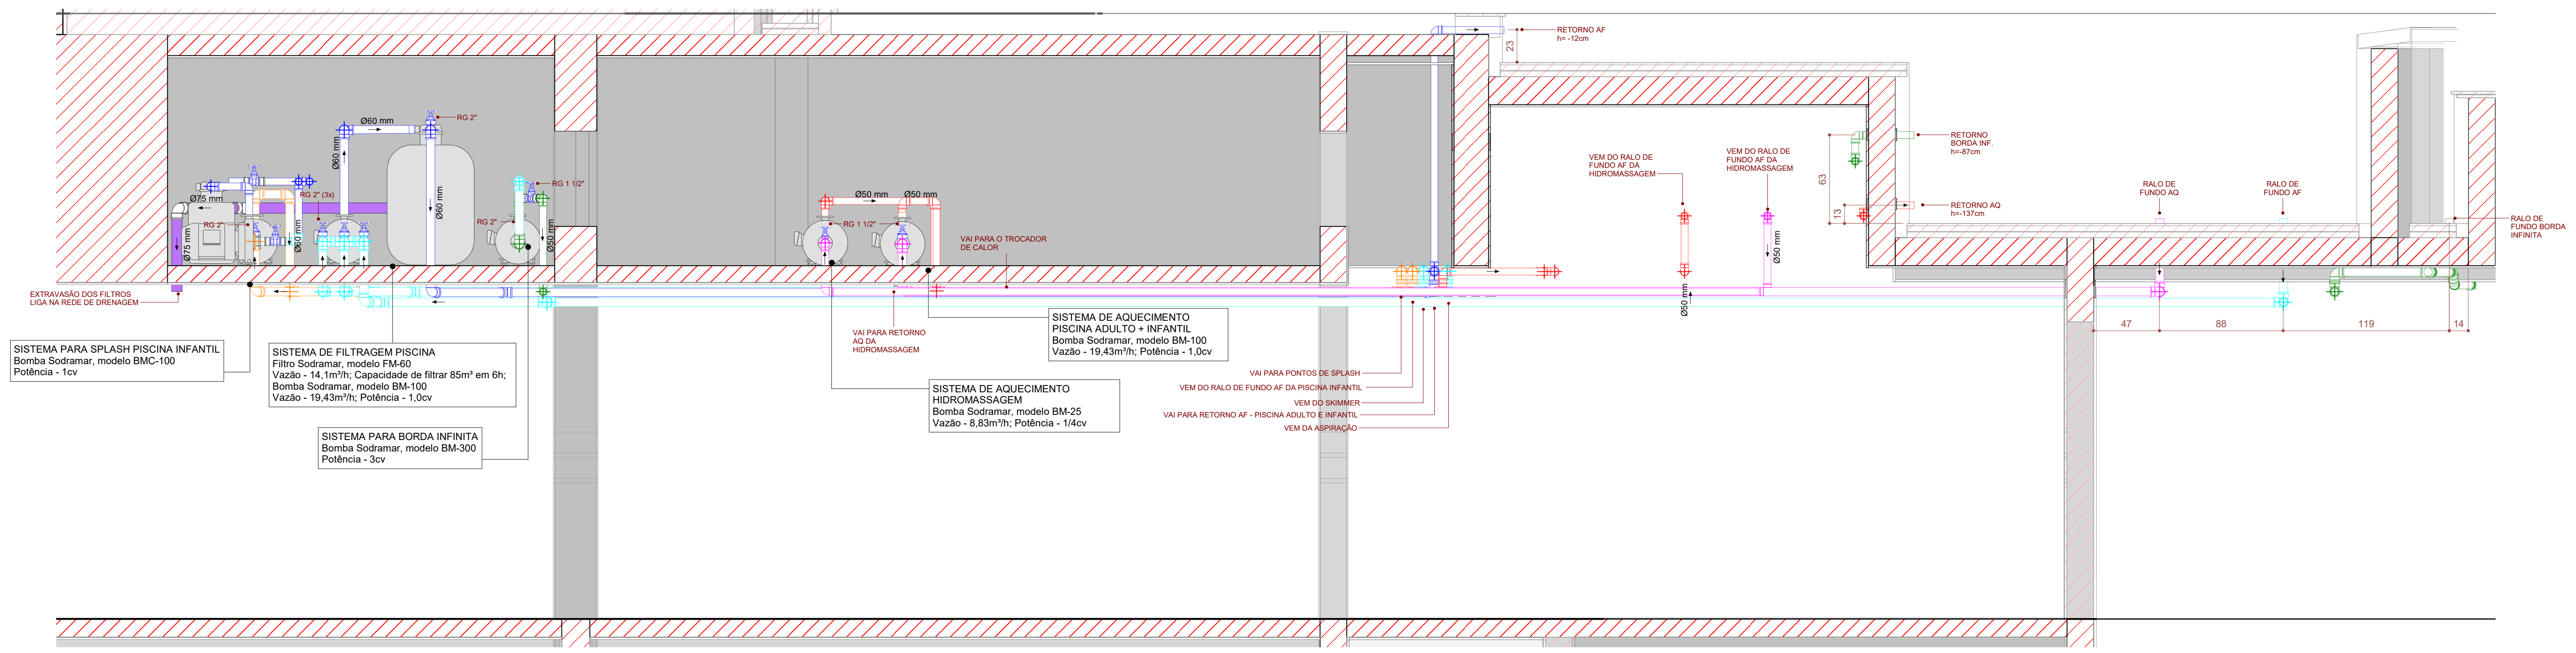
Ø60 mm
RG 2"
Ø60 mm
Ø75 mm
RG 2" (3x)
RG 2"
Ø60 mm
Ø75 mm
Ø60 mm
RG 1 1/2"
RG 2"
Ø50 mm
Ø50 mm
Ø50 mm
RG 1 1/2"
VAI PARA O TROCADOR DE CALOR
EXTRAVASÃO DOS FILTROS LIGA NA REDE DE DRENAGEM
VAI PARA RETORNO AQ DA HIDROMASSAGEM
VAI PARA PONTOS DE SPLASH
VEM DO RALO DE FUNDO AF DA PISCINA INFANTIL
VEM DO SKIMMER
VAI PARA RETORNO AF - PISCINA ADULTO E INFANTIL
VEM DA ASPIRAÇÃO
RETORNO AF h= -12cm
23
VEM DO RALO DE FUNDO AF DA HIDROMASSAGEM
VEM DO RALO DE FUNDO AF DA HIDROMASSAGEM
Ø50 mm
Ø50 mm
RETORNO BORDA INF. h=-87cm
63
13
RETORNO AQ h=-137cm
RALO DE FUNDO AQ
RALO DE FUNDO AF
RALO DE FUNDO BORDA INFINITA
47
88
119
14

SISTEMA PARA SPLASH PISCINA INFANTIL
Bomba Sodramar, modelo BMC-100
Potência - 1cv

SISTEMA DE FILTRAGEM PISCINA
Filtro Sodramar, modelo FM-60
Vazão - 14,1m³/h; Capacidade de filtrar 85m³ em 6h;
Bomba Sodramar, modelo BM-100
Vazão - 19,43m³/h; Potência - 1,0cv

SISTEMA PARA BORDA INFINITA
Bomba Sodramar, modelo BM-300
Potência - 3cv

SISTEMA DE AQUECIMENTO
PISCINA ADULTO + INFANTIL
Bomba Sodramar, modelo BM-100
Vazão - 19,43m³/h; Potência - 1,0cv

SISTEMA DE AQUECIMENTO
HIDROMASSAGEM
Bomba Sodramar, modelo BM-25
Vazão - 8,83m³/h; Potência - 1/4cv

DETALHE 05 - CASA DE BOMBAS DA PISCINA
ESCALA 1:25

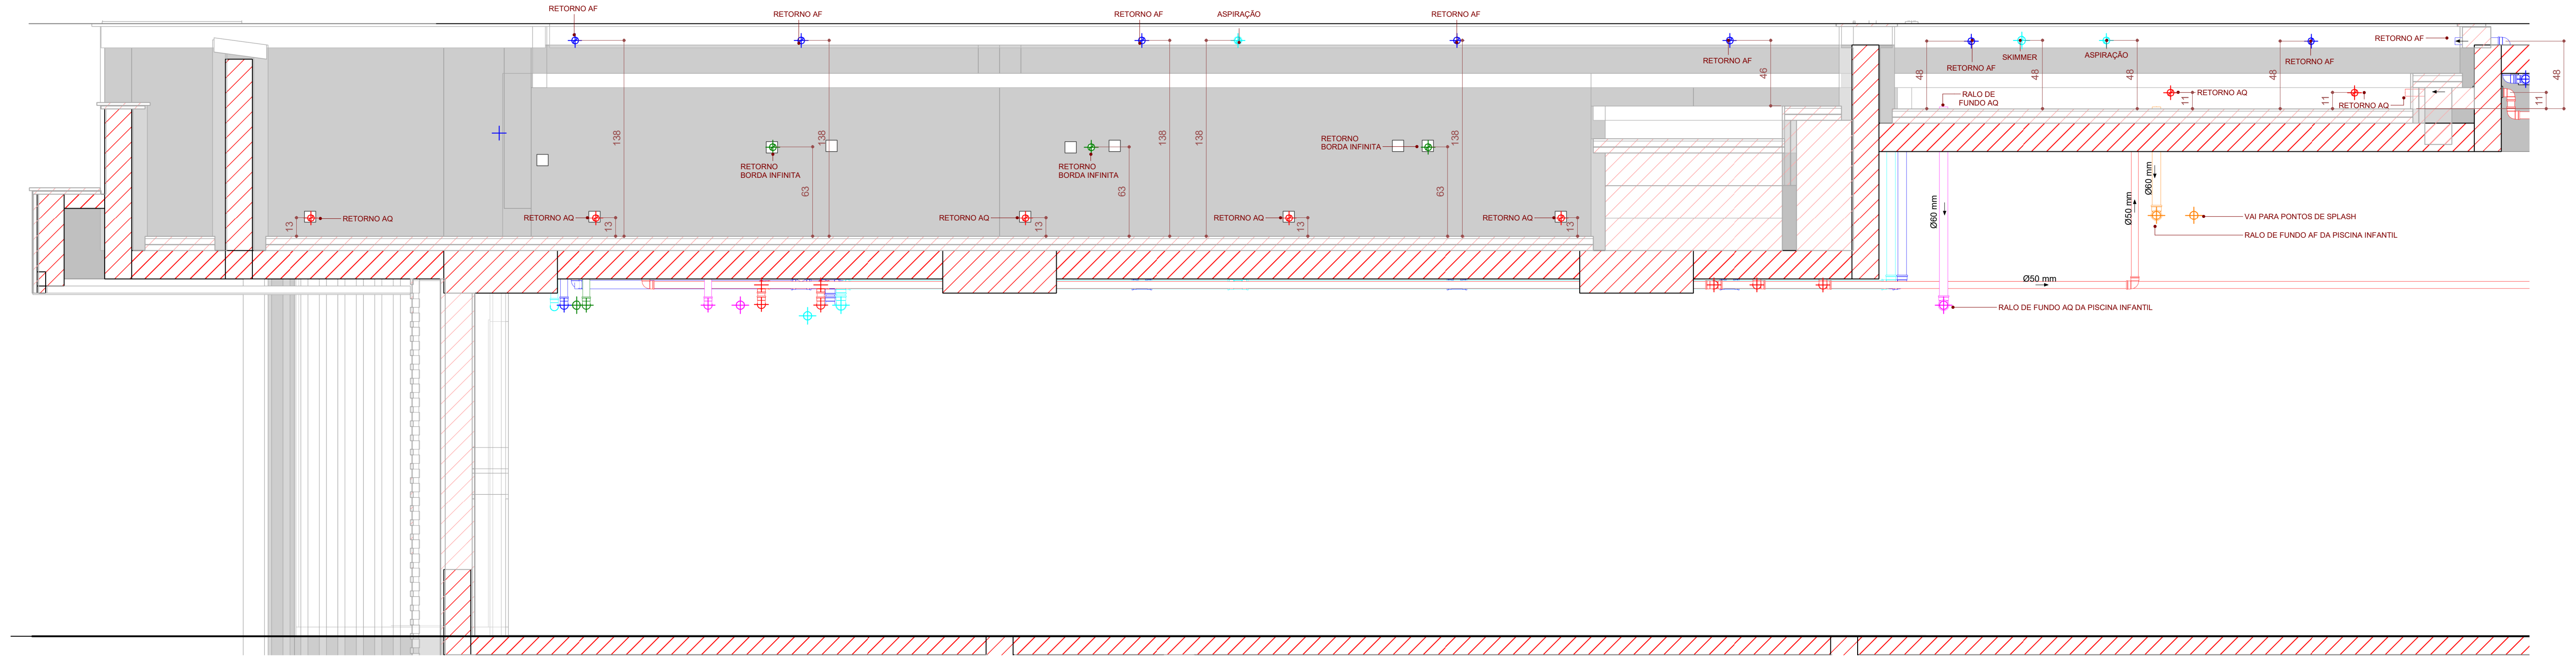
RETORNO AF
RETORNO AF
RETORNO AF
ASPIRAÇÃO
RETORNO AF
138
RETORNO BORDA INFINITA
63
RETORNO AQ
13
RETORNO AQ
RETORNO AQ
RETORNO AQ
RETORNO AQ
RETORNO AF
46
RETORNO AF
SKIMMER
ASPIRAÇÃO
RALO DE FUNDO AQ
48
RETORNO AQ
11
RETORNO AQ
RETORNO AF
RETORNO AF
48
Ø60 mm
Ø50 mm
Ø60 mm
VAI PARA PONTOS DE SPLASH
RALO DE FUNDO AF DA PISCINA INFANTIL
Ø50 mm
RALO DE FUNDO AQ DA PISCINA INFANTIL

DETALHE 06 - ALTURA DE PONTOS PISCINA ADULTO E INFANTIL
ESCALA 1:25

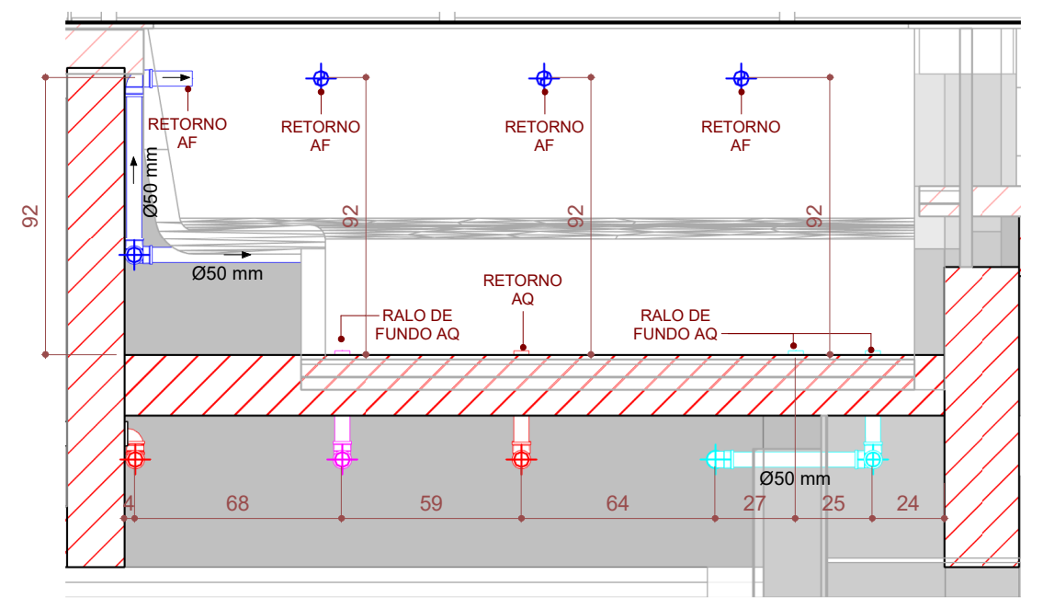
RETORNO AF
RETORNO AF
RETORNO AF
RETORNO AF
Ø50 mm
92
92
92
92
Ø50 mm
RALO DE FUNDO AQ
RETORNO AQ
RALO DE FUNDO AQ
Ø50 mm
68
59
64
27
25
24

DETALHE 07 - ALTURA DE PONTOS HIDROMASSAGEM
ESCALA 1:25

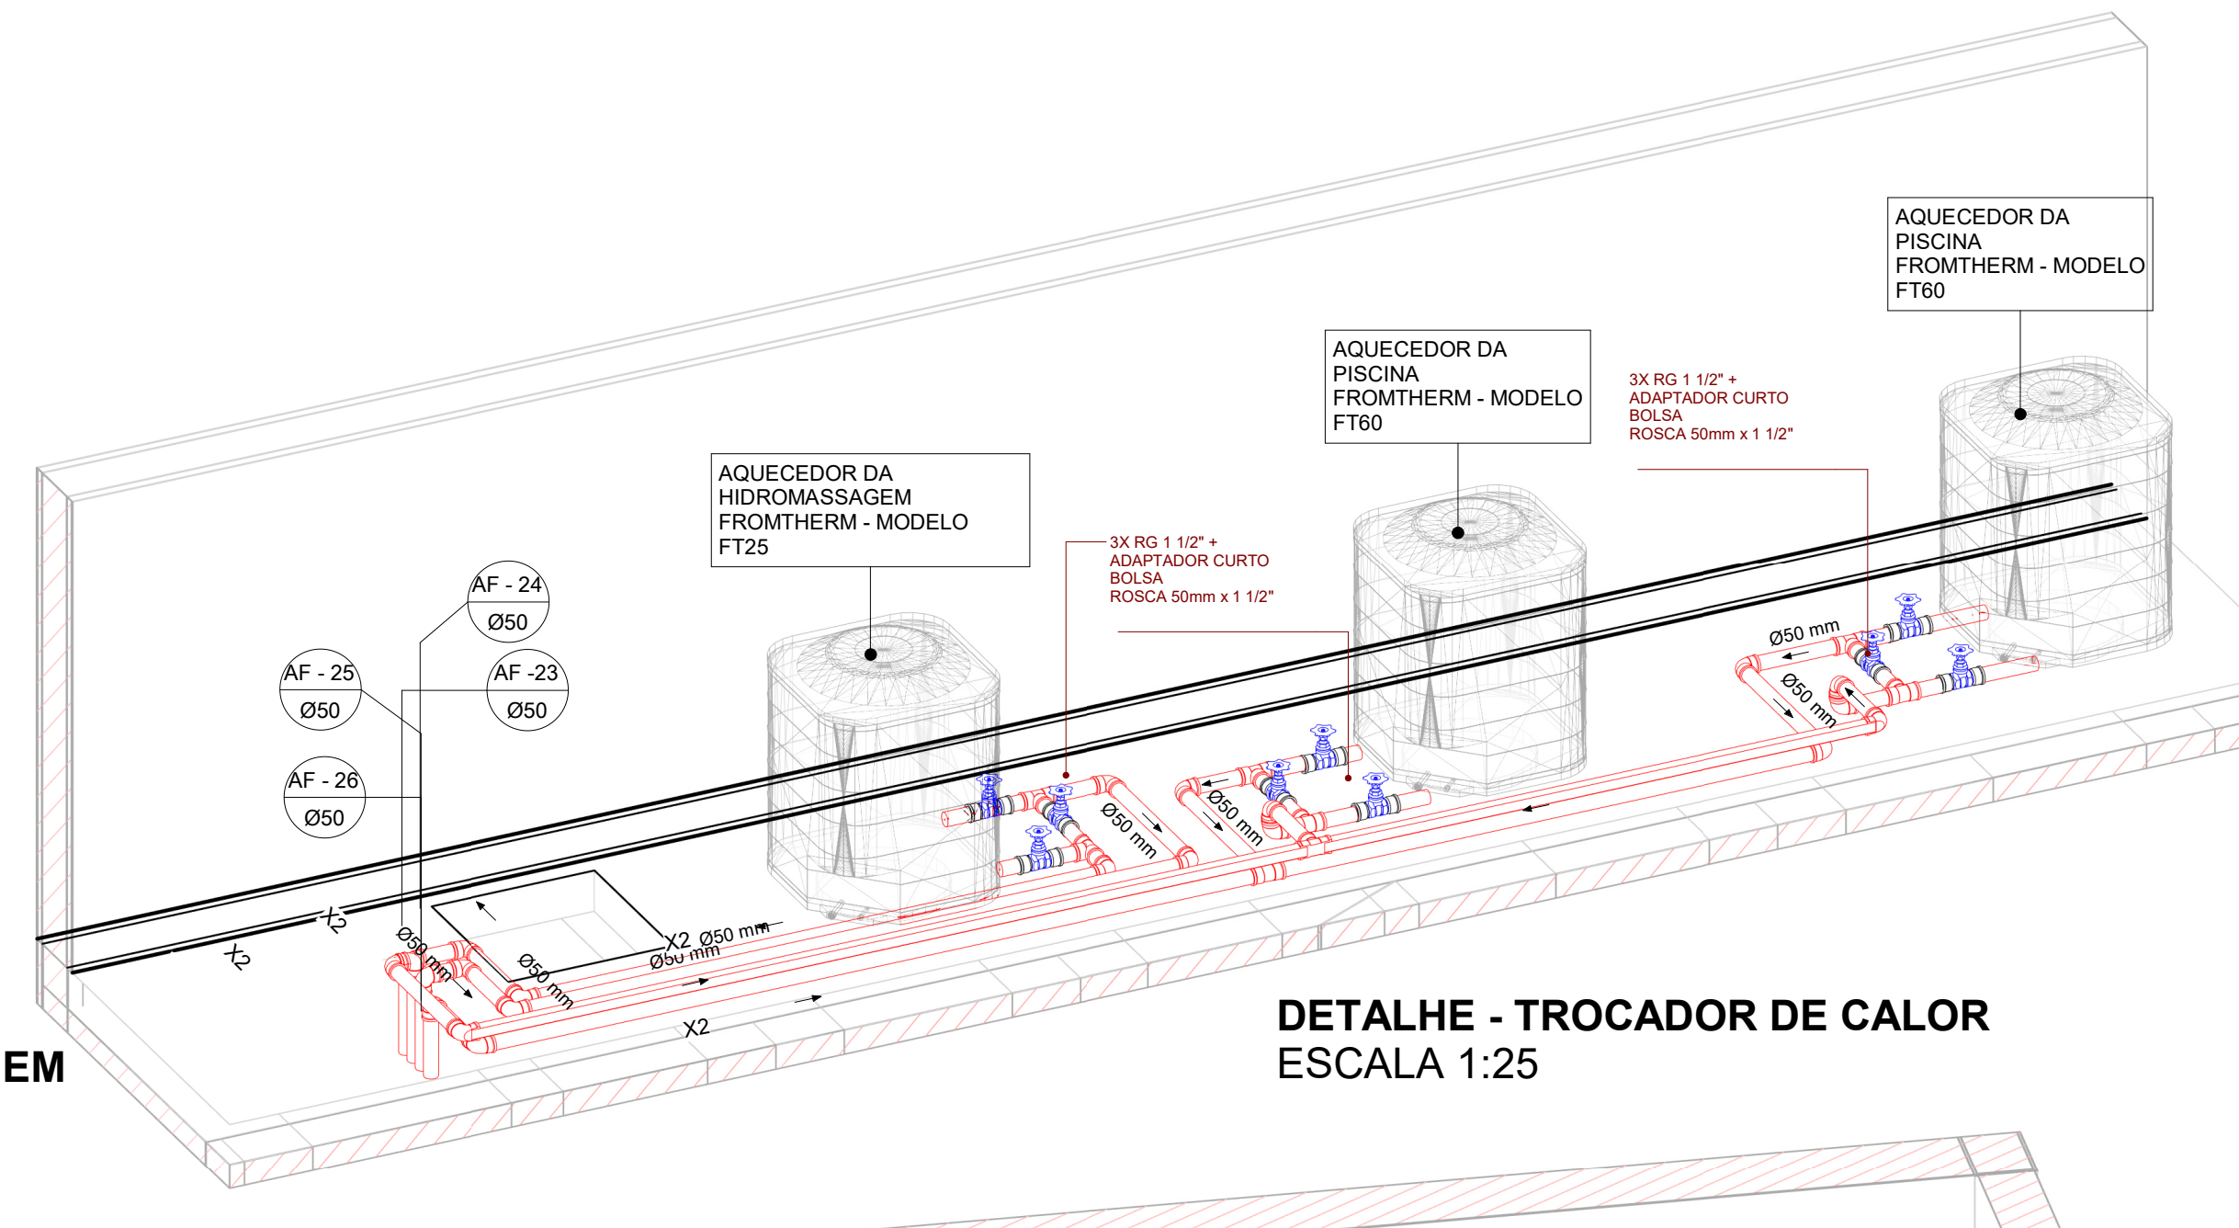
AQUECEDOR DA HIDROMASSAGEM FROMTHERM - MODELO FT25
AQUECEDOR DA PISCINA FROMTHERM - MODELO FT60
AQUECEDOR DA PISCINA FROMTHERM - MODELO FT60
3X RG 1 1/2" + ADAPTADOR CURTO BOLSA ROSCA 50mm x 1 1/2"
3X RG 1 1/2" + ADAPTADOR CURTO BOLSA ROSCA 50mm x 1 1/2"
AF - 24 Ø50
AF - 25 Ø50
AF -23 Ø50
AF - 26 Ø50
X2
X2
X2
X2
Ø50 mm
Ø50 mm
Ø50 mm
Ø50 mm
Ø50 mm

DETALHE - TROCADOR DE CALOR
ESCALA 1:25

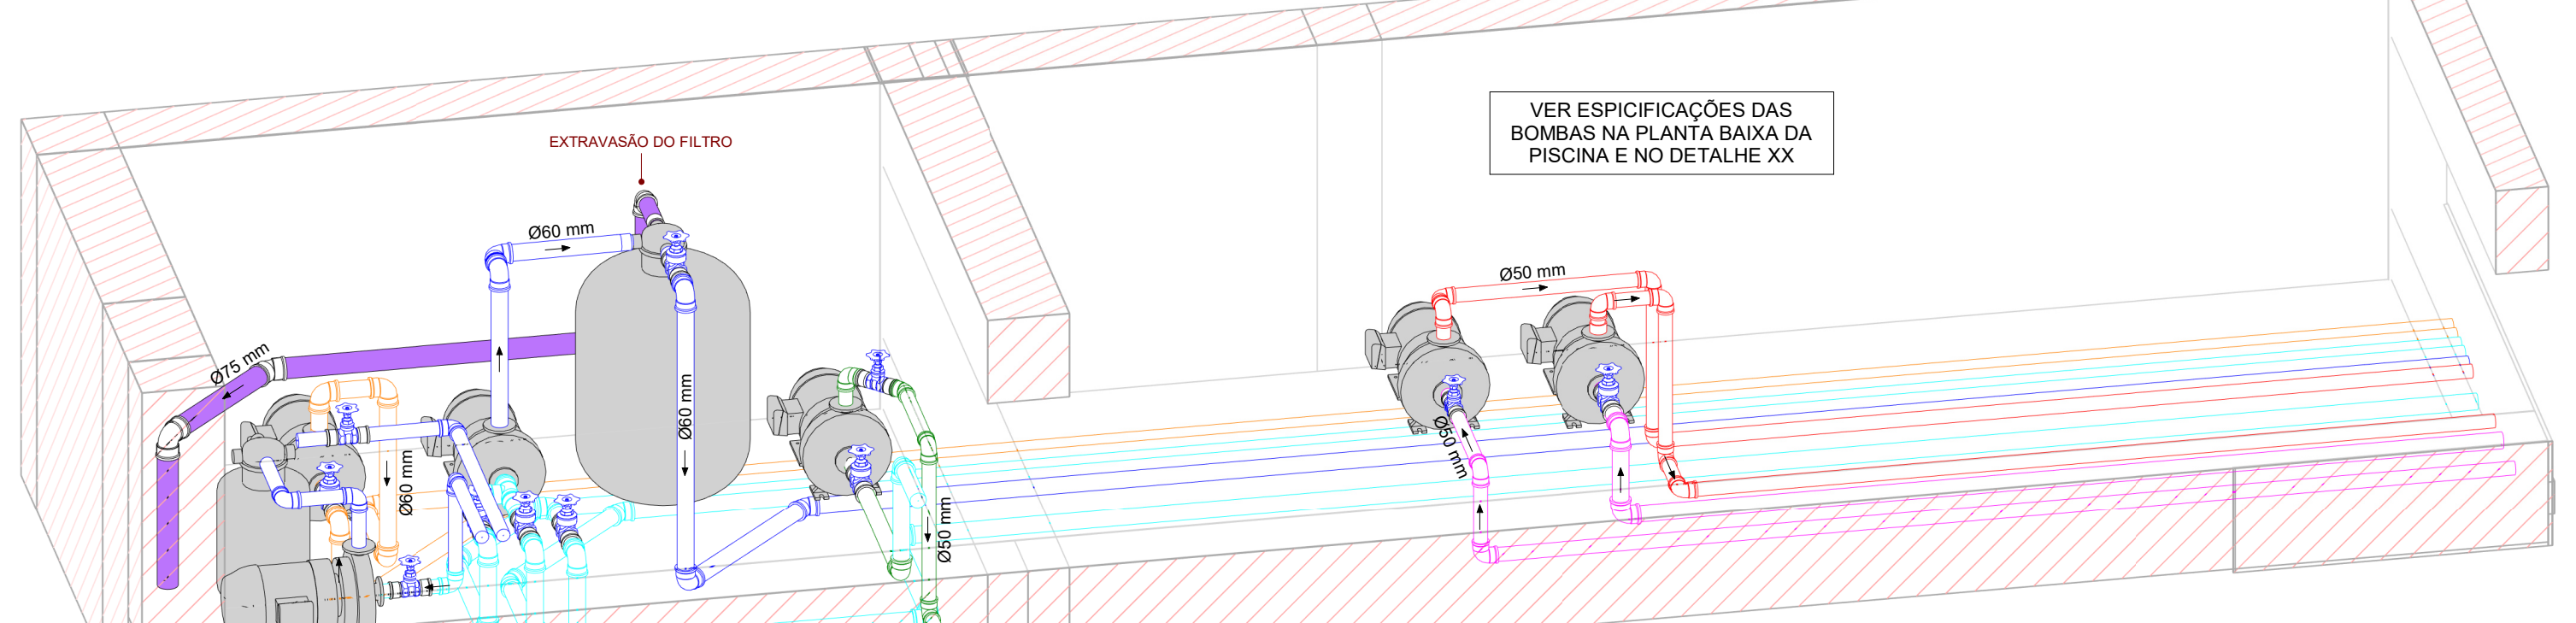
EXTRAVASÃO DO FILTRO
Ø60 mm
Ø75 mm
Ø60 mm
Ø60 mm
Ø50 mm
Ø50 mm
Ø60 mm

VER ESPICIFICAÇÕES DAS BOMBAS NA PLANTA BAIXA DA PISCINA E NO DETALHE XX

DETALHE 08 - 3D CASA DE BOMBAS DA PISCINA
ESCALA 1:25

SISTEMA PARA BORDA INFINITA
Bomba Sodramar, modelo BM-300
Potência - 3cv

SISTEMA DE FILTRAGEM PISCINA
Filtro Sodramar, modelo FM-60
Vazão - 14,1m³/h; Capacidade de filtrar 85m³ em 6h;
Bomba Sodramar, modelo BM-100
Vazão - 19,43m³/h; Potência - 1,0cv

SISTEMA PARA SPLASH PISCINA INFANTIL
Bomba Sodramar, modelo BMC-100
Potência - 1cv

SISTEMA DE AQUECIMENTO
HIDROMASSAGEM
Bomba Sodramar, modelo BM-25
Vazão - 8,83m³/h; Potência - 1/4cv

SISTEMA DE AQUECIMENTO
PISCINA ADULTO + INFANTIL
Bomba Sodramar, modelo BM-150
Vazão - 19,43m³/h; Potência - 1,0cv

RV05 - LIGAÇÃO DOS TUBOS COM FILTRO DA PISCINA

RV04 - ALTERAÇÃO NA EXTRAVASÃO DO FILTRO (CONFORME ITEM 3.5 DO RELATÓRIO DE COMPATIBILIZAÇÃO R08)

LIGA NA REDE DE DRENAGEM

Acesso 100x100

CASA DE BOMBAS DA PISCINA - VER DETALHE 05

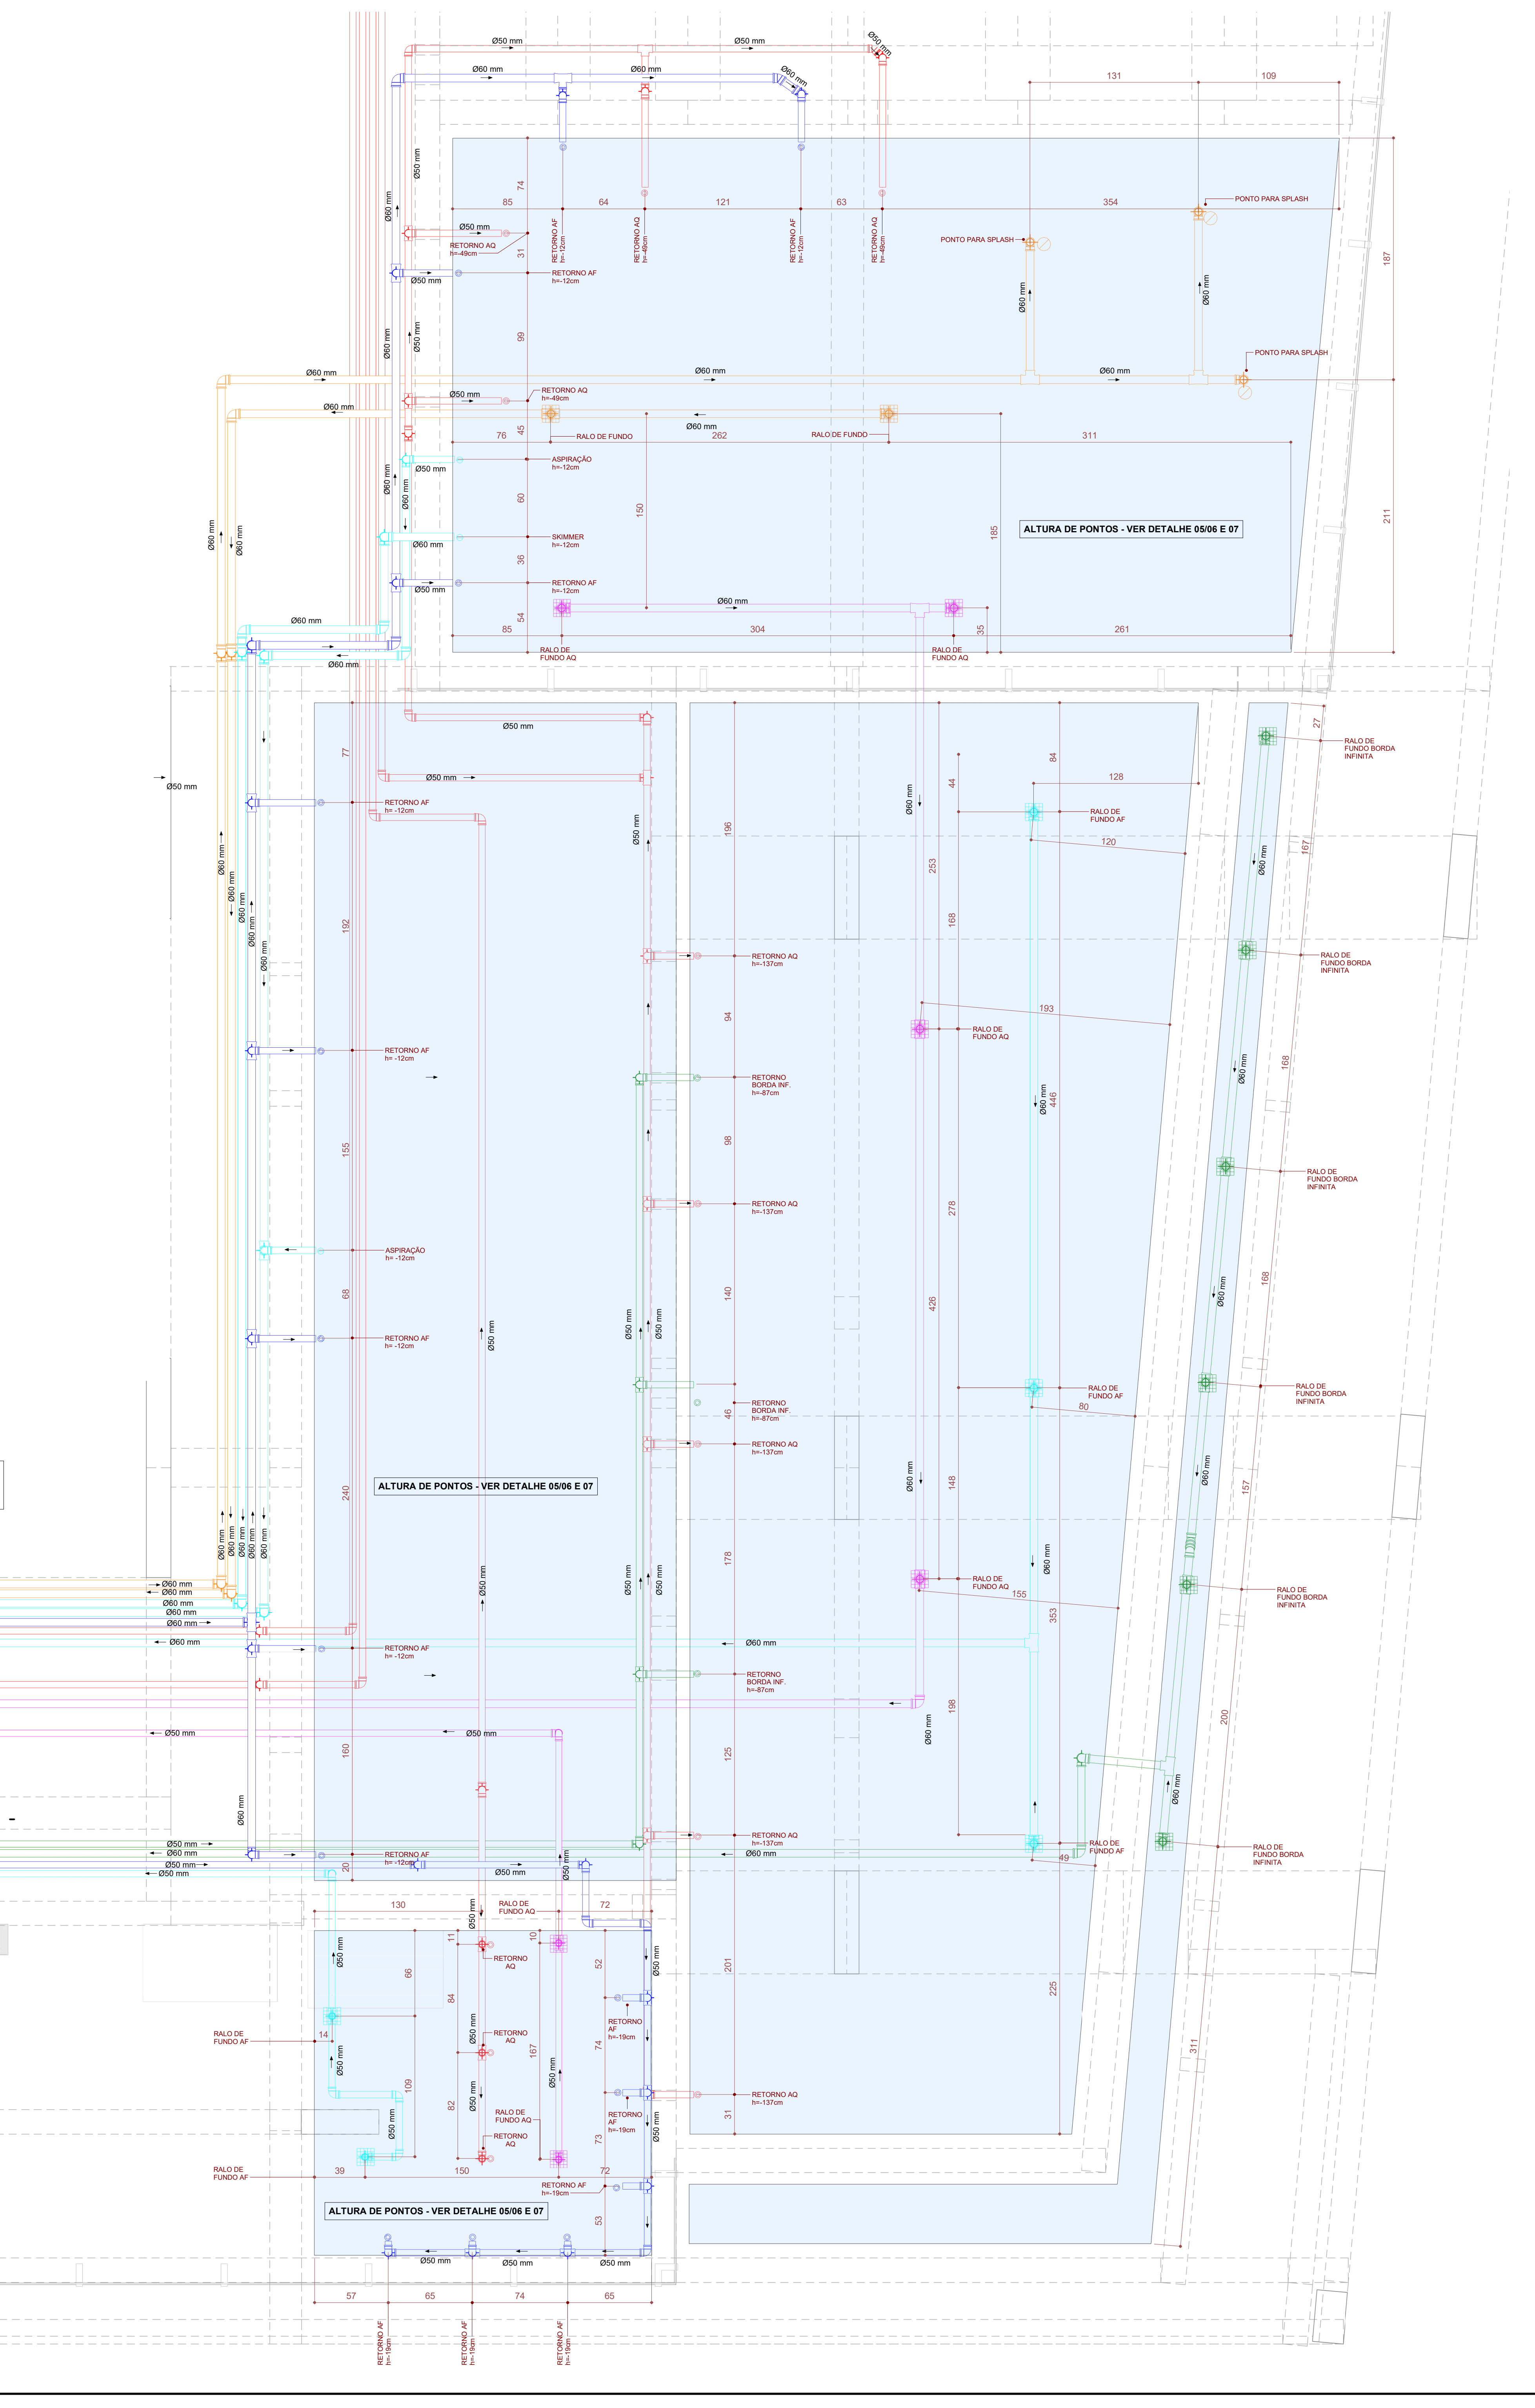
Ø50 mm
Ø60 mm
Ø50 mm
Ø60 mm
Ø60 mm
Ø50 mm
Ø60 mm
RETORNO AQ h=-49cm
RETORNO AF h=-12cm
RETORNO AQ h=-49cm
RETORNO AF h=-12cm
RETORNO AQ h=-49cm
RETORNO AF h=-12cm
RETORNO AQ h=-49cm
85
64
121
63
354
131
109
74
31
99
45
76
60
36
54
85
304
35
261
262
311
150
185
187
211
PONTO PARA SPLASH
PONTO PARA SPLASH
PONTO PARA SPLASH
RALO DE FUNDO
RALO DE FUNDO
ASPIRAÇÃO h=-12cm
SKIMMER h=-12cm
RETORNO AF h=-12cm
RALO DE FUNDO AQ
RALO DE FUNDO AQ
ALTURA DE PONTOS - VER DETALHE 05/06 E 07
Ø50 mm
RETORNO AF h= -12cm
ASPIRAÇÃO h= -12cm
RETORNO AF h= -12cm
RETORNO AF h= -12cm
RETORNO AF h= -12cm
77
192
155
68
240
160
20
RALO DE FUNDO AF
RALO DE FUNDO AF
RALO DE FUNDO AQ
RALO DE FUNDO AQ
RETORNO AQ h=-137cm
RETORNO BORDA INF. h=-87cm
RETORNO AQ h=-137cm
RETORNO BORDA INF. h=-87cm
RETORNO AQ h=-137cm
RETORNO BORDA INF. h=-87cm
RETORNO AQ h=-137cm
RETORNO AQ h=-137cm
196
94
98
140
46
178
125
201
31
84
128
44
120
253
168
193
446
278
426
148
155
80
353
198
49
225
RALO DE FUNDO BORDA INFINITA
RALO DE FUNDO BORDA INFINITA
RALO DE FUNDO BORDA INFINITA
RALO DE FUNDO BORDA INFINITA
RALO DE FUNDO BORDA INFINITA
27
167
168
168
157
200
311
ALTURA DE PONTOS - VER DETALHE 05/06 E 07
ALTURA DE PONTOS - VER DETALHE 05/06 E 07
130
72
RALO DE FUNDO AQ
RETORNO AQ
RETORNO AQ
RETORNO AQ
RALO DE FUNDO AQ
RETORNO AF h=-19cm
RETORNO AF h=-19cm
RETORNO AF h=-19cm
RETORNO AF h=-19cm
RETORNO AF h=-19cm
RETORNO AF h=-19cm
RALO DE FUNDO AF
RALO DE FUNDO AF
11
66
84
14
109
82
167
10
52
74
73
72
39
150
53
57
65
74
65

PLANTA BAIXA - PISCINA
ESCALA 1:25

LEGENDA

—	TUBO DE RETORNO ÁGUA FRIA DA PISCINA E HIDRO - PVC - DIÂMETRO INDICADO	—	TUBO DE RETORNO ÁGUA QUENTE PVC - DIÂMETRO INDICADO
—	TUBO DE SUCÇÃO ÁGUA FRIA DA PISCINA E HIDRO - PVC - DIÂMETRO INDICADO	—	TUBO DE SUCÇÃO ÁGUA QUENTE PVC - DIÂMETRO INDICADO
—	TUBO DO SISTEMA DE BORDA INFINITA PVC - DIÂMETRO INDICADO	—	TUBO DO SISTEMA DE CHAFARIZ PVC - DIÂMETRO INDICADO
▦	DRENO DE FUNDO PARA BORDA INFINITA VER ESPECIFICAÇÃO EM NOTA	◎	DISP. DE RETORNO SISTEMA DE FILTRAGEM VER ESPECIFICAÇÃO EM NOTA
▦	DRENO DE FUNDO SISTEMA DE FILTRAGEM VER ESPECIFICAÇÃO EM NOTA	◎	DISP. DE RETORNO BORDA INFINITA VER ESPECIFICAÇÃO EM NOTA
▦	DRENO DE FUNDO SIST. DE AQUECIMENTO VER ESPECIFICAÇÃO EM NOTA	◎	DISP. DE RETORNO SIST. DE AQUECIMENTO VER ESPECIFICAÇÃO EM NOTA
▦	DRENO DE FUNDO SIST. DE CHAFARIZ VER ESPECIFICAÇÃO EM NOTA	⊘	PONTO PARA CHAFARIZ VER ESPECIFICAÇÃO CONF. FORNECEDOR
⊖	DISP. DE ASPIRAÇÃO - MANTER FECHADO VER ESPECIFICAÇÃO EM NOTA	▬	FURO NA VIGA CONFORME PROJETO ESTRUTURAL

QUADRO ESPECIFICAÇÕES

RALOS DE FUNDO

- Ralo de fundo Cego Antiaprisionamento - Cristal LED - Monobloco de Aço Inox 304L - 150x150mmxØ50mm ou similar
OBRIGATÓRIO DISPOSITIVO ANTI-APRISIONAMENTO

DISPOSITIVOS DE RETORNOS

- Dispositivo de retorno Cristal LED - Aço Inox 304L - Ø72x50mm ou similar

DISPOSITIVOS DE ASPIRAÇÃO

- Dispositivo de aspiração 50mm Cristal LED - Aço Inox 304L - Ø82x50mm ou similar

DISPOSITIVO DE SUCÇÃO

- Dispositivo anti-turbilhonamento Cristal LED - Aço Inox 304L - Quadrado 82x82xØ50mm ou similar
OBRIGATÓRIO DISPOSITIVO ANTI-SUCÇÃO

BOMBAS

- Bomba com pré-filtro BM 100 1,0cv - Sodramar ou similar - Sistema de aquecimento da piscina
- Bomba com pré-filtro BM 100 1,0cv - Sodramar ou similar - Sistema de filtragem piscina adulto e infantil
- Bomba com pré-filtro BM 25 1/4cv - Sodramar ou similar - Sistema de filtragem hidromassagem
- Bomba com pré-filtro BM 25 1/4cv - Sodramar ou similar - Sistema de aquecimento hidromassagem
- Bomba com pré-filtro BM 300 3cv - Sodramar ou similar - Sistema de borda infinita
- Bomba com pré-filtro BMC 100 1cv - Sodramar ou similar - Sistema de chafariz

FILTROS DE AREIA

- Fitro de areia FM-60 - Sodramar ou similar - Sistema de filtragem da piscina
- Fitro de areia FM-25 - Sodramar ou similar - Sistema de filtragem da hidromassagem

CARACTERISTICA DA PISCINA

- Volume Piscina Adulto+Infantil: 75,4m³
- Volume borda infinita: 2,5m³
- Volume Hidromassagem: 5,2m³

TROCADOR DE CALOR

- FT20 Fronttherm - 20.000 BTU/h ou Similar (Hidromassagem)
- FT100 Fronttherm - 100.000 BTU/h ou Similar (Piscina Adulto e Infantil)

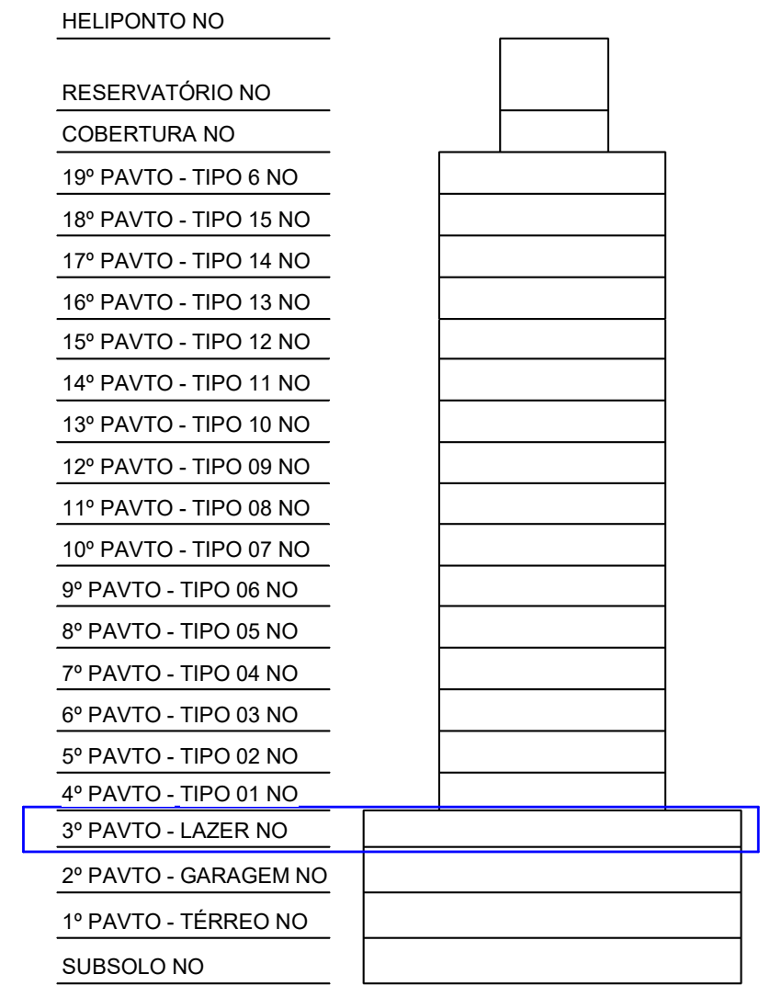
HELIPONTO NO
RESERVATÓRIO NO
COBERTURA NO
19º PAVTO - TIPO 6 NO
18º PAVTO - TIPO 15 NO
17º PAVTO - TIPO 14 NO
16º PAVTO - TIPO 13 NO
15º PAVTO - TIPO 12 NO
14º PAVTO - TIPO 11 NO
13º PAVTO - TIPO 10 NO
12º PAVTO - TIPO 09 NO
11º PAVTO - TIPO 08 NO
10º PAVTO - TIPO 07 NO
9º PAVTO - TIPO 06 NO
8º PAVTO - TIPO 05 NO
7º PAVTO - TIPO 04 NO
6º PAVTO - TIPO 03 NO
5º PAVTO - TIPO 02 NO
4º PAVTO - TIPO 01 NO
3º PAVTO - LAZER NO
2º PAVTO - GARAGEM NO
1º PAVTO - TÉRREO NO
SUBSOLO NO

ESQUEMA DE PAVIMENTOS

ARQUIVO BASE	NOME DO ARQUIVO	RECEBIDO EM
PROJETO ARQUITETÔNICO	179_EX_SUN SET TOWER_VETTER_R07	26/06/2020
PROJETO ESTRUTURAL - IFC	E877-Sunset Tower 23-06-2020	23/06/2020
PROJETO ESTRUTURAL - DWG		

	RESPONSÁVEL PELA RESPOSTA	RECEBIDO EM
LISTA DE DEFINIÇÕES		
FUROS APROVADOS		

REVISÃO	DATA	DESCRIÇÃO	RESPONSÁVEL
RV05	20/04/2022	CONEXÃO DAS TUBULAÇÕES COM FILTRO - PISCINA	JÉSSICA
RV04	14/04/2022	AJUSTES CONFORME RELATÓRIO DE COMPATIBILIZAÇÃO R08	JÉSSICA
RV03	18/03/2022	AJUSTE TROCADOR DE CALOR PISCINA	NAIARA
RV02	15/10/2020	AJUSTES GERAIS	LUANI
RV01	30/06/2020	FASE 03 - LIBERADO PARA OBRA	LUANI

THÓRUS ENGENHARIA

EQUIPE TÉCNICA:
AMANDA LARENTIS
ENG. CIVIL - CREA SC 126.082-4
RAUL PEDRO ESKELSEN
ENG. ELETRICISTA - CREA/SC 149.963-2
RAFAEL ANTON
ENG. CIVIL - CREA SC 160.962-4

RUA DR. JOÃO COLIN, 1.872, SL 32
BAIRRO AMÉRICA | JOINVILLE-SC
FONE: (47) 3043 6643

AV. DO ESTADO DALMO VIEIRA, 1900, SL 32
BAIRRO ARIRIBÁ | BALNEÁRIO CAMBORIÚ-SC
FONE: (47) 3046 8227

THORUSENGENHARIA.COM.BR
PROJETOS@THORUSENGENHARIA.COM.BR

PROJETO HIDRÁULICO

OBRA
EDIFÍCIO SUNSET TOWER

ENDEREÇO
RUA 3020 - LT. JARDIM AVIADOR - BAIRRO ITACOLOMI - BALNEÁRIO PIÇARRAS/SC.

PROPRIETÁRIO
VETTER EMPREENDIMENTOS LTDA

CONTEÚDO
PLANTA BAIXA - PISCINA; DETALHES PISCINA E CASA DE BOMBAS

HID
09 | 12

PROJETO	REVISOR	FASE DO PROJETO	ESCALA	DATA	REVISÃO	ARQUIVO
LUANI	ALLAN	FASE 03	INDICADA	20/04/2022	RV05	19025

DIREITOS AUTORAIS RESERVADOS - PROIBIDA A REPRODUÇÃO OU UTILIZAÇÃO SEM AUTORIZAÇÃO.