


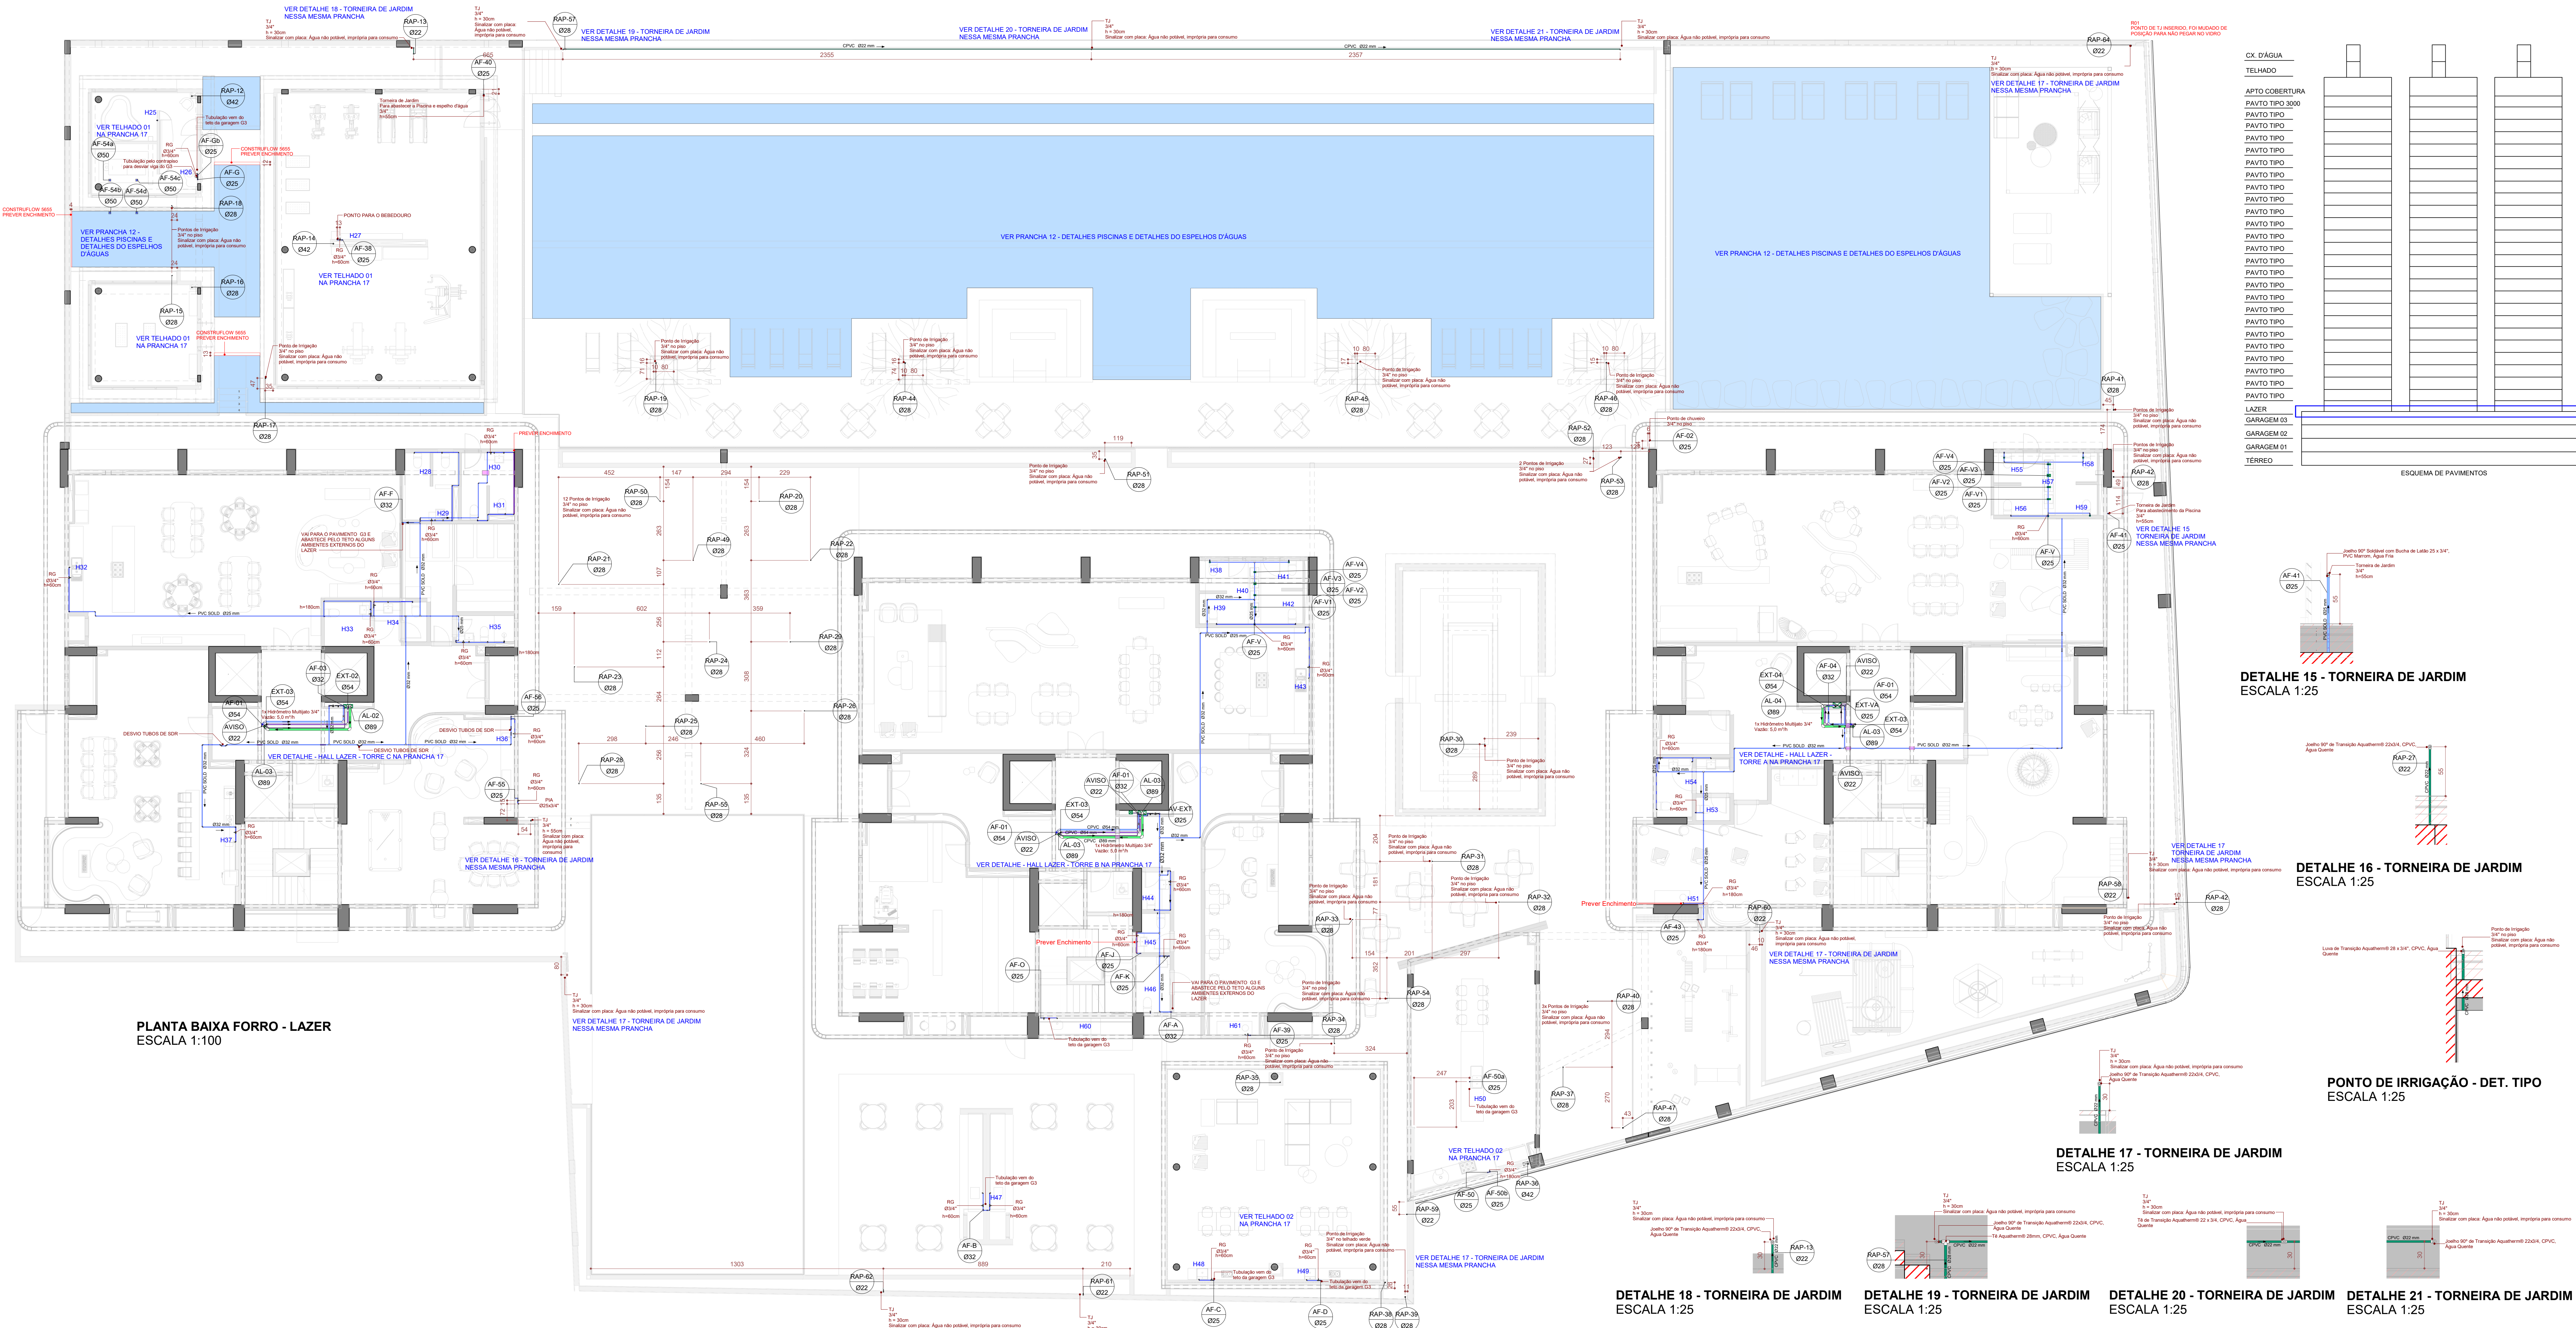

PLANTA BAIXA FORRO - LAZER
ESCALA 1:100

DETALHE 15 - TORNEIRA DE JARDIM
ESCALA 1:25

DETALHE 16 - TORNEIRA DE JARDIM
ESCALA 1:25

PONTO DE IRRIGAÇÃO - DET. TIPO
ESCALA 1:25

DETALHE 17 - TORNEIRA DE JARDIM
ESCALA 1:25

DETALHE 18 - TORNEIRA DE JARDIM
ESCALA 1:25

DETALHE 19 - TORNEIRA DE JARDIM
ESCALA 1:25

DETALHE 20 - TORNEIRA DE JARDIM
ESCALA 1:25

DETALHE 21 - TORNEIRA DE JARDIM
ESCALA 1:25

LEGENDA

TUBO DE ALIMENTAÇÃO - AL MATERIAL(CPVC/PPR/PE DIÂMETRO INDICADOS)	TUBO DE LIMPEZA E EXTRAVASÃO MATERIAL E DIÂMETRO INDICADOS
TUBO DE ÁGUA FRIA - AF MATERIAL(PPR/PPVC/PE DIÂMETRO INDICADOS)	TUBO DE ÁGUA QUENTE - AQ CPVC - DIÂMETRO INDICADO
TUBO DE REAPROVEITAMENTO (PVC/CPVC) - DIÂMETRO INDICADO	TUBO ENTERRADO - SISTEMA CONFORME COLORAÇÃO INDICADA
SHAFT HIDROSSANITÁRIO	TUBO DE SUÇÃO AF DA PISCINA PVC - DIÂMETRO INDICADO
TUBO DE RETORNO ÁGUA FRIA DA PISCINA PVC - DIÂMETRO INDICADO	FURO EM VIGA
REGISTRO DE RETORNO DE ÁGUA QUENTE - AQ CPVC - DIÂMETRO INDICADO	

CH	CHUVEIRO h= 210cm	GE	GELADEIRA h= 110cm
PIA	PIA DE COZINHA h= 60cm	MLR	MÁQUINA DE LAVAR ROUPA h= 60cm
LV	LAVATÓRIO h= 60cm	TLR	TANQUE DE LAVAR ROUPA h= 50cm
RP	REGISTRO DE PRESSÃO h= 110cm	VS	VASO SANITÁRIO COM CAIXA ACOPLADA h= 20cm
DH	DUCHA HIGIÊNICA h= 50cm	MLL	MÁQUINA DE LAVAR LOUÇAS h= 20cm
MON	MONITORAMENTO h= 110cm	VR	VÁLVULA DE RETENÇÃO
RG	REGISTRO DE GAVETA	TJ	TORNEIRA DE JARDIM h= 60cm

LEGENDA DE TUBOS DE QUEDA

AL 00	ALIMENTAÇÃO	AF 00	ÁGUA FRIA
AVISO	AVISO DE EXTRAVASÃO	RAP 00	REAPROVEITAMENTO
EXT	EXTRAVASÃO	REC 00	RECALQUE/SUÇÃO

OBSERVAÇÕES DE PROJETO:
NOTA 01: ESTE PROJETO FOI PROJETADO E DIMENSIONADO COM UMA VIDA ÚTIL DE PROJETO DE 20 ANOS DE FORMA QUE ATENDA OS REQUISITOS MÍNIMOS DE DESEMPENHO DA NBR 15575, SUPONDO O ATENDIMENTO DA PERIODICIDADE E CORRETA EXECUÇÃO DOS PROCESSOS DE MANUTENÇÃO.

ARQUIVO BASE	NOME DO ARQUIVO	RECEBIDO EM
PROJETO ARQUITETÔNICO	BOC-EXE-ARG-EMB	04-12-2023
PROJETO ESTRUTURAL - IFC	BOC-EST-EXE-MOD (A,B,C,D)	18-04-2024
PROJETO ESTRUTURAL - DWG		

	RESPONSÁVEL PELA RESPOSTA	RECEBIDO EM
LISTA DE DEFINIÇÕES	EDUARDO E THAMYRA	11-02-2022
FUROS APROVADOS		

REVISÃO

R04	30-08-2024	INSERÇÃO DOS DESVIOS DAS PRUMADAS HIDRAULICAS QUE VEM DA TORRE E DESCEM NO LAZER DAS TORRES A E C	ANGÉLICA
R03	01-12-2023	AJUSTES CONFORME RELATÓRIO DE ANÁLISE 25-07-23*	NAIARA
R02	27-04-2023	AJUSTE CONFORME RELATÓRIO E CONSTRUTIFLOW	PEDRO
R01	03-03-2023	REVISÃO GERAL CONFORME RELATÓRIO E CONSTRUTIFLOW	PEDRO
R00	16-12-2022	EXECUTIVO - EMISSÃO INICIAL	PEDRO

REVISÃO

REVISÃO	DATA	DESCRIÇÃO	RESPONSÁVEL
---------	------	-----------	-------------

thórus

engenharia

PROJETO HIDRÁULICO

CIPA
BRAVA OCEAN

PROPRIETÁRIO
CN CONSTRUTORA E INCORP. LTDA

CONTEÚDO
PLANTA BAIXA FORRO - LAZER

PROJETO TÉCNICO
AMANDA LARENTIS
DRA. CIVIL - CRB 001.254
GUILLERME LARENTIS
DRA. MECÂNICO - CREA: 187.225-9
RAUL PEDRO ESKELEN
DRA. ELÉTRICO - CREA: 188.003-2
PROJETO: THORUS ENGENHARIA.COM.BR

RUA DA JARDIM COLINA, 1.386
VILA CONCEIÇÃO
BARRO ANDARAÍ, JARDIM L. G. C.
FONE: (41) 3081-8800
RUA 3.300, 34 - SL. 12 E 13
JARDIM CONCEIÇÃO, CENTRO
BARRO ANDARAÍ, PARANÁ 81.600-000
BARRO ANDARAÍ, PARANÁ 81.600-000
PROJETO: THORUS ENGENHARIA.COM.BR

PROPRIETÁRIO
CN CONSTRUTORA E INCORP. LTDA

CONTEÚDO
PLANTA BAIXA FORRO - LAZER

HID
06 | 19

PROJETO: JESSICA

REVISÃO: ANGÉLICA

FASE DO PROJETO: EXECUTIVO

ESCALA: INDICADA

DATA: 30-08-2024

REVISÃO: R04

ARQUIVO: 0005