


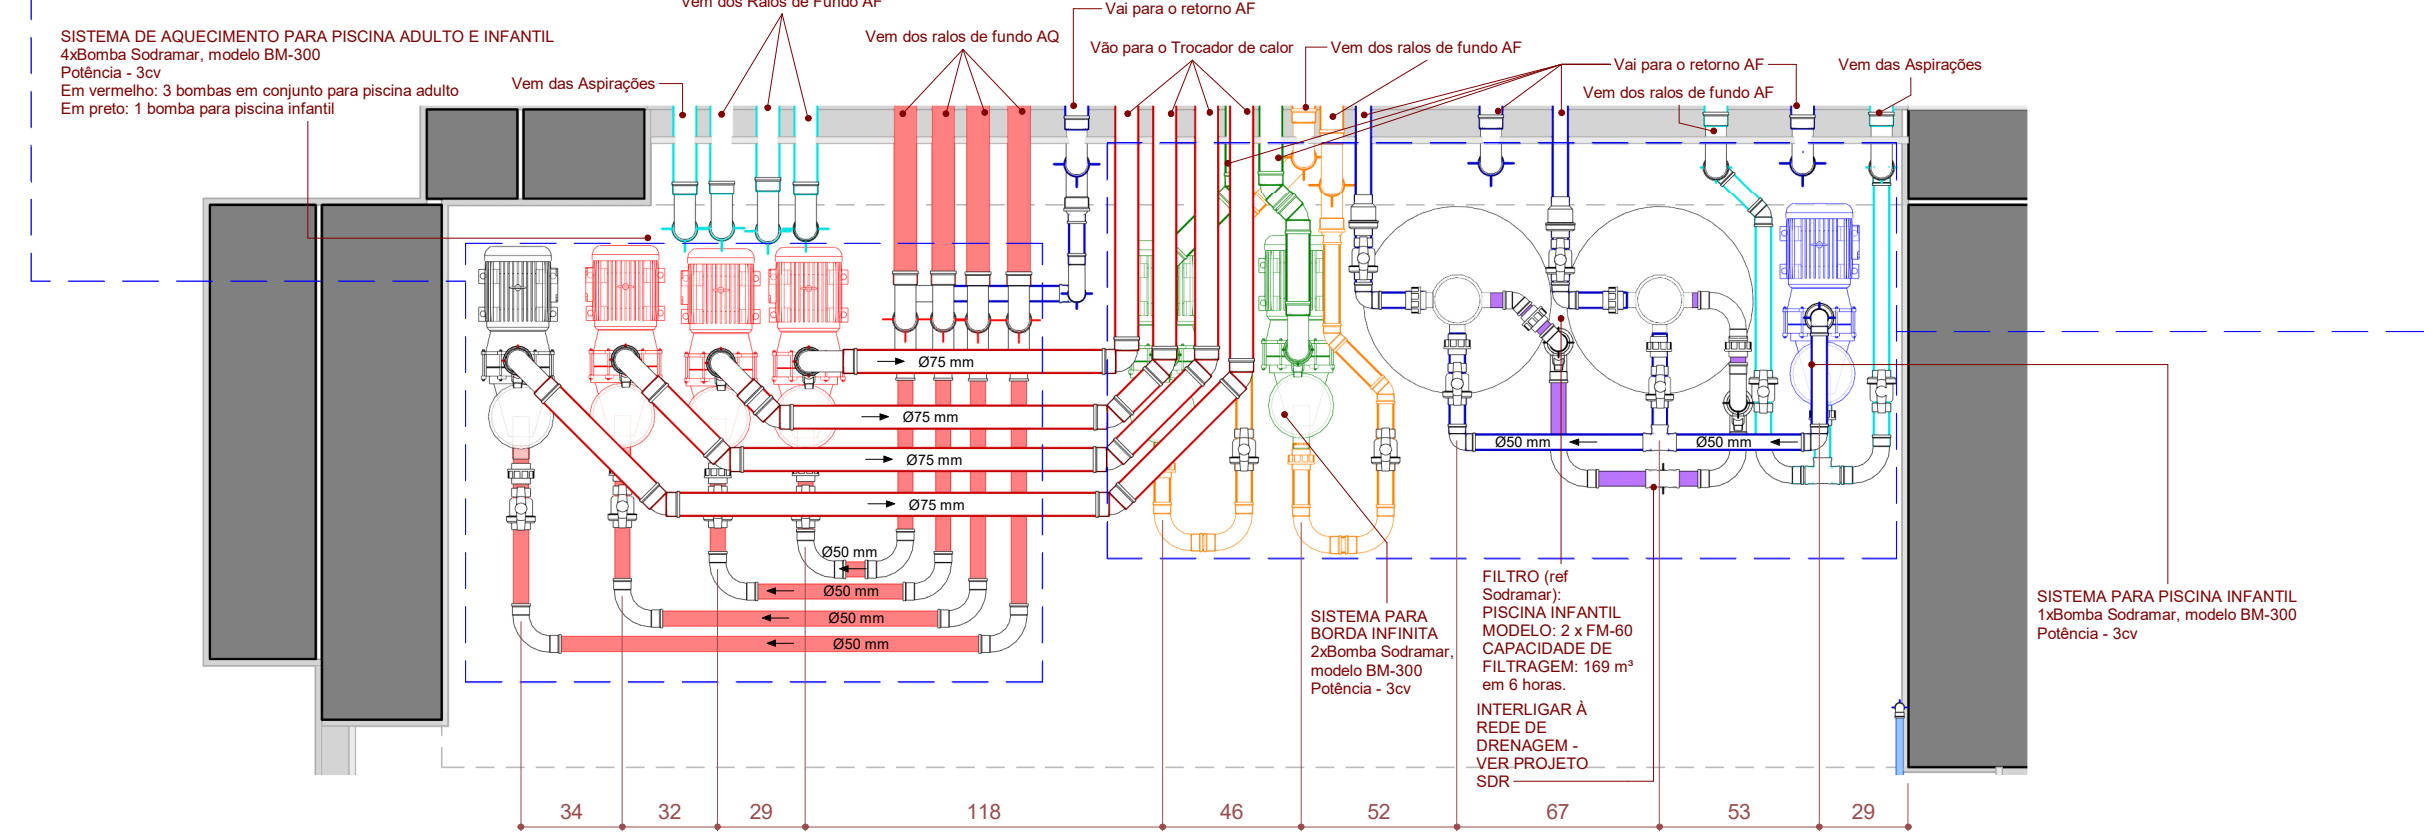
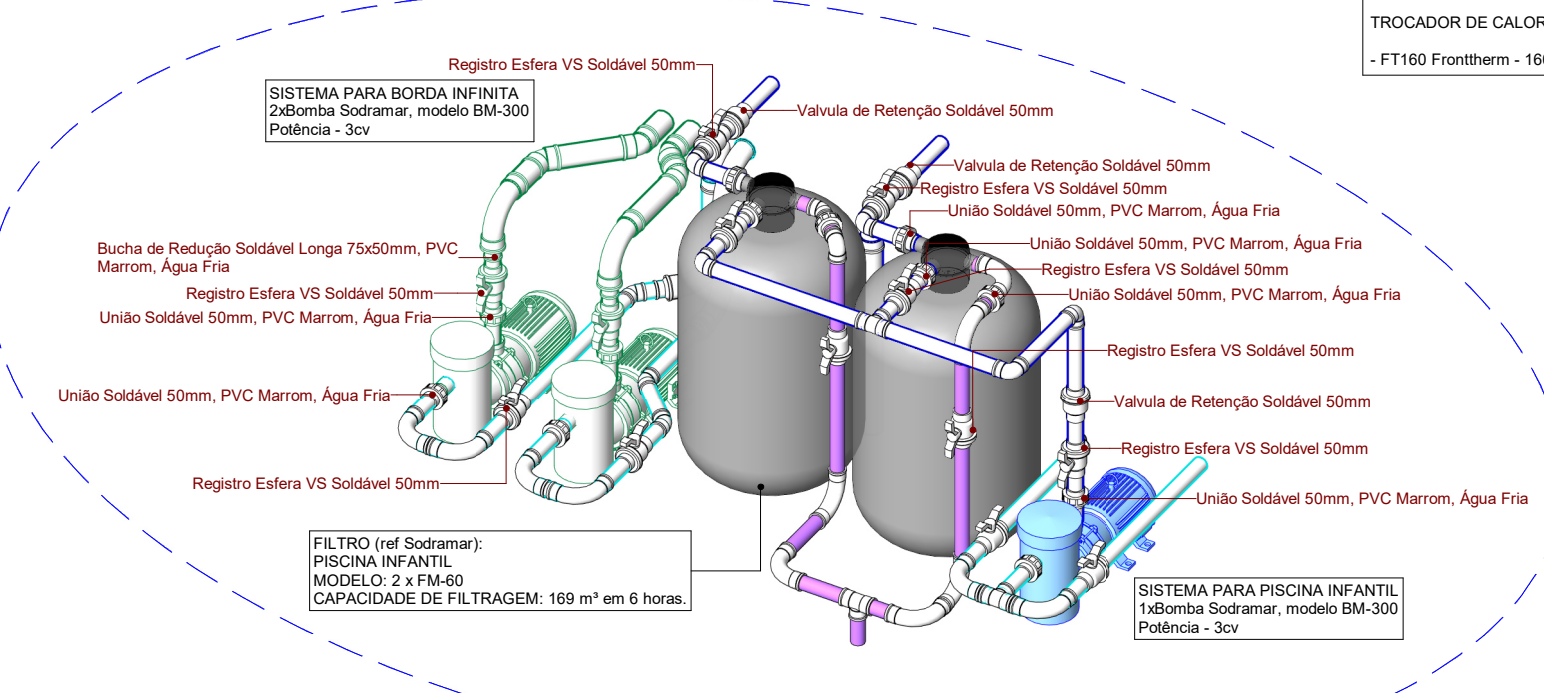


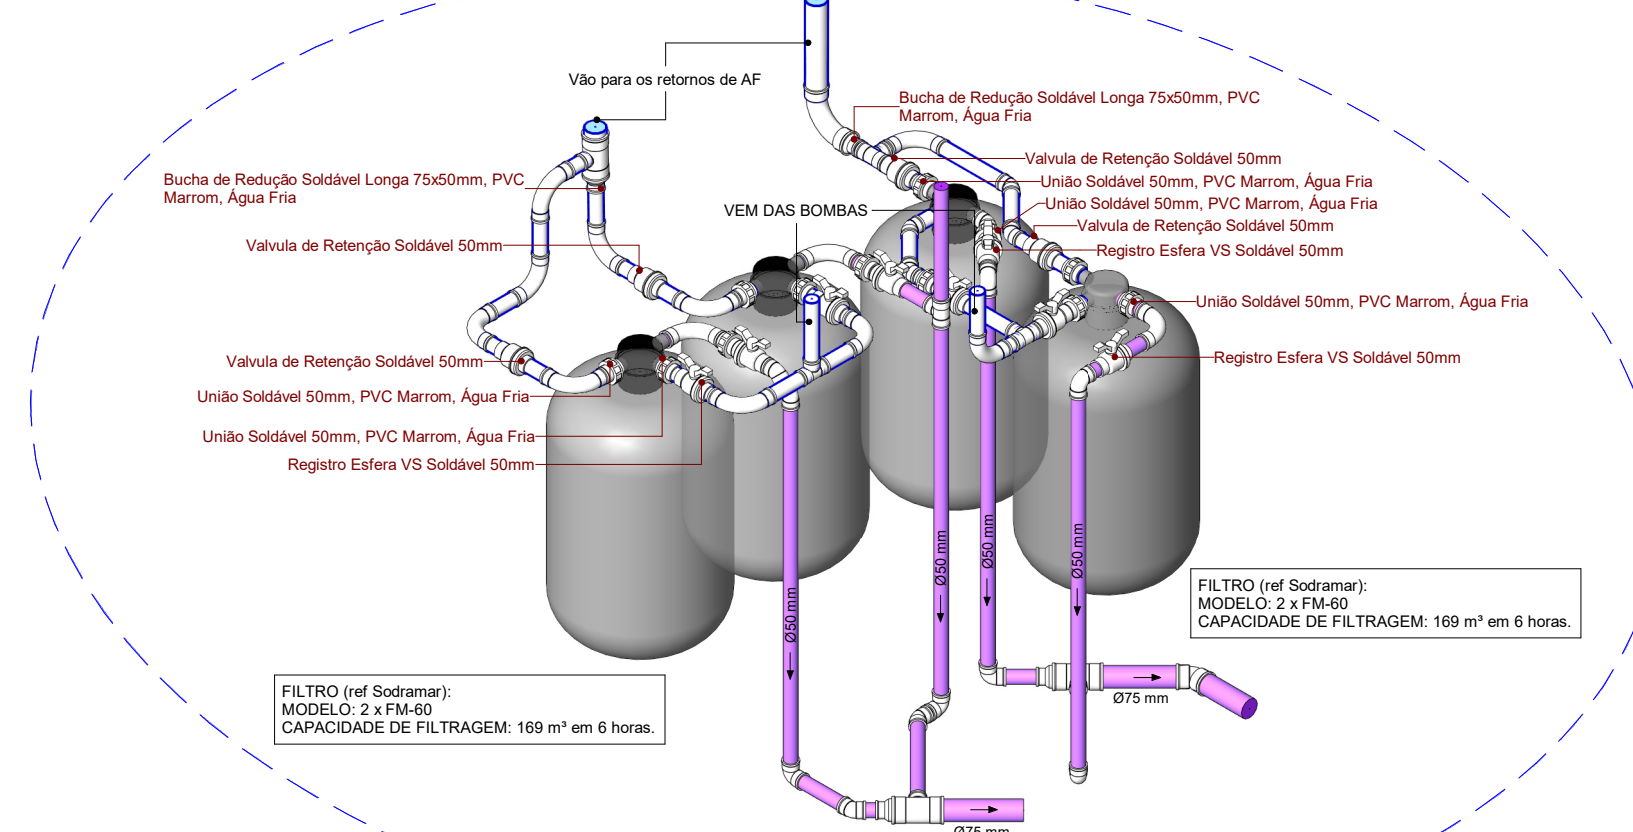

**PLANTA BAIXA - CASA DE MÁQUINAS SUPERIOR**  
ESCALA 1:25

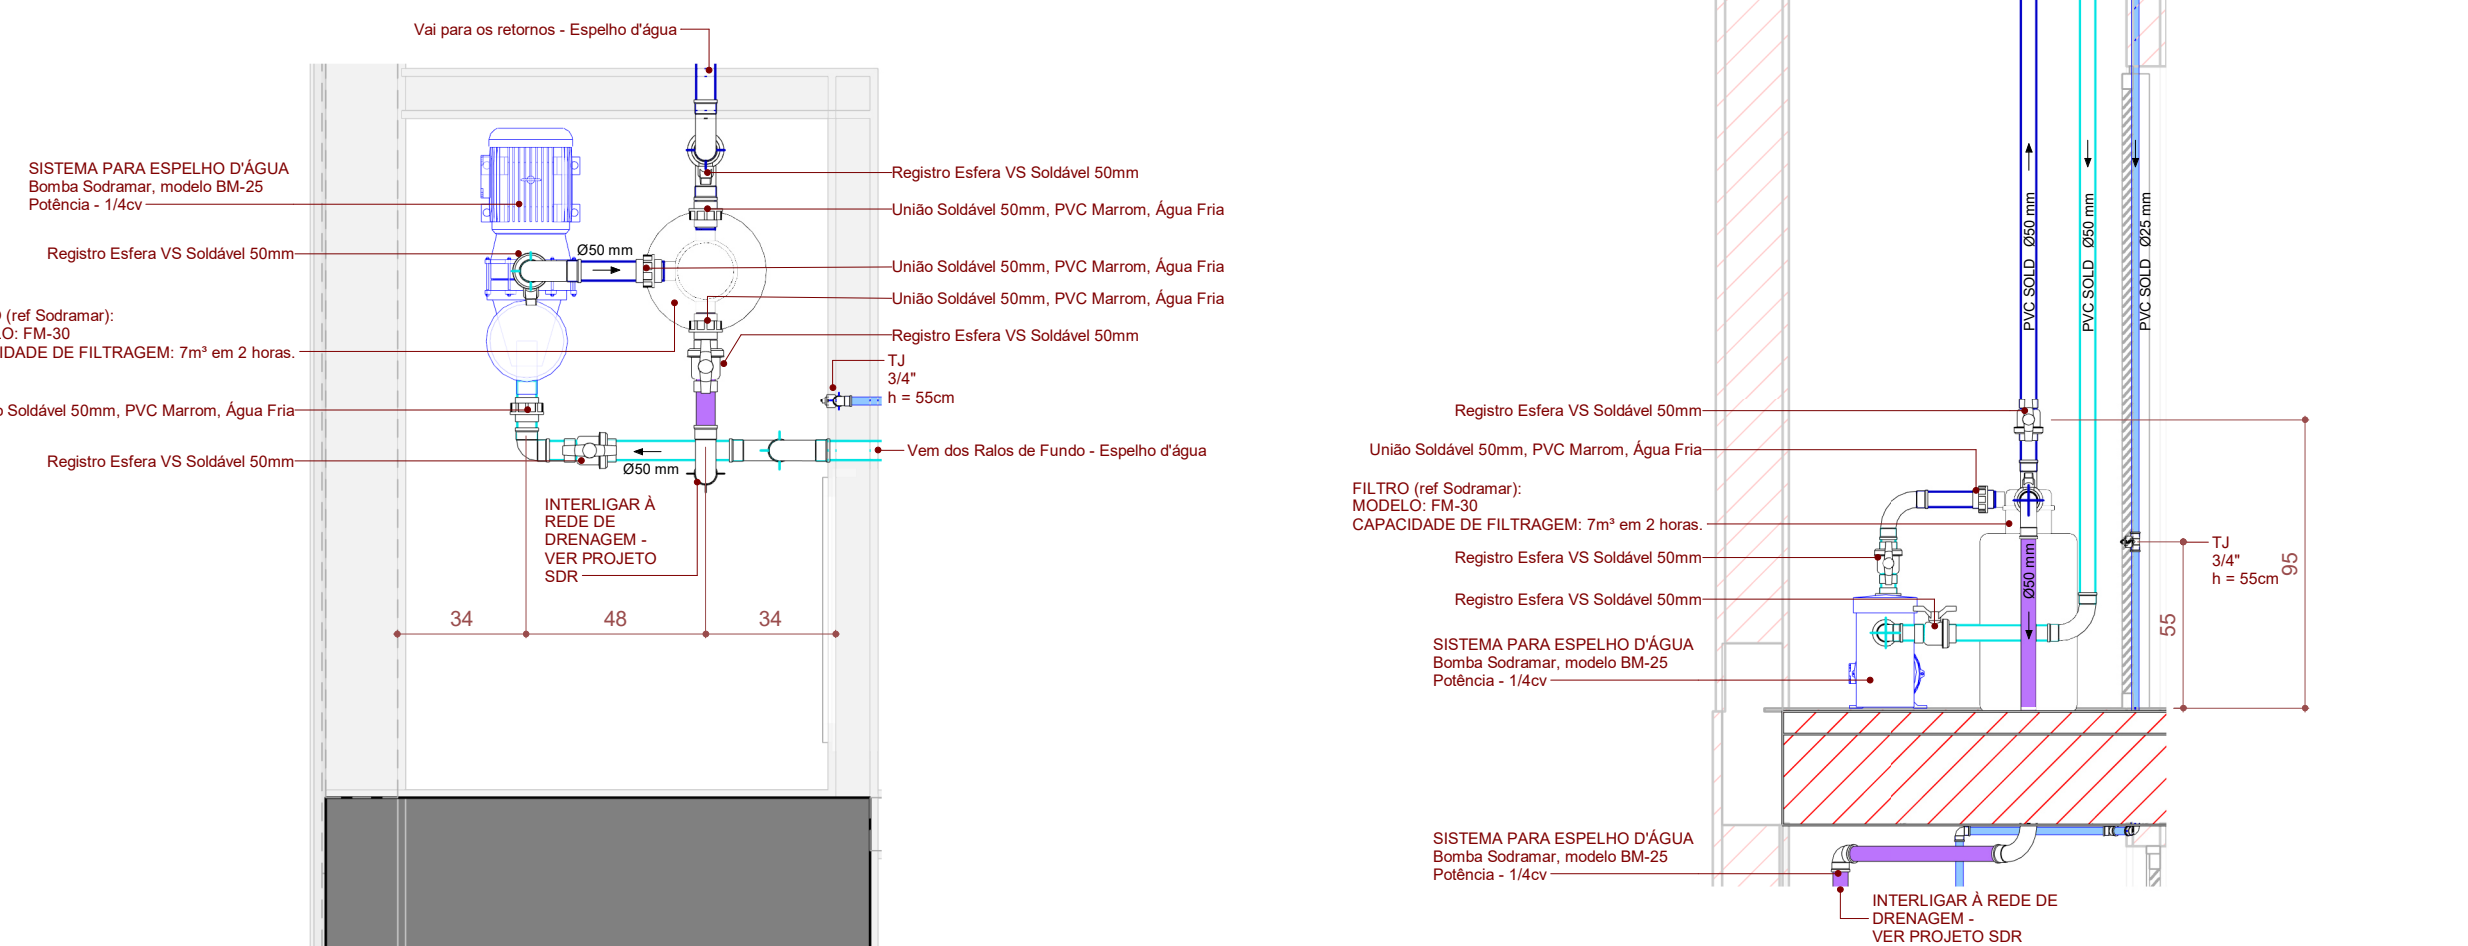

**PLANTA BAIXA - CASA DE MÁQUINAS ESPELHO D'ÁGUA - G3**  
**ESCALA 1:20**

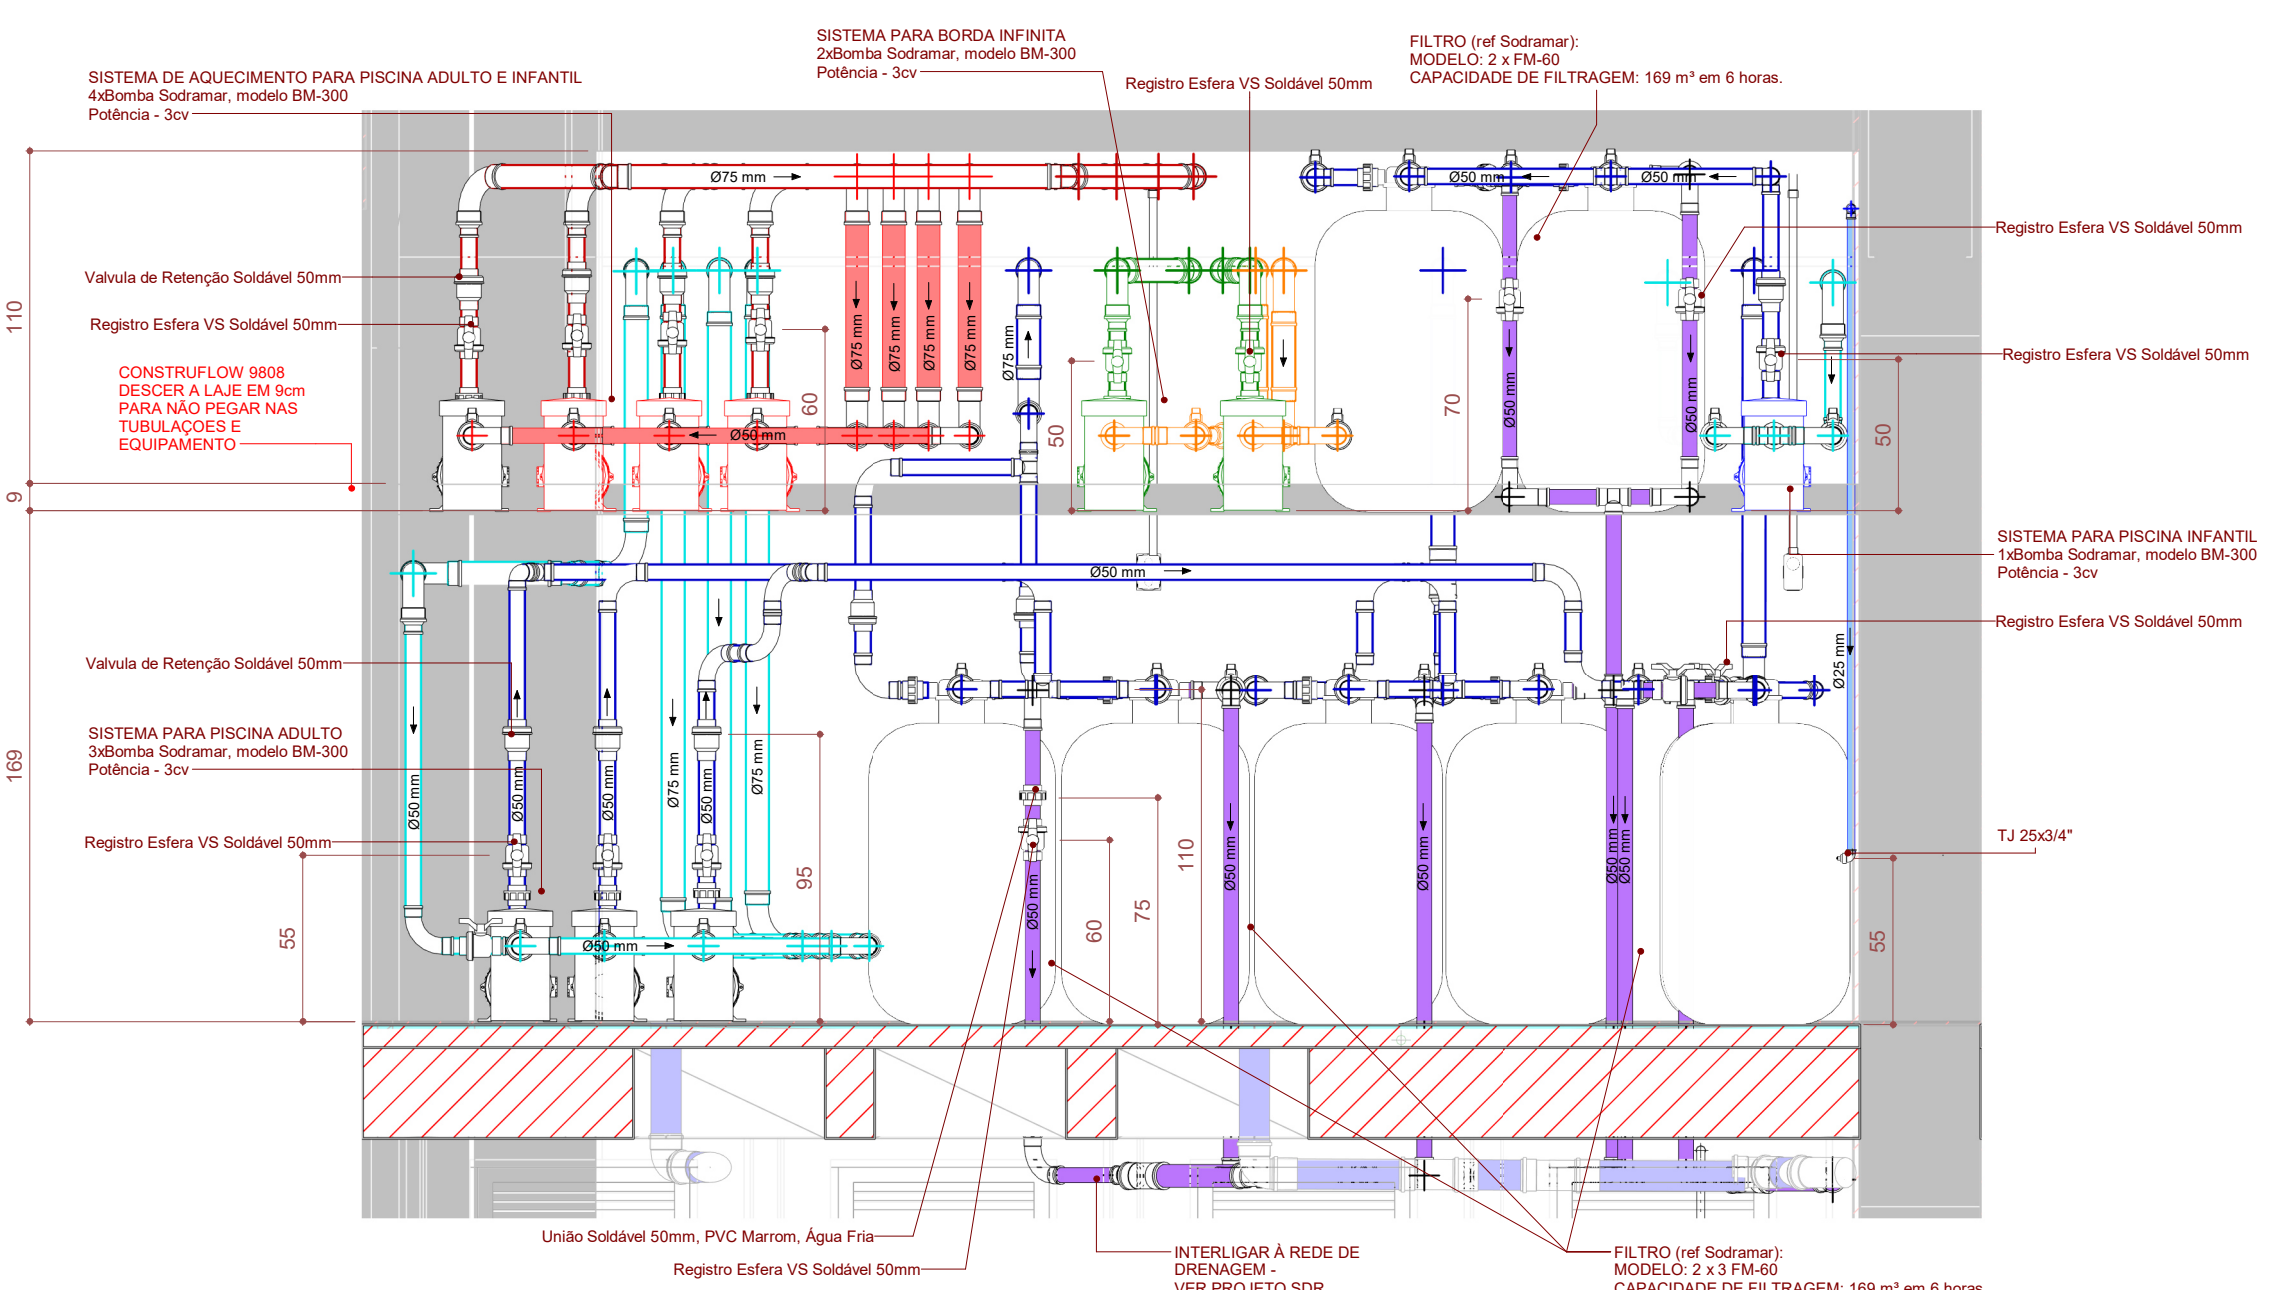

**CORTE - CASA DE MÁQUINAS**  
ESCALA 1:25

| LEGENDA |                                                                 |  |                                                                |
|---------|-----------------------------------------------------------------|--|----------------------------------------------------------------|
|         | TUBO DE SUÇÃO AF DA PISCINA<br>PVC - DIÂMETRO INDICADO          |  | TUBO DE RETORNO ÁGUA QUENTE PISCINA<br>PVC - DIÂMETRO INDICADO |
|         | TUBO DE RETORNO ÁGUA FRIA DA PISCINA<br>PVC - DIÂMETRO INDICADO |  | TUBO DE SUÇÃO AF BORDA INFINITA<br>PVC - DIÂMETRO INDICADO     |
|         | TUBO DE RETORNO AF DA BORDA INFINITA<br>PVC - DIÂMETRO INDICADO |  | TUBO DE SUÇÃO ÁGUA QUENTE<br>PVC - DIÂMETRO INDICADO           |
|         | TUBO DE LIMPEZA E EXTRAVASADO<br>MATERIAL E DIÂMETRO INDICADOS  |  |                                                                |

|                 |  |  |  |  |  |  |
|-----------------|--|--|--|--|--|--|
| CX. D'ÁGUA      |  |  |  |  |  |  |
| TELHADO         |  |  |  |  |  |  |
| APTO COBERTURA  |  |  |  |  |  |  |
| PAVTO TIPO 3800 |  |  |  |  |  |  |
| PAVTO TIPO      |  |  |  |  |  |  |
| PAVTO TIPO      |  |  |  |  |  |  |
| PAVTO TIPO      |  |  |  |  |  |  |
| PAVTO TIPO      |  |  |  |  |  |  |
| PAVTO TIPO      |  |  |  |  |  |  |
| PAVTO TIPO      |  |  |  |  |  |  |
| PAVTO TIPO      |  |  |  |  |  |  |
| PAVTO TIPO      |  |  |  |  |  |  |
| PAVTO TIPO      |  |  |  |  |  |  |
| PAVTO TIPO      |  |  |  |  |  |  |
| PAVTO TIPO      |  |  |  |  |  |  |
| PAVTO TIPO      |  |  |  |  |  |  |
| PAVTO TIPO      |  |  |  |  |  |  |
| PAVTO TIPO      |  |  |  |  |  |  |
| PAVTO TIPO      |  |  |  |  |  |  |
| PAVTO TIPO      |  |  |  |  |  |  |
| PAVTO TIPO      |  |  |  |  |  |  |
| PAVTO TIPO      |  |  |  |  |  |  |
| PAVTO TIPO      |  |  |  |  |  |  |
| PAVTO TIPO      |  |  |  |  |  |  |
| PAVTO TIPO      |  |  |  |  |  |  |
| PAVTO TIPO      |  |  |  |  |  |  |
| PAVTO TIPO      |  |  |  |  |  |  |
| LAZER           |  |  |  |  |  |  |
| GARAGEM 03      |  |  |  |  |  |  |
| GARAGEM 02      |  |  |  |  |  |  |
| GARAGEM 01      |  |  |  |  |  |  |
| TÉRREÇO         |  |  |  |  |  |  |

| ESQUEMA DE PAVIMENTOS    |                 |             |
|--------------------------|-----------------|-------------|
| ARQUIVO BASE             | NOME DO ARQUIVO | RECEBIDO EM |
| PROJETO ARQUITETÔNICO    | BOC-EXE-ARQ-LAZ | 24-02-2023  |
| PROJETO ESTRUTURAL - IFC | BOC-EST-PRE-MOD | 07-03-2023  |
| PROJETO ESTRUTURAL - DWG |                 |             |

|                     |                           |             |
|---------------------|---------------------------|-------------|
|                     | RESPONSÁVEL PELA RESPOSTA | RECEBIDO EM |
| LISTA DE DEFINIÇÕES |                           |             |
| FUROS APROVADOS     |                           |             |

|         |            |                                         |             |
|---------|------------|-----------------------------------------|-------------|
|         |            |                                         |             |
|         |            |                                         |             |
| R01     | 27-04-2023 | AJUSTE CONFORME RELATÓRIO E CONSTRUFLOW | PEDRO       |
| R00     | 03-03-2023 | EXECUTIVO - EMISSÃO INICIAL             | PEDRO       |
| REVISÃO | DATA       | DESCRIÇÃO                               | RESPONSÁVEL |

**thórus**  
engenharia

**AMANDA LARENTIS**  
ENSG. CIVIL - CREA RJ 128.062-4

**RAUL PEDRO ESKELESSEN**  
ENSG. ELÉTRICISTA - CREA/SC 145.953-2

**RAFAEL ANTON**  
ENSG. CIVIL - CREA RJ 160.962-4

**EQUIPE TÉCNICA:**

RUA DR. JOÃO COLIN, 1.872, SL. 32  
BARRIO AMÉRICA | JORNALW-SC  
FONE: (47) 3041.0643

AV. DO ESTADO MALDI VIEIRA, 1600, SL. 32  
BARRIO ARRIBA | BALNEÁRIO CAMBORIÚ-SC  
FONE: (47) 3948.8227

THORUSENGENHARIA.COM.BR  
PROJETOS@THORUSENGENHARIA.COM.BR

|                                       |                                                                     |
|---------------------------------------|---------------------------------------------------------------------|
| <b>PROJETO HIDRÁULICO</b>             |                                                                     |
| OBRA                                  | BRAVA OCEAN                                                         |
| ENDEREÇO                              | RUA CABO - POLÍCIA MILITAR ANTÔNIO RUDOLF, 155, PRAIA BRAVA, ITAJAÍ |
| PROPRIETÁRIO                          | CN CONSTRUTORA E INCORP. LTDA                                       |
| DETALHES - PISCINAS E ESPELHOS D'ÁGUA | <b>HID</b>                                                          |