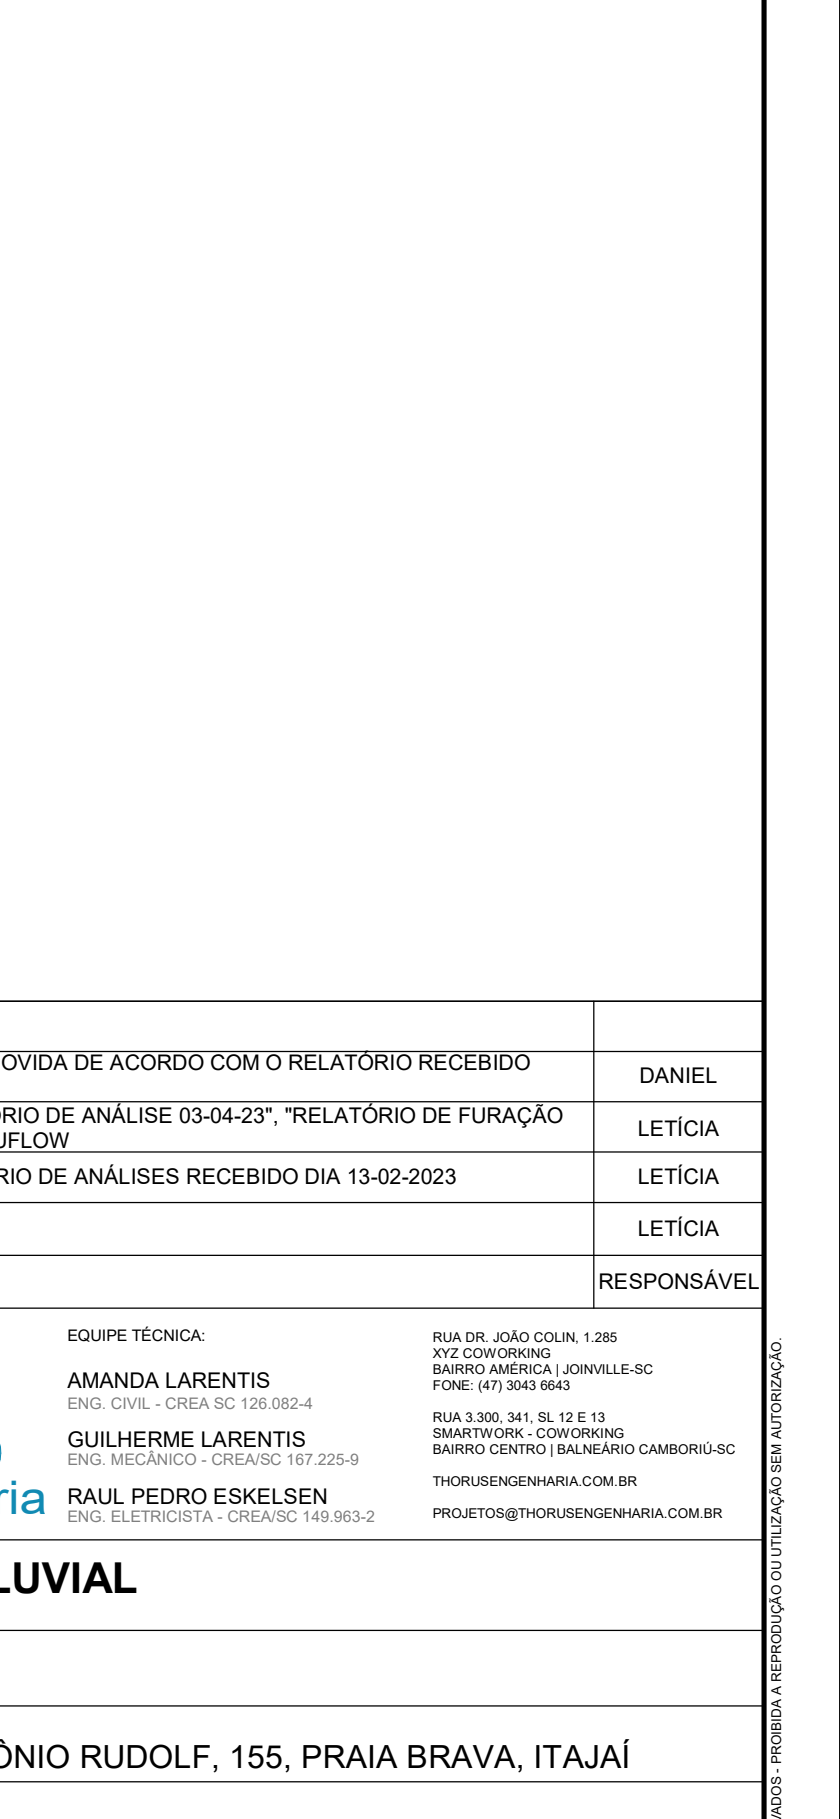
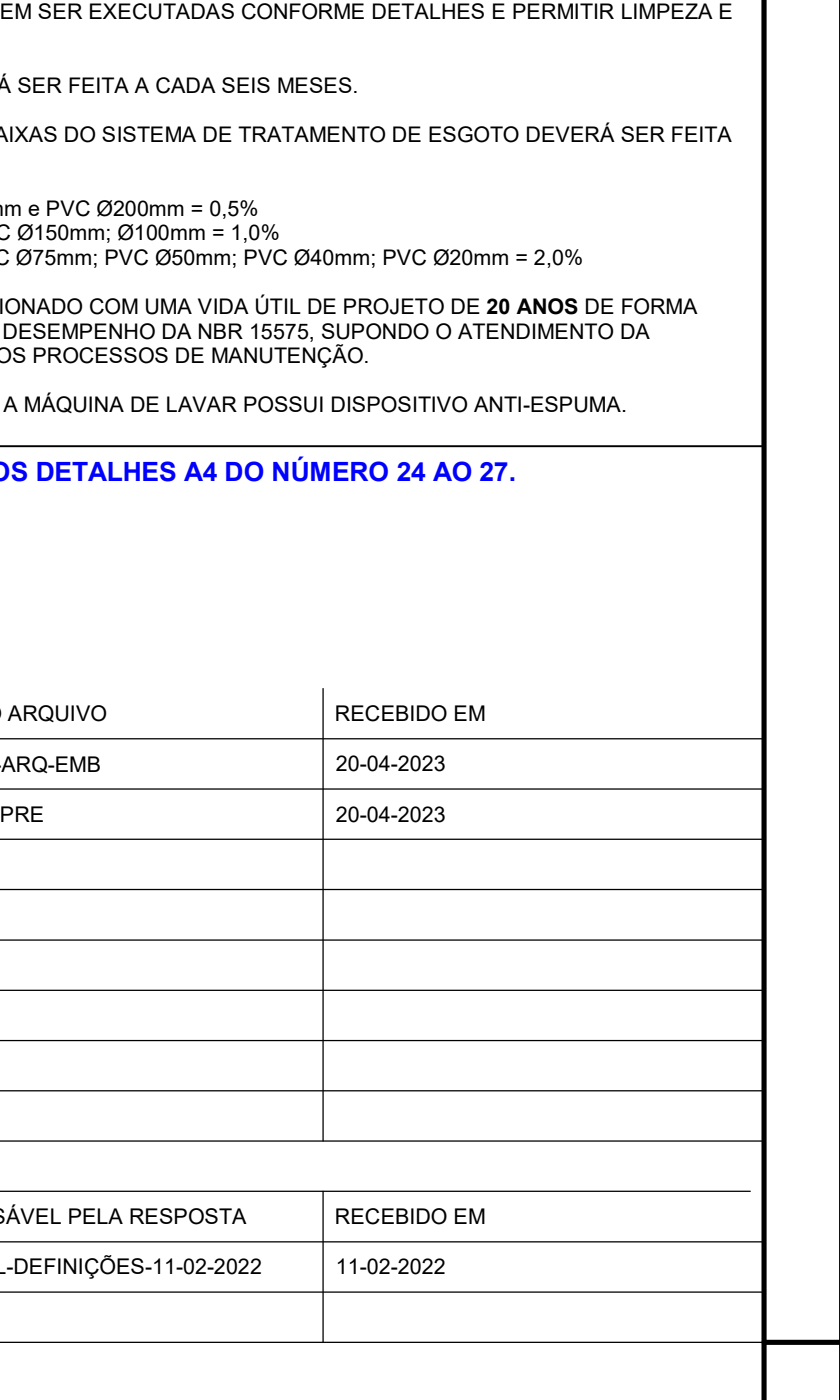
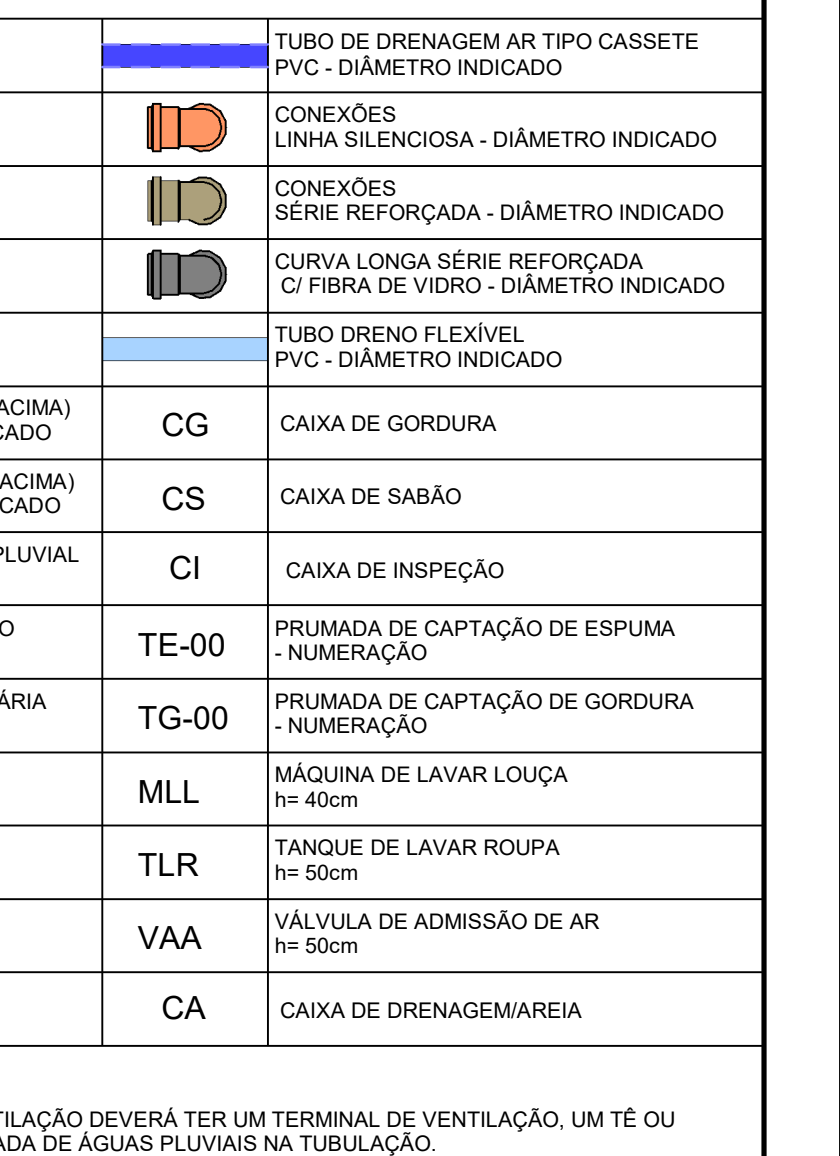
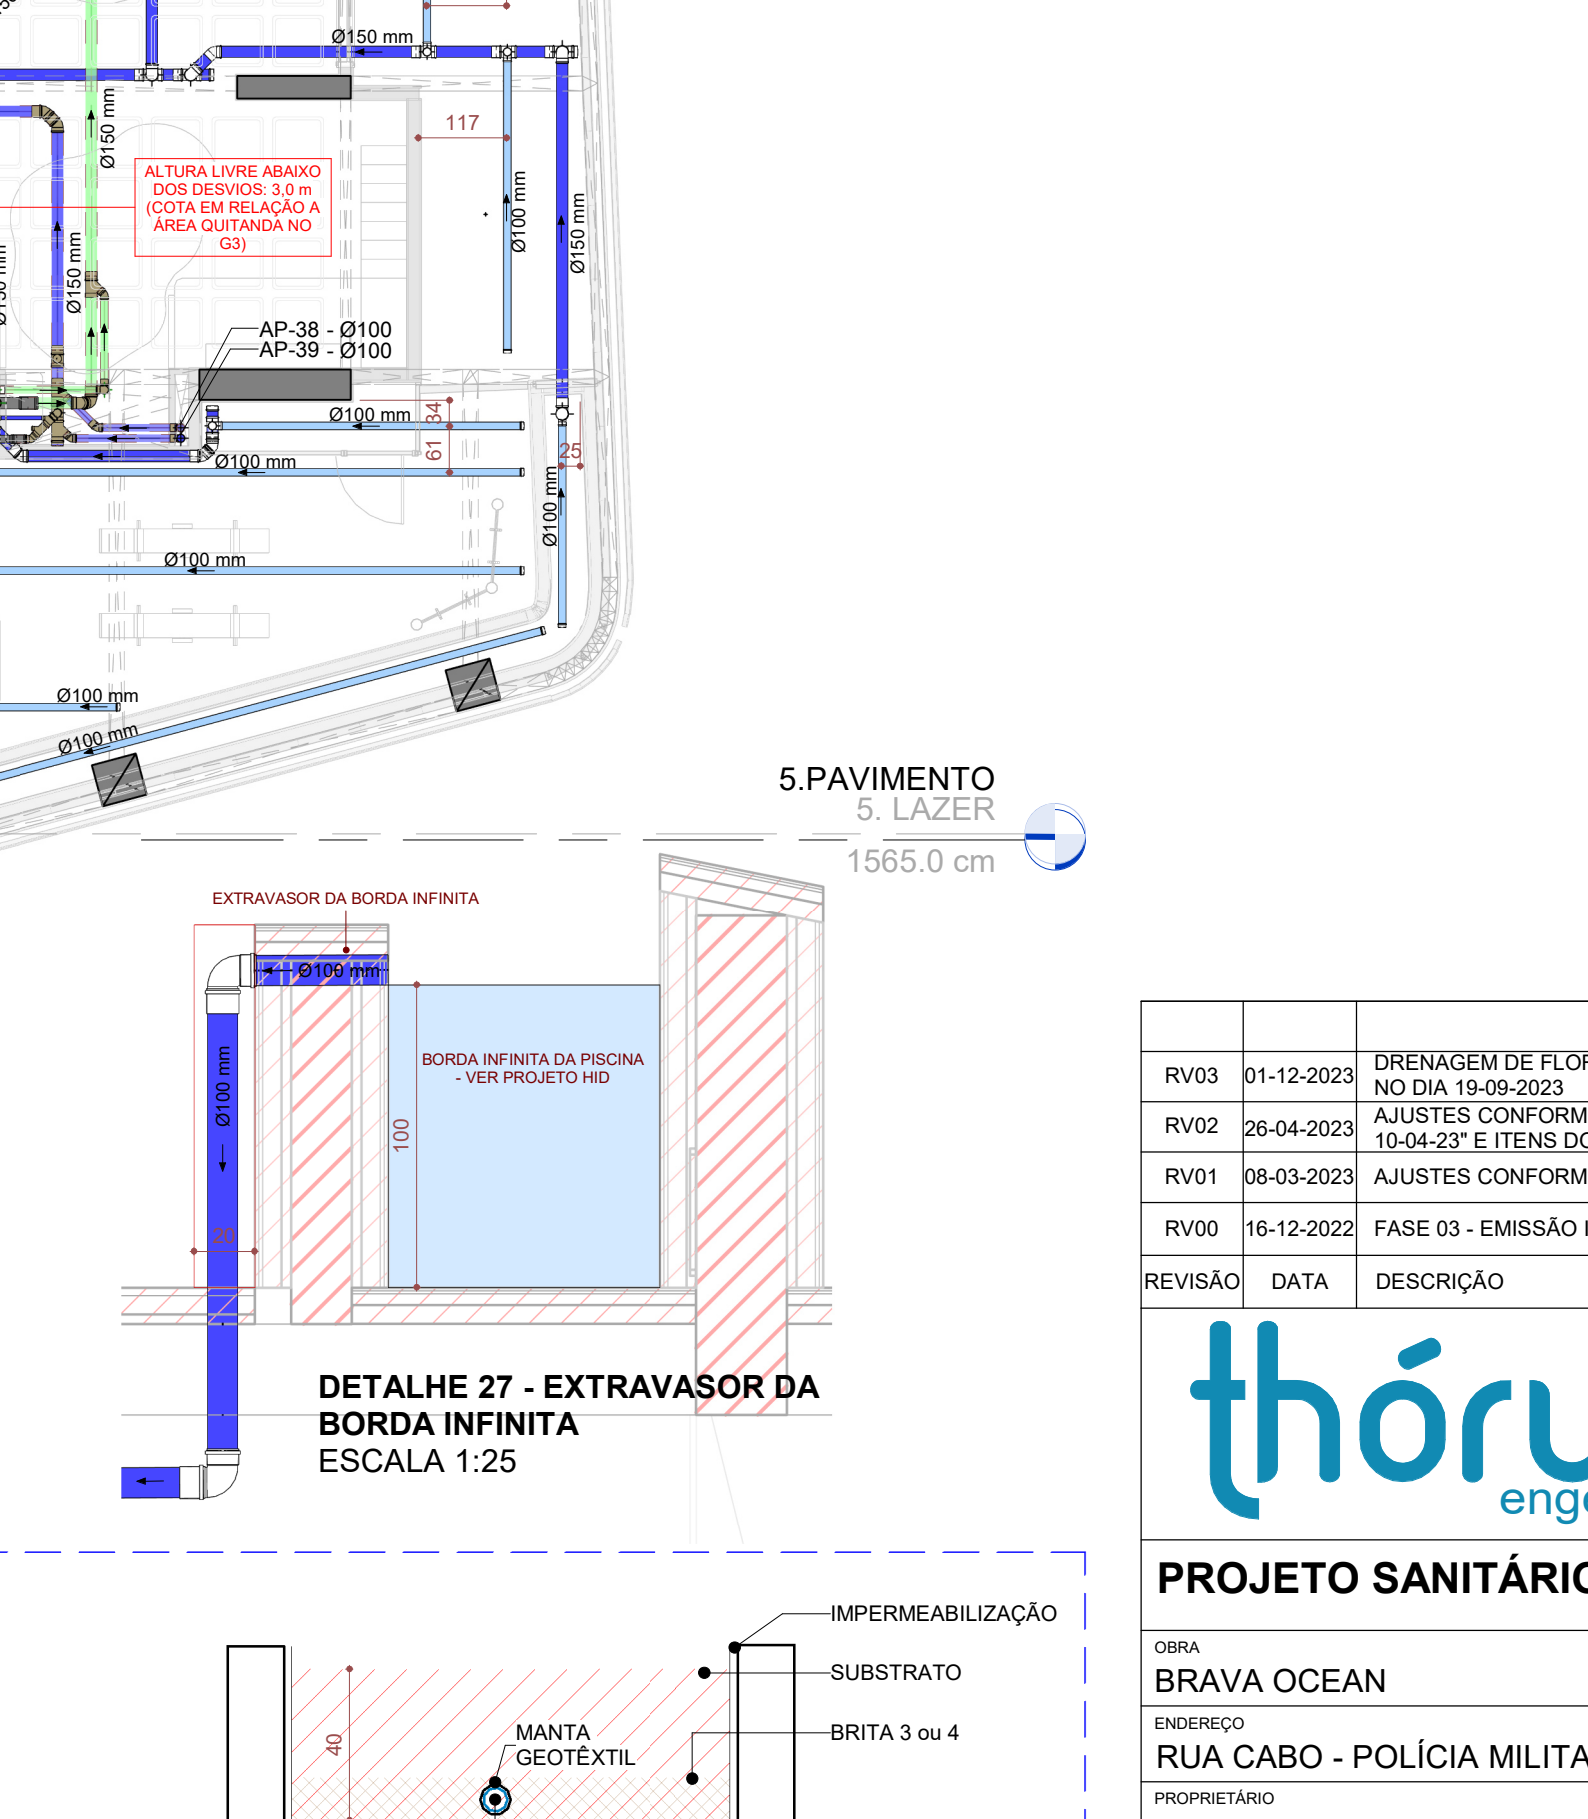
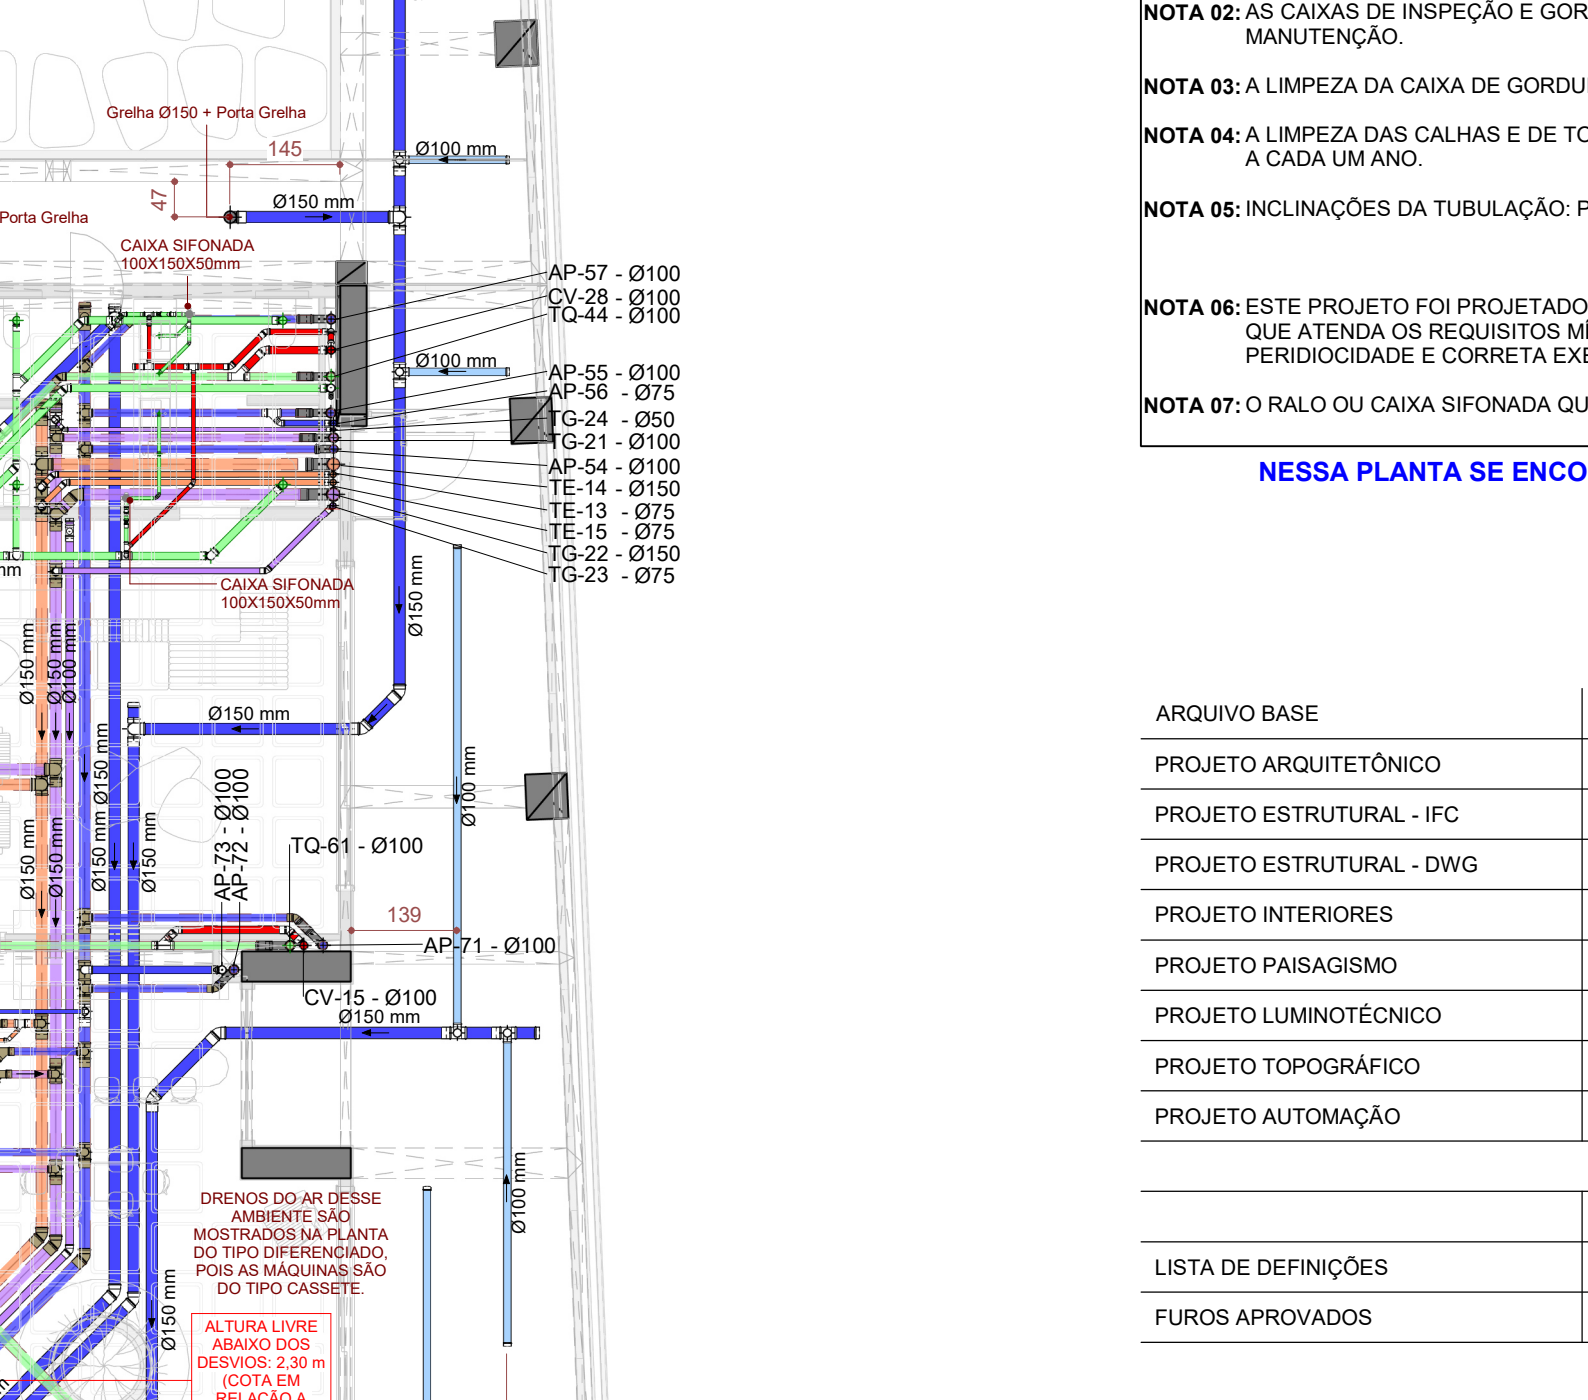
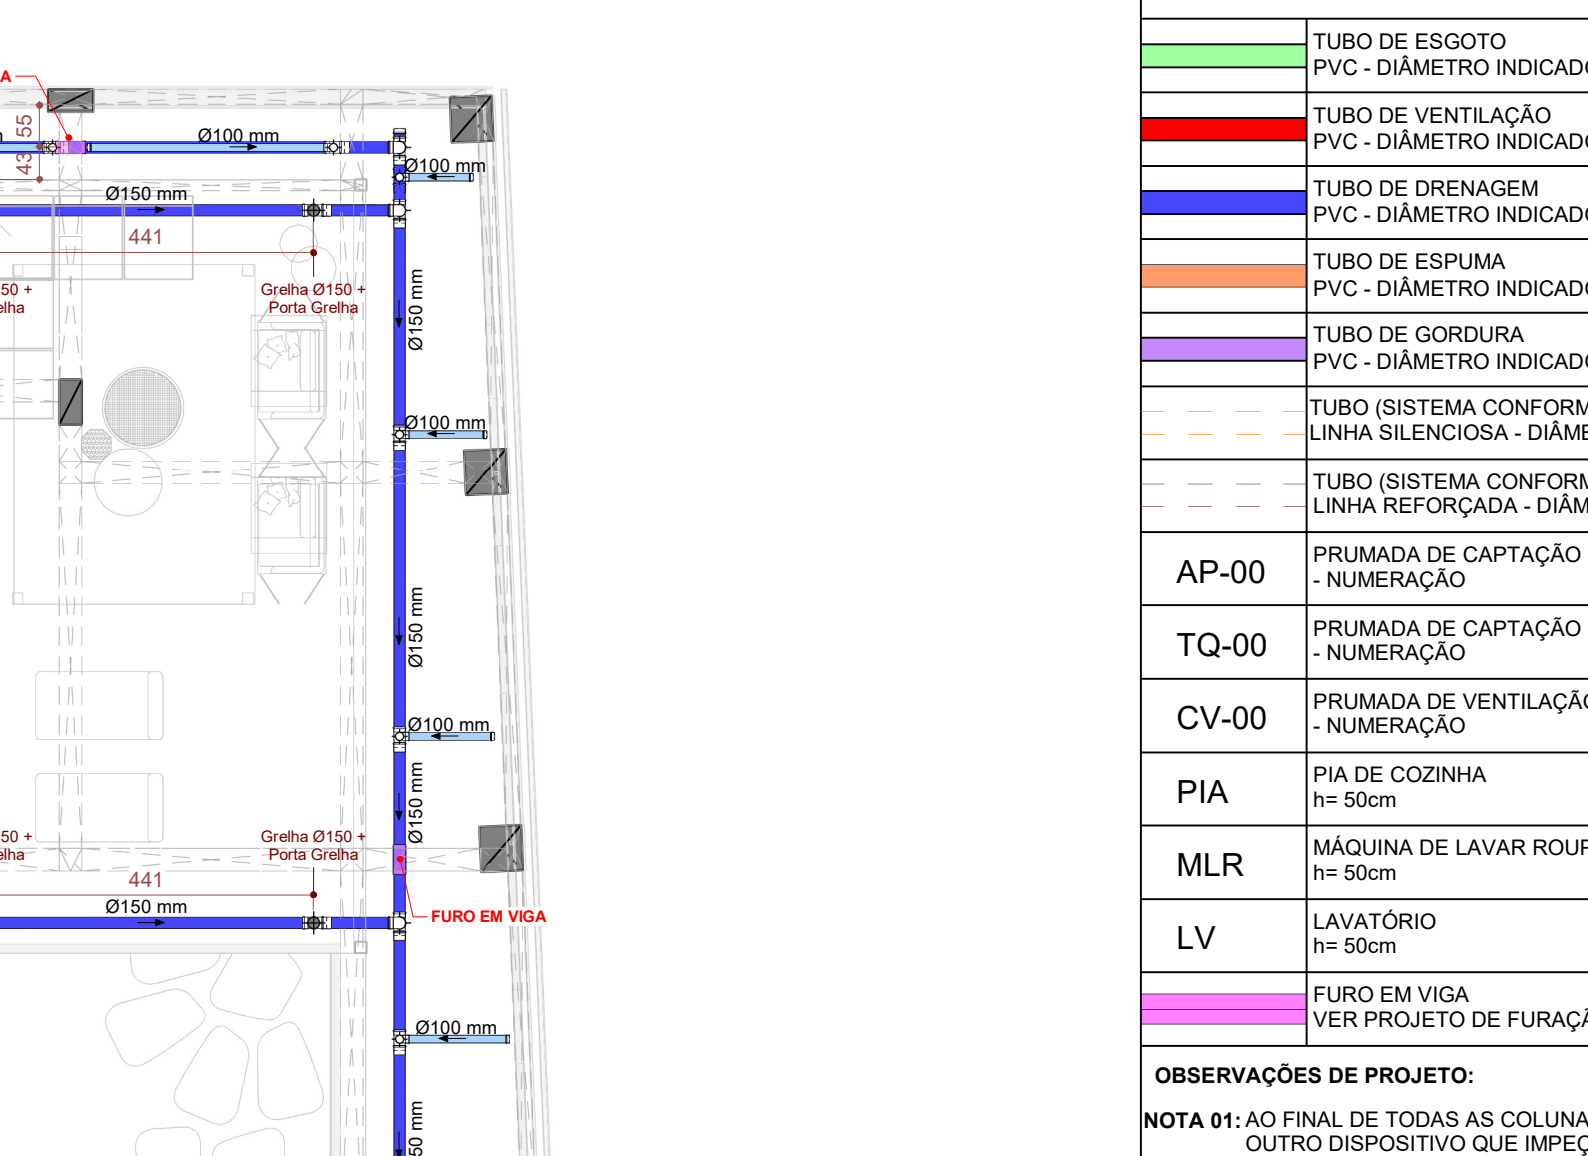
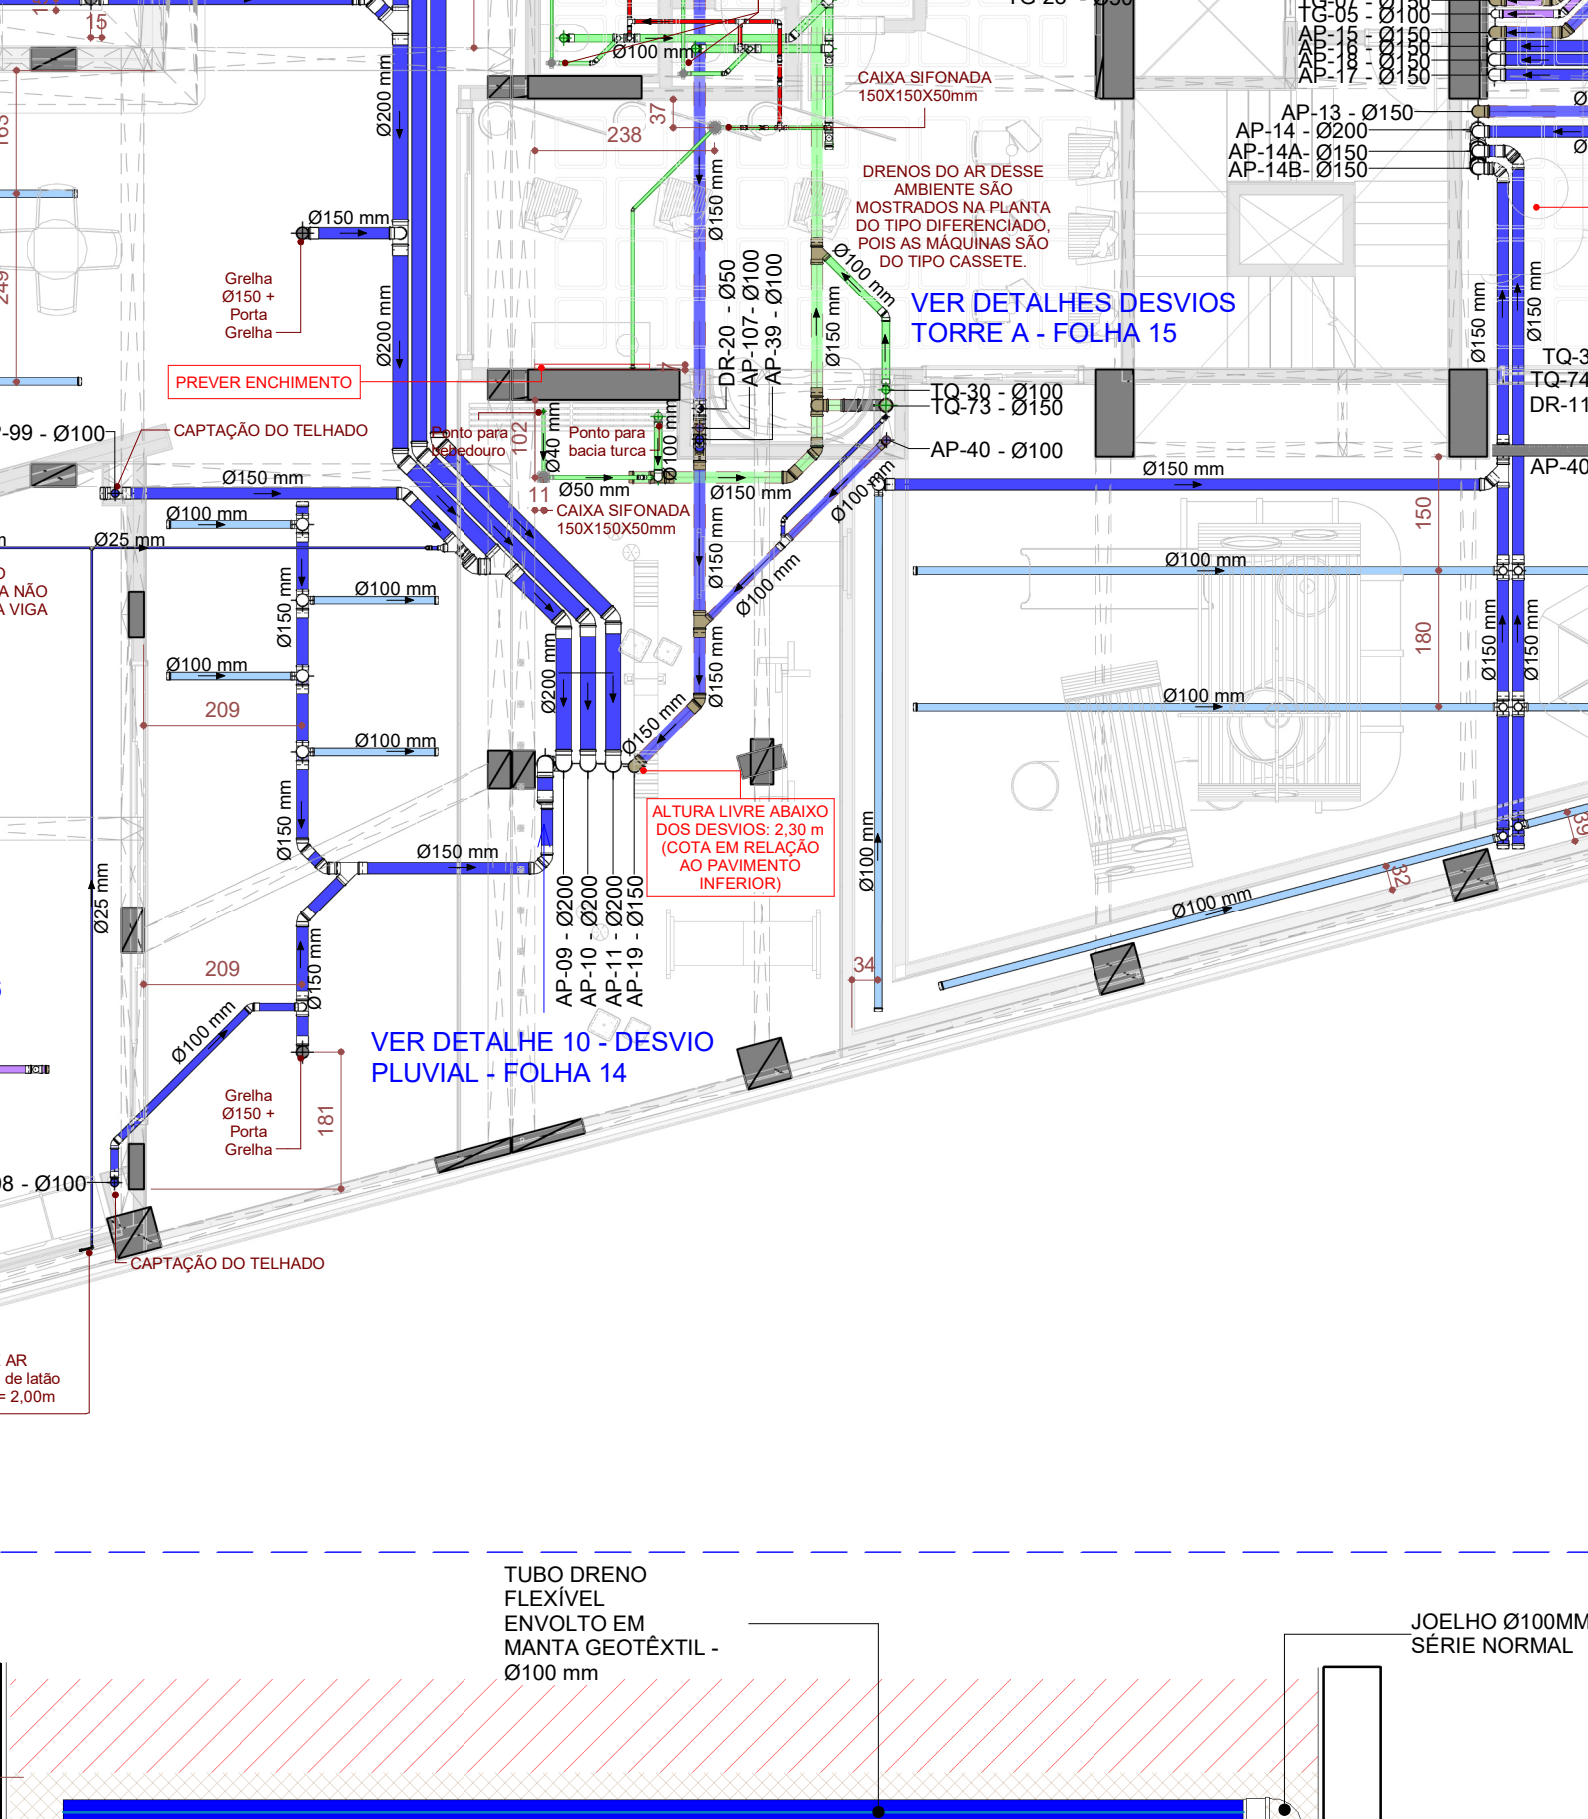
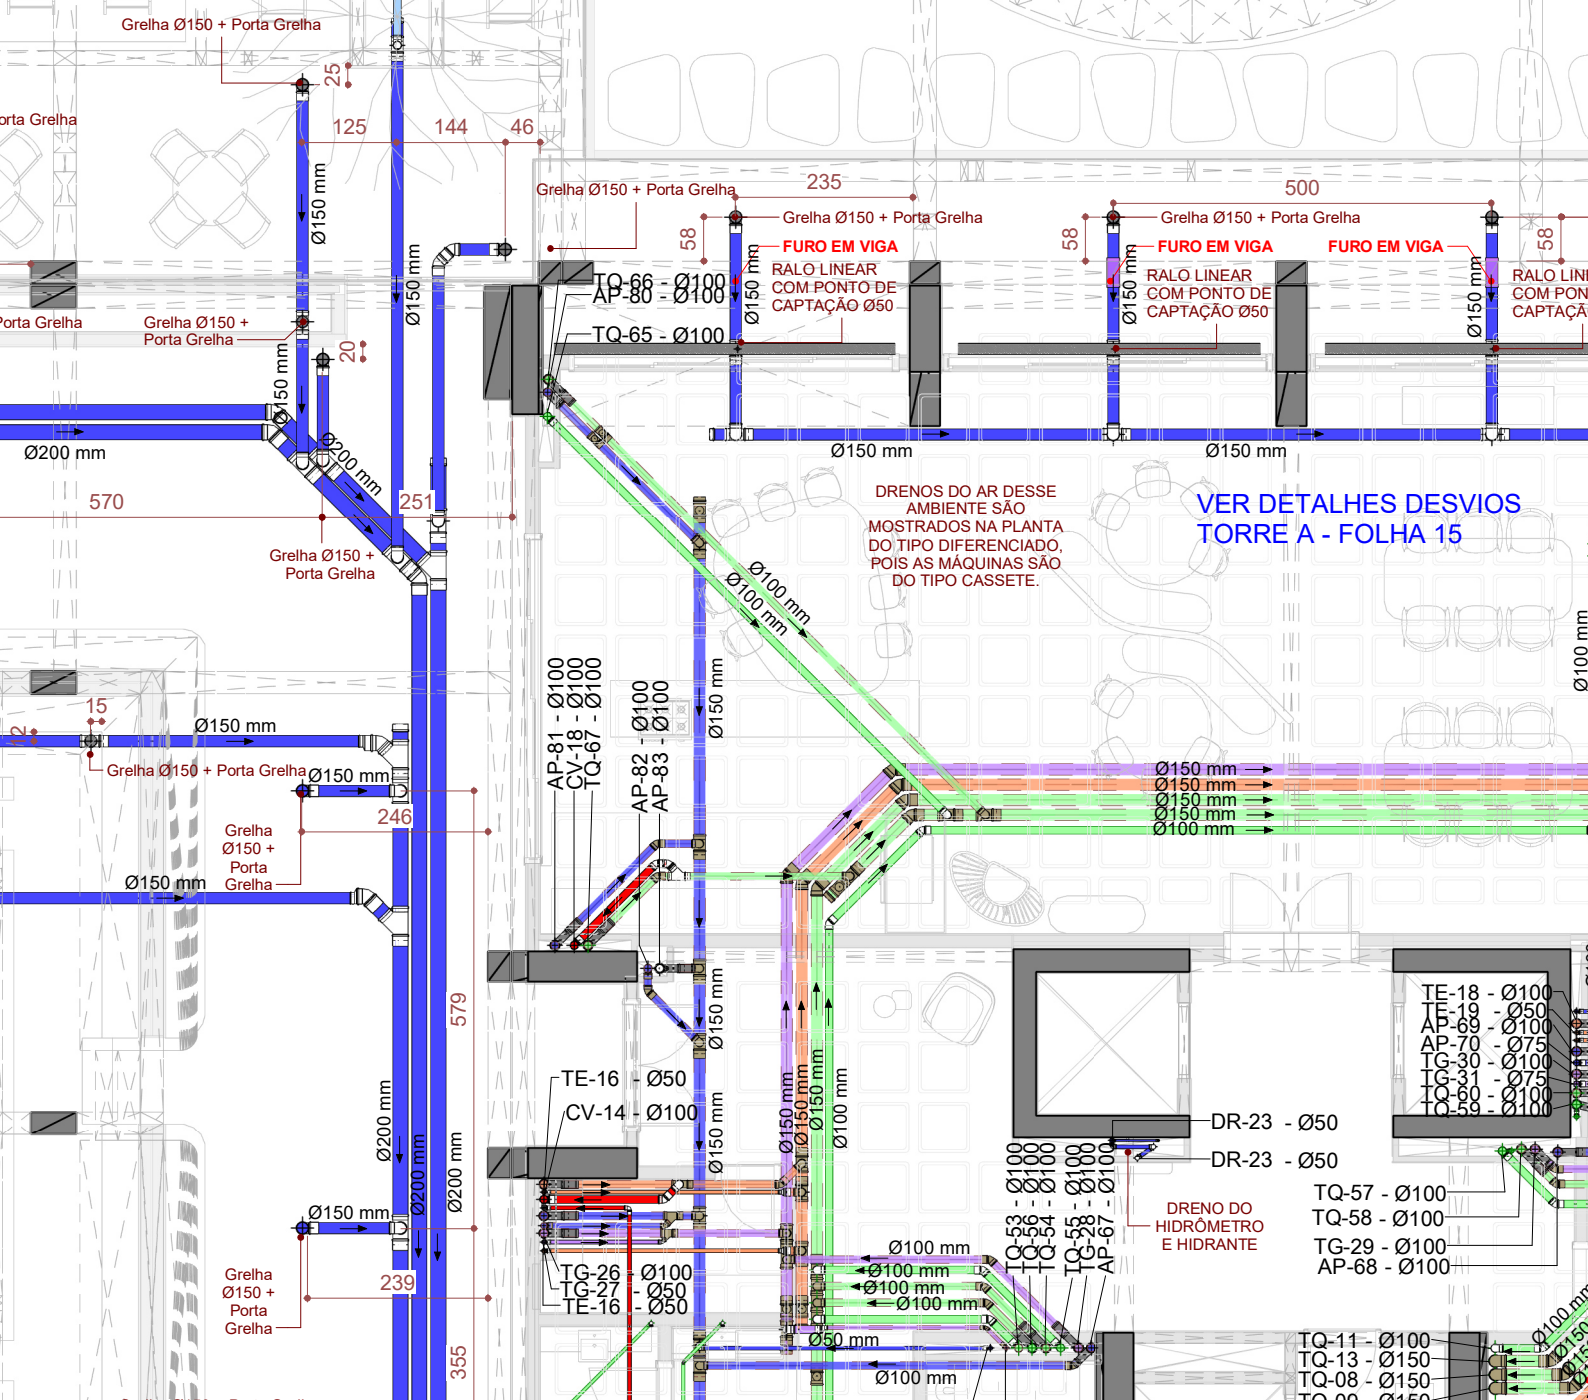
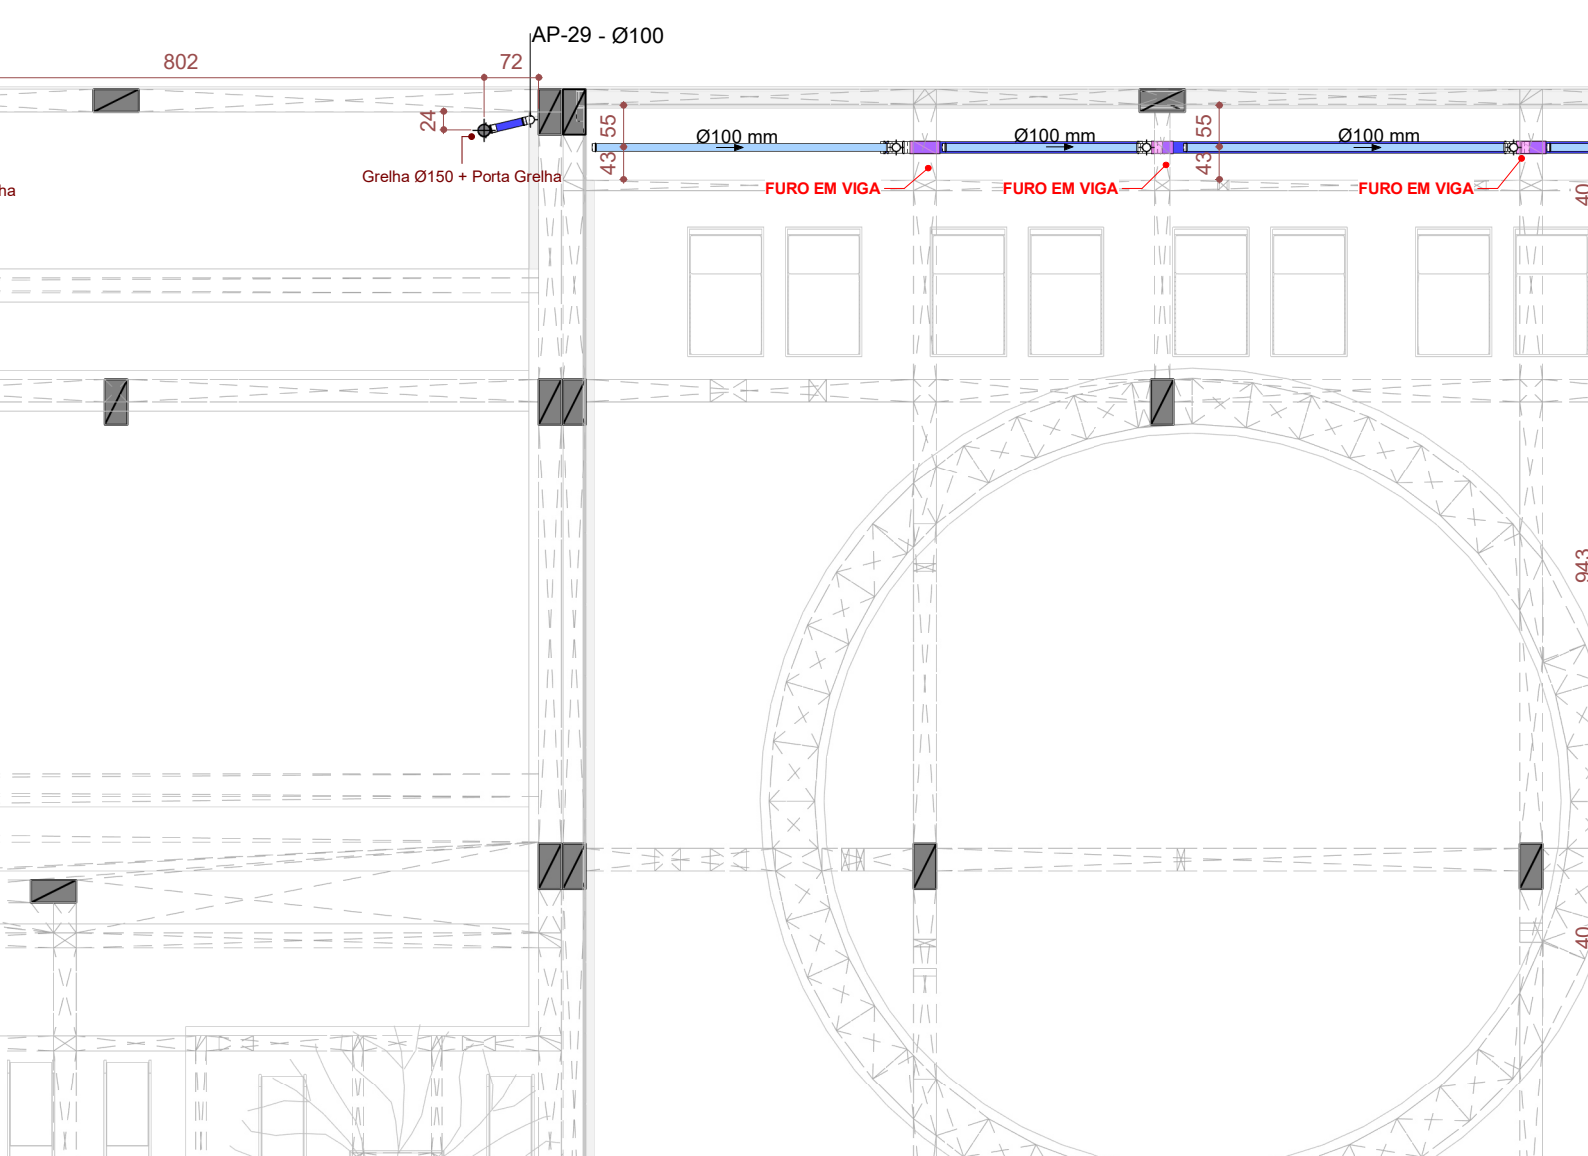
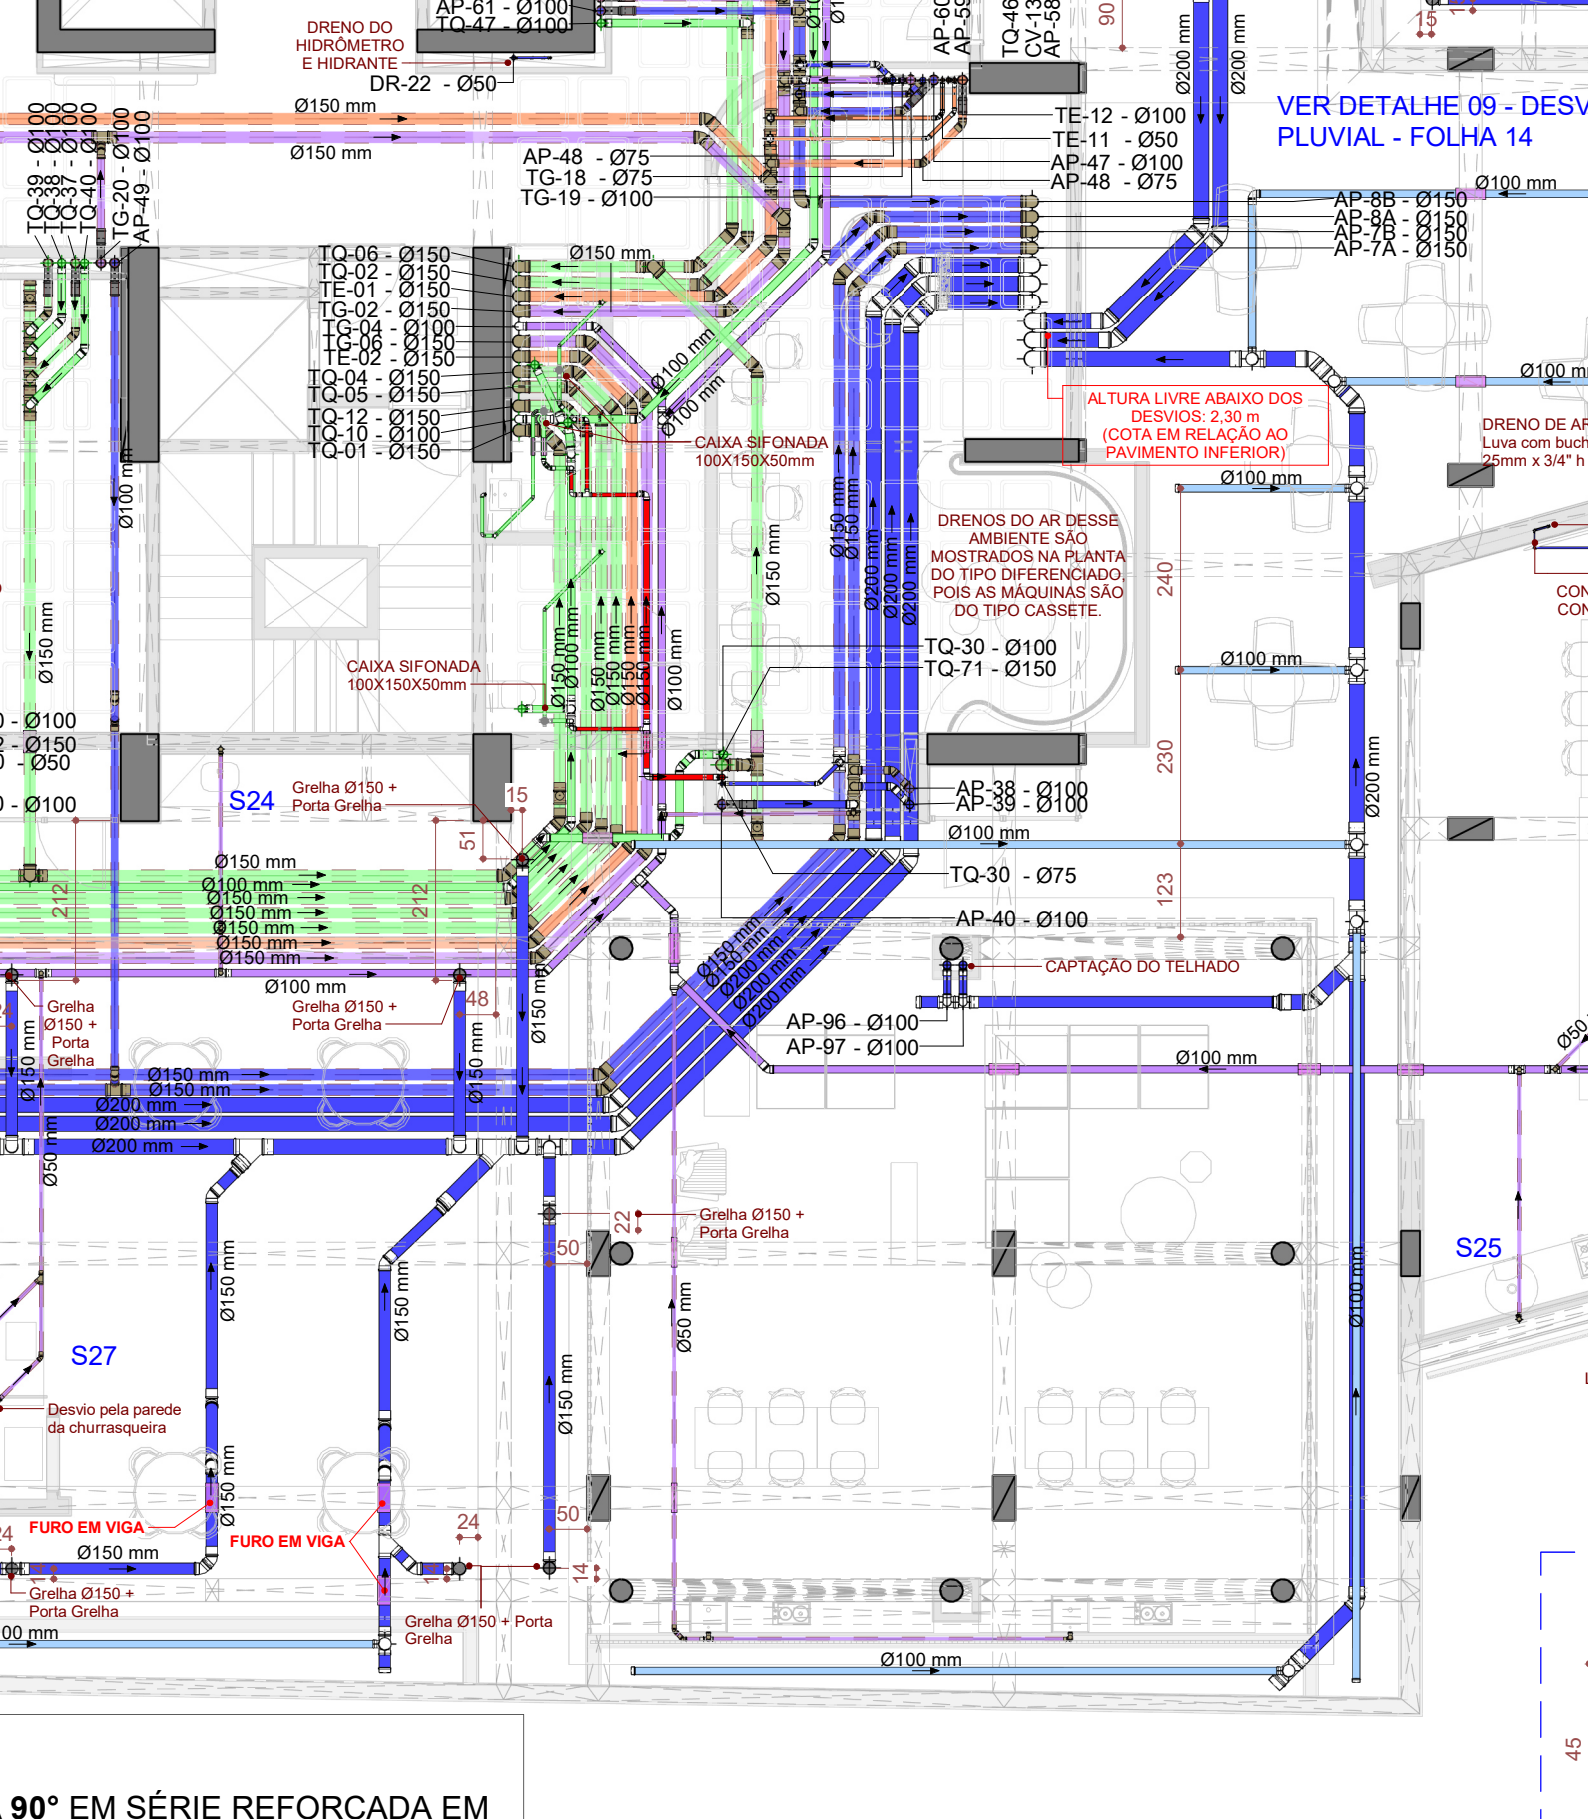
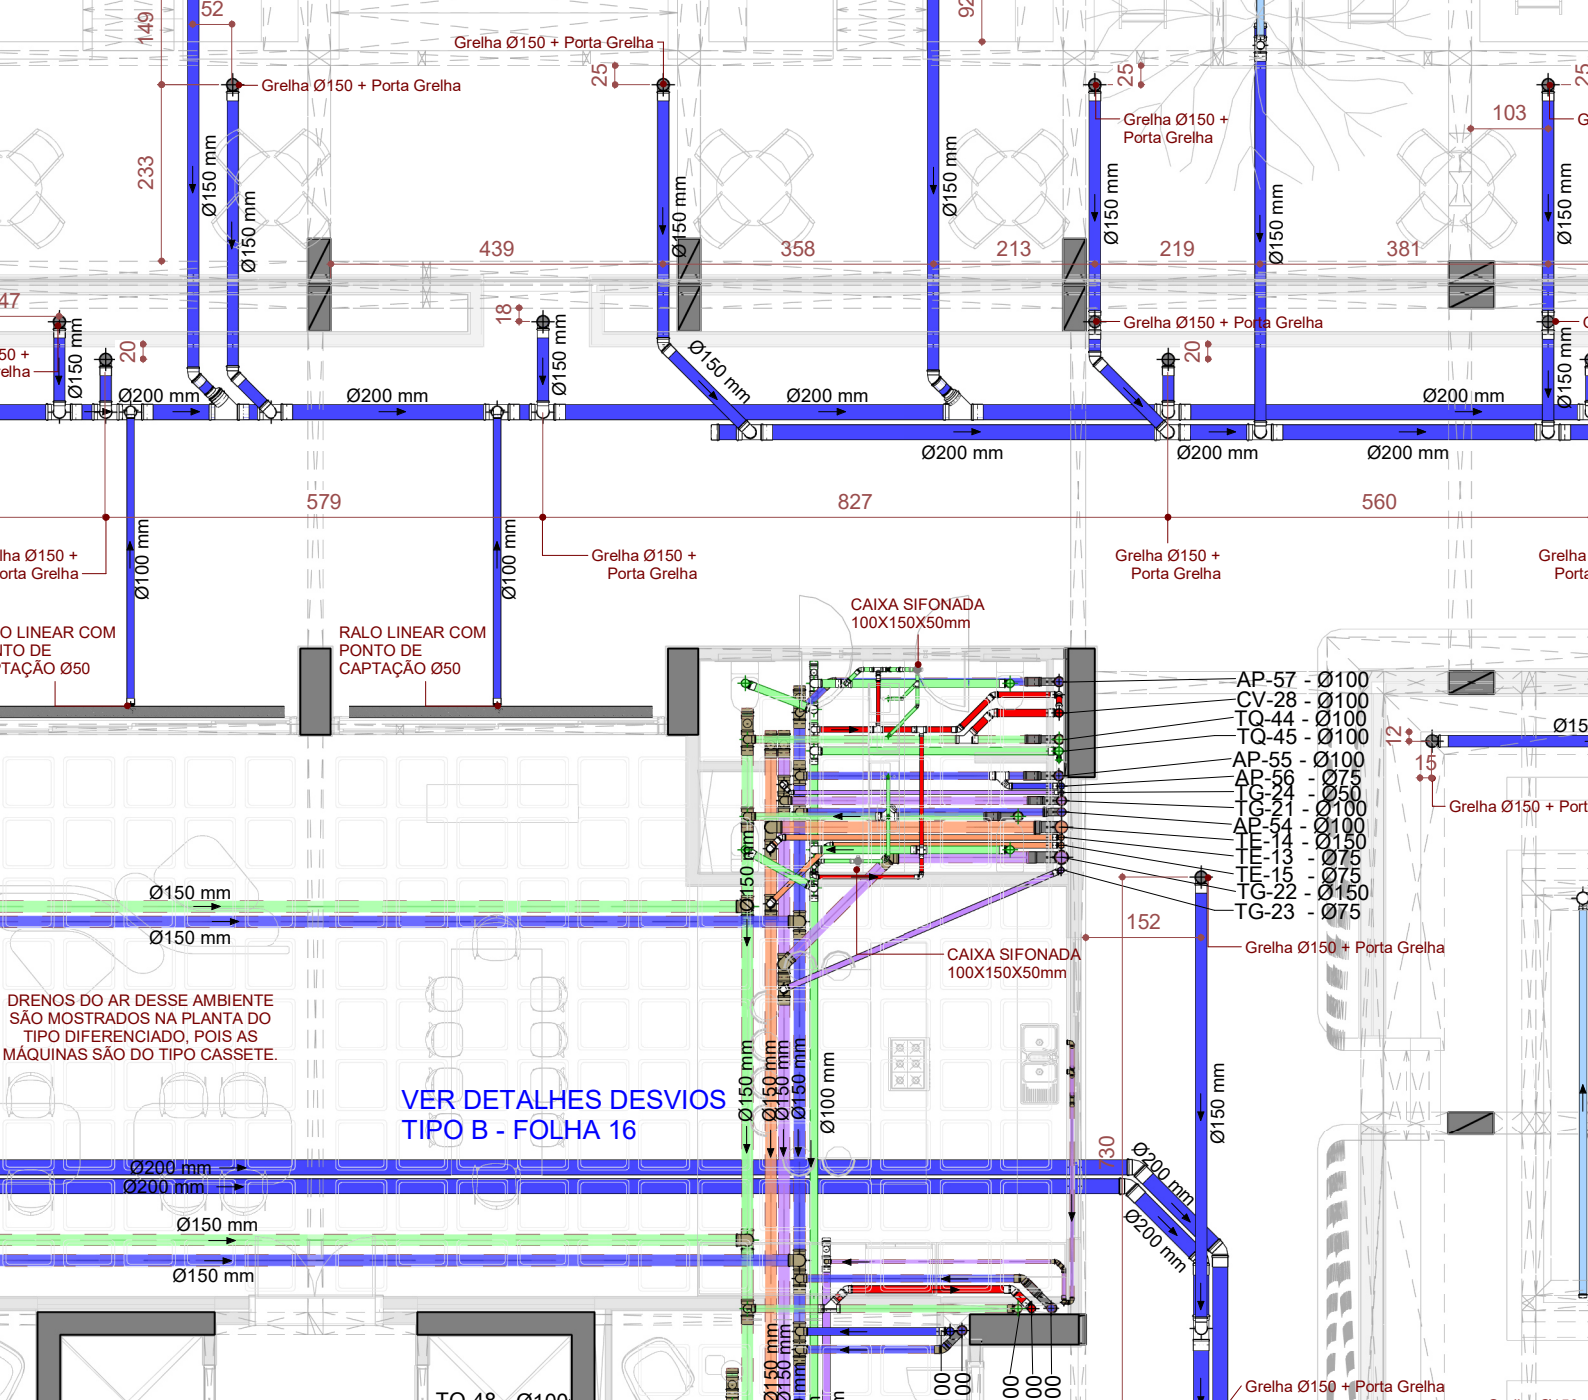
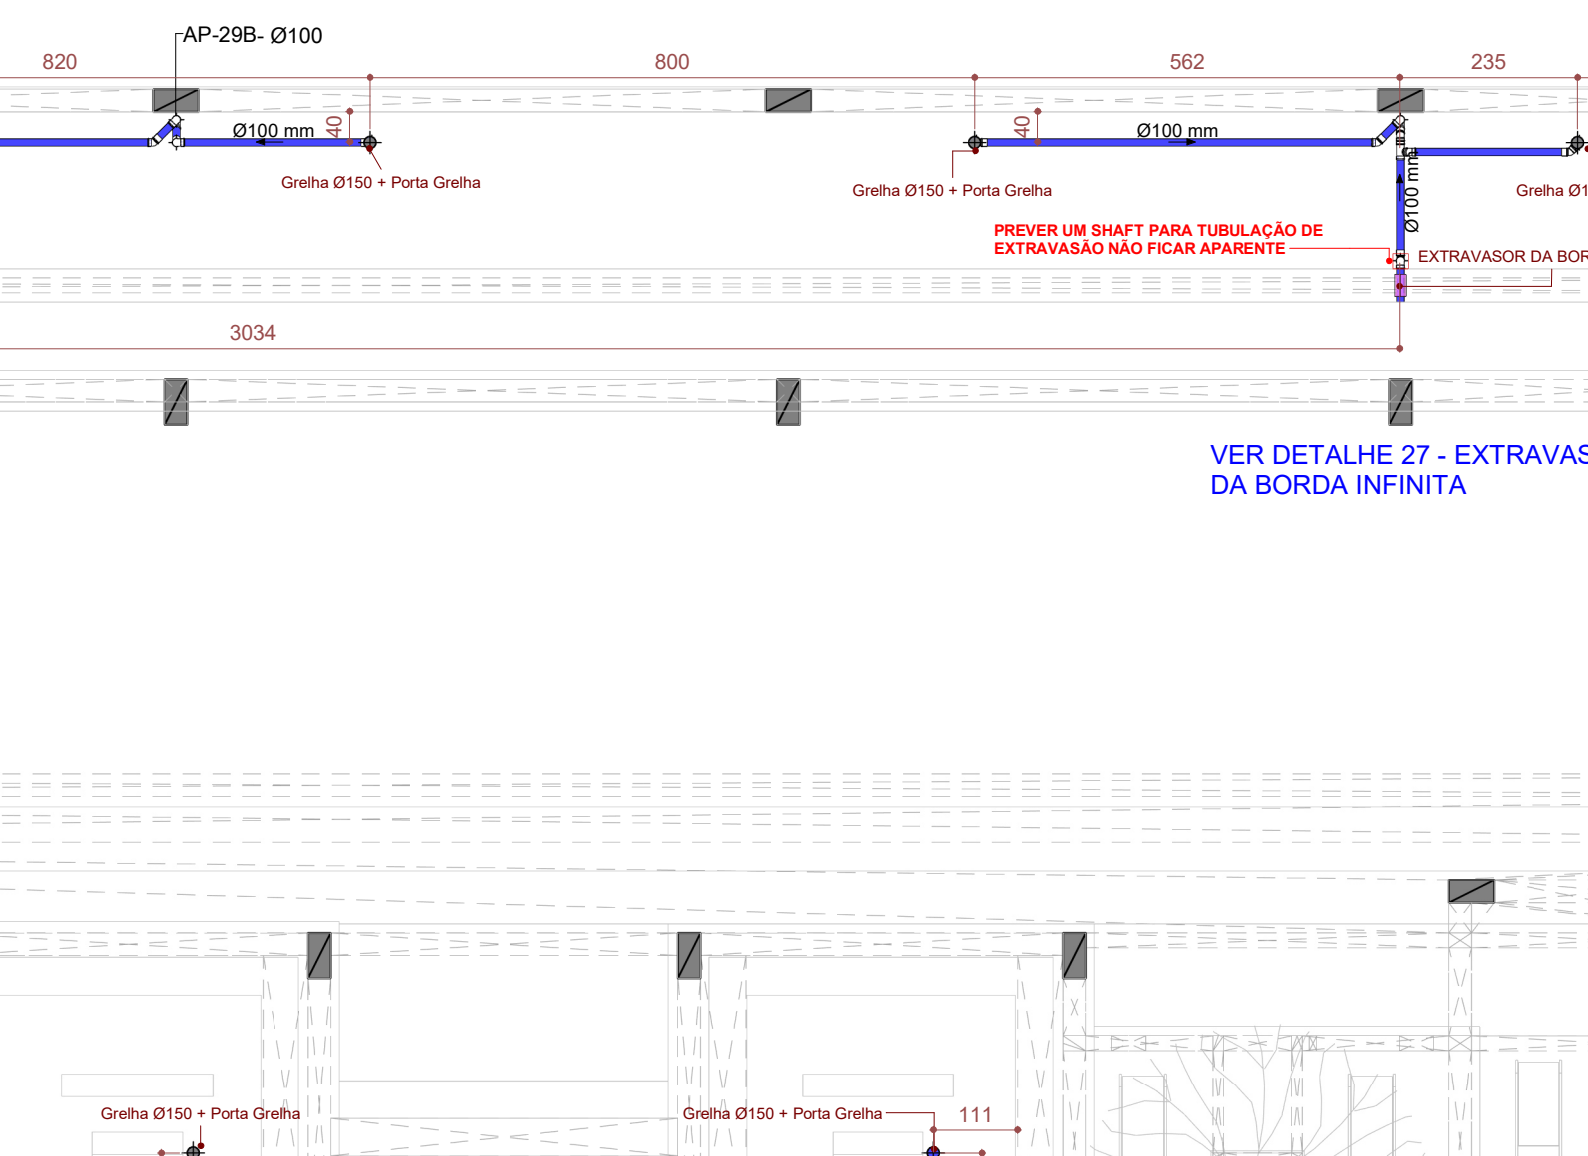
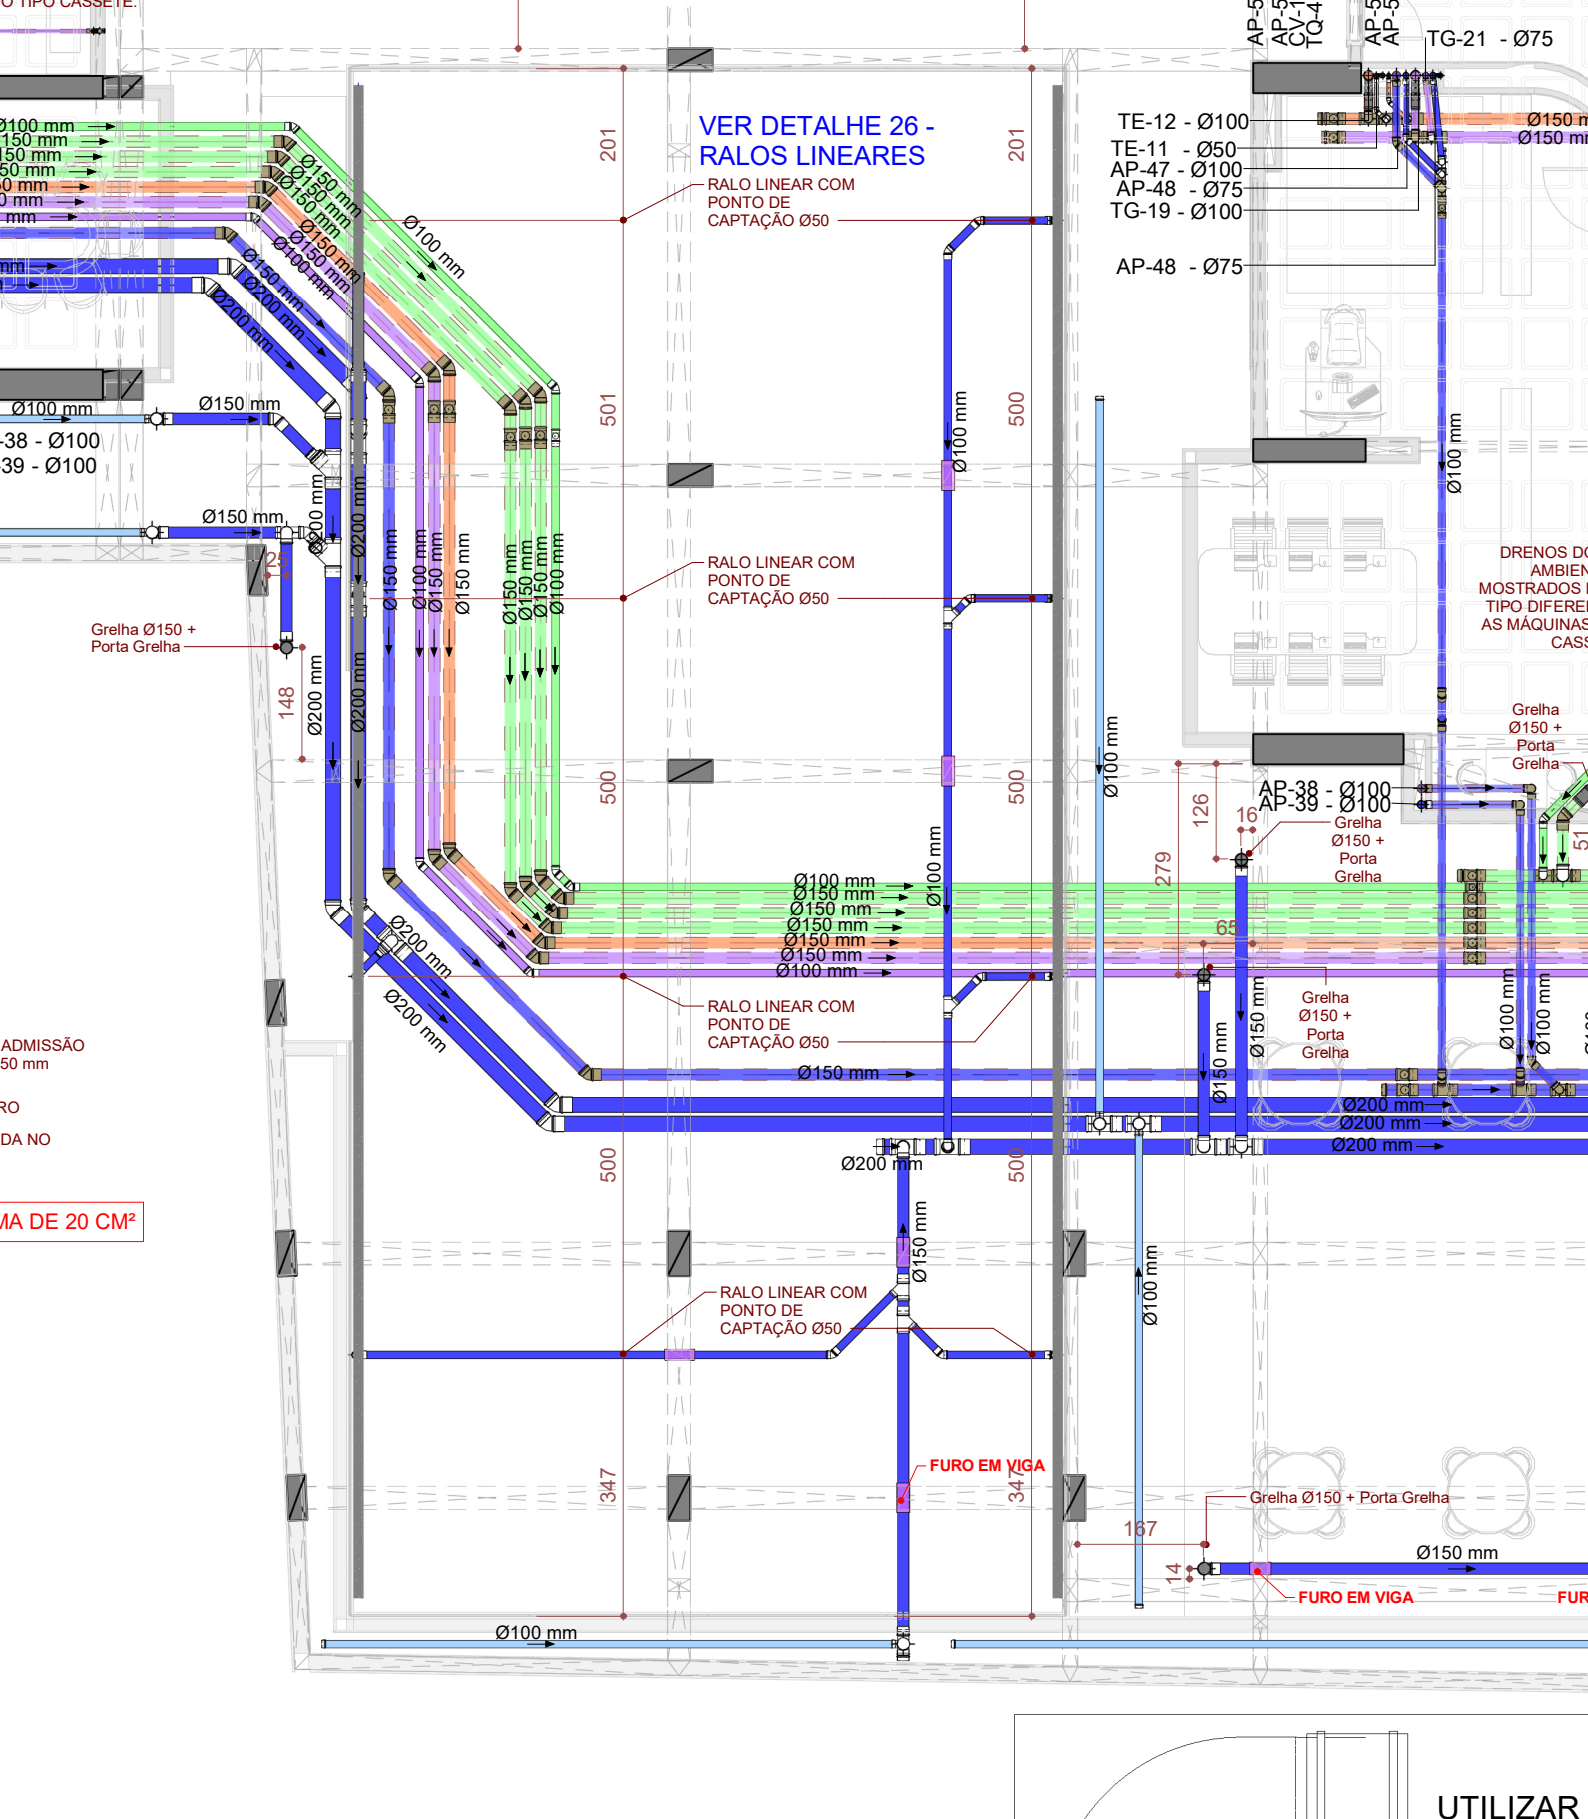
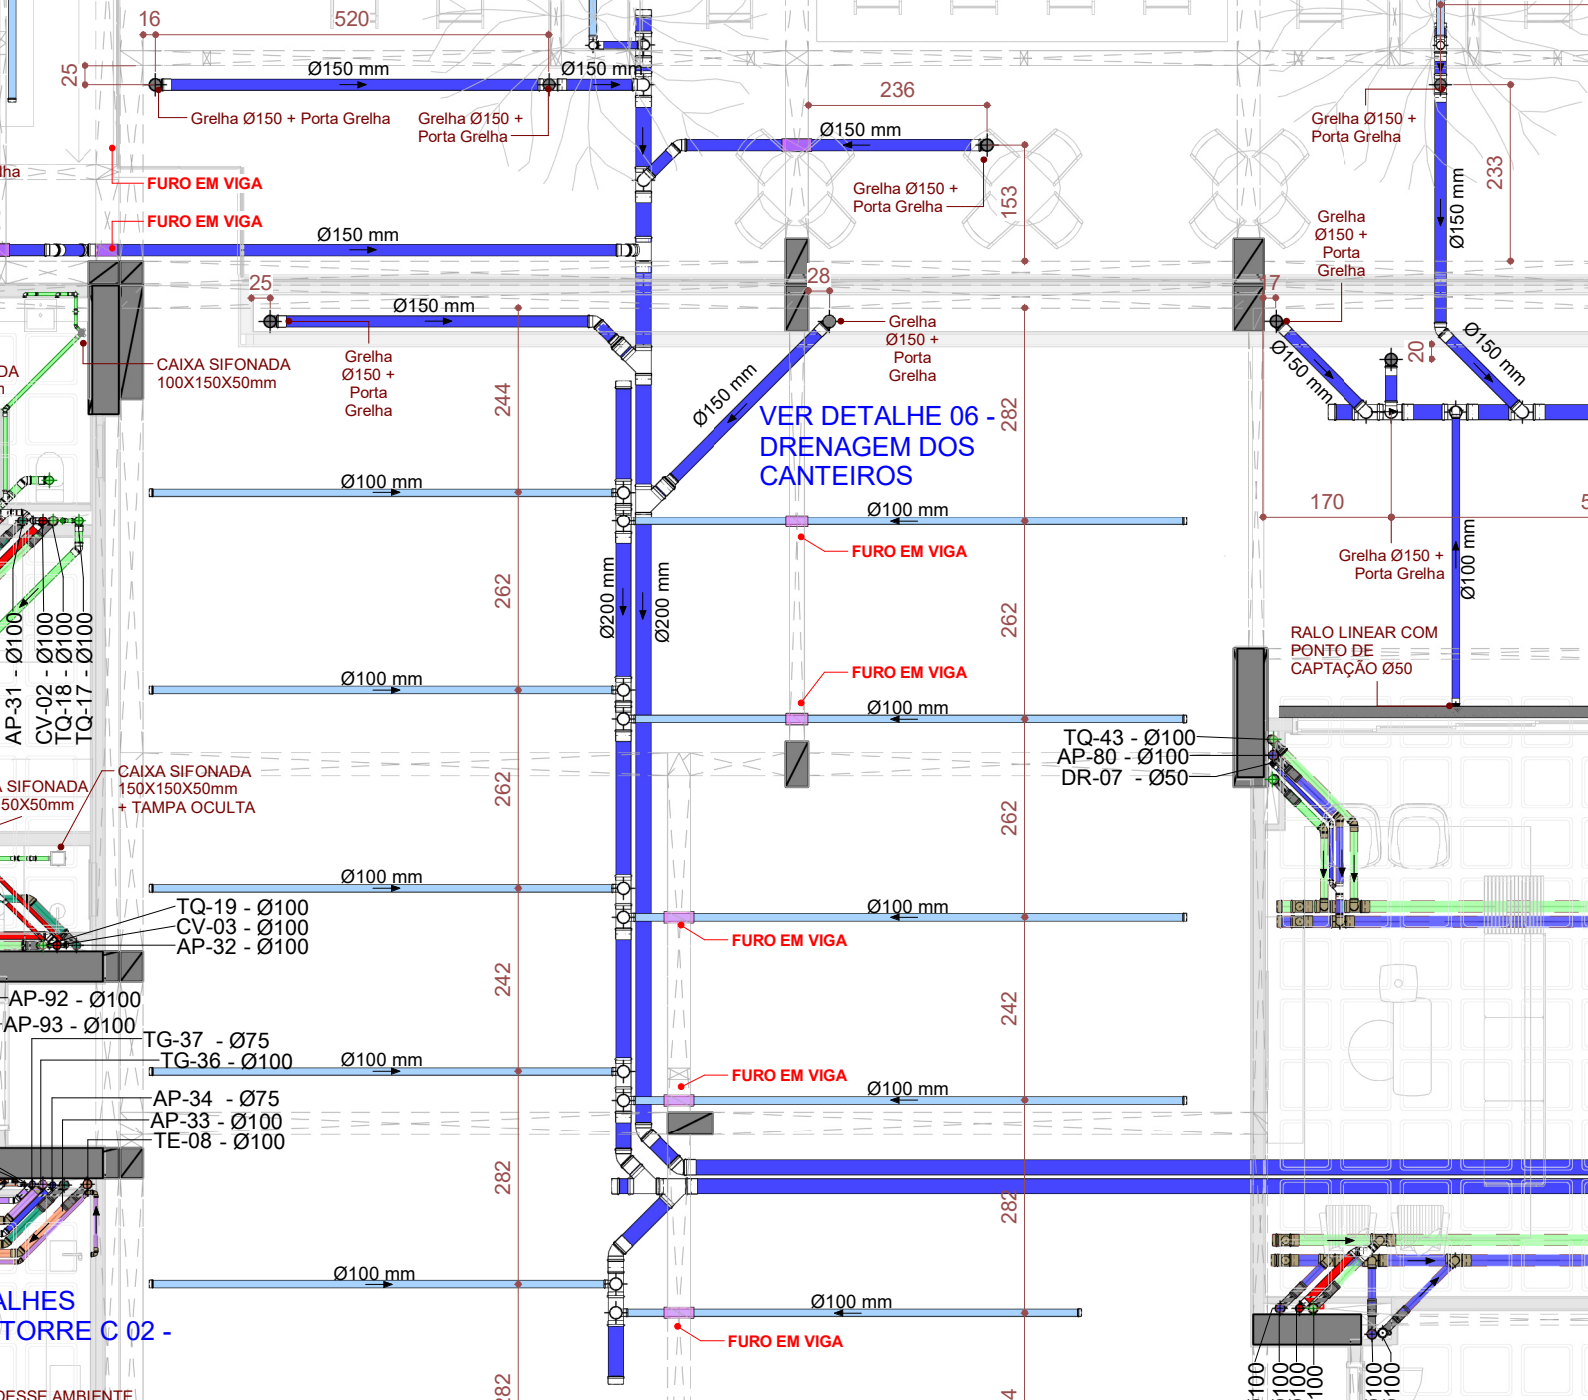
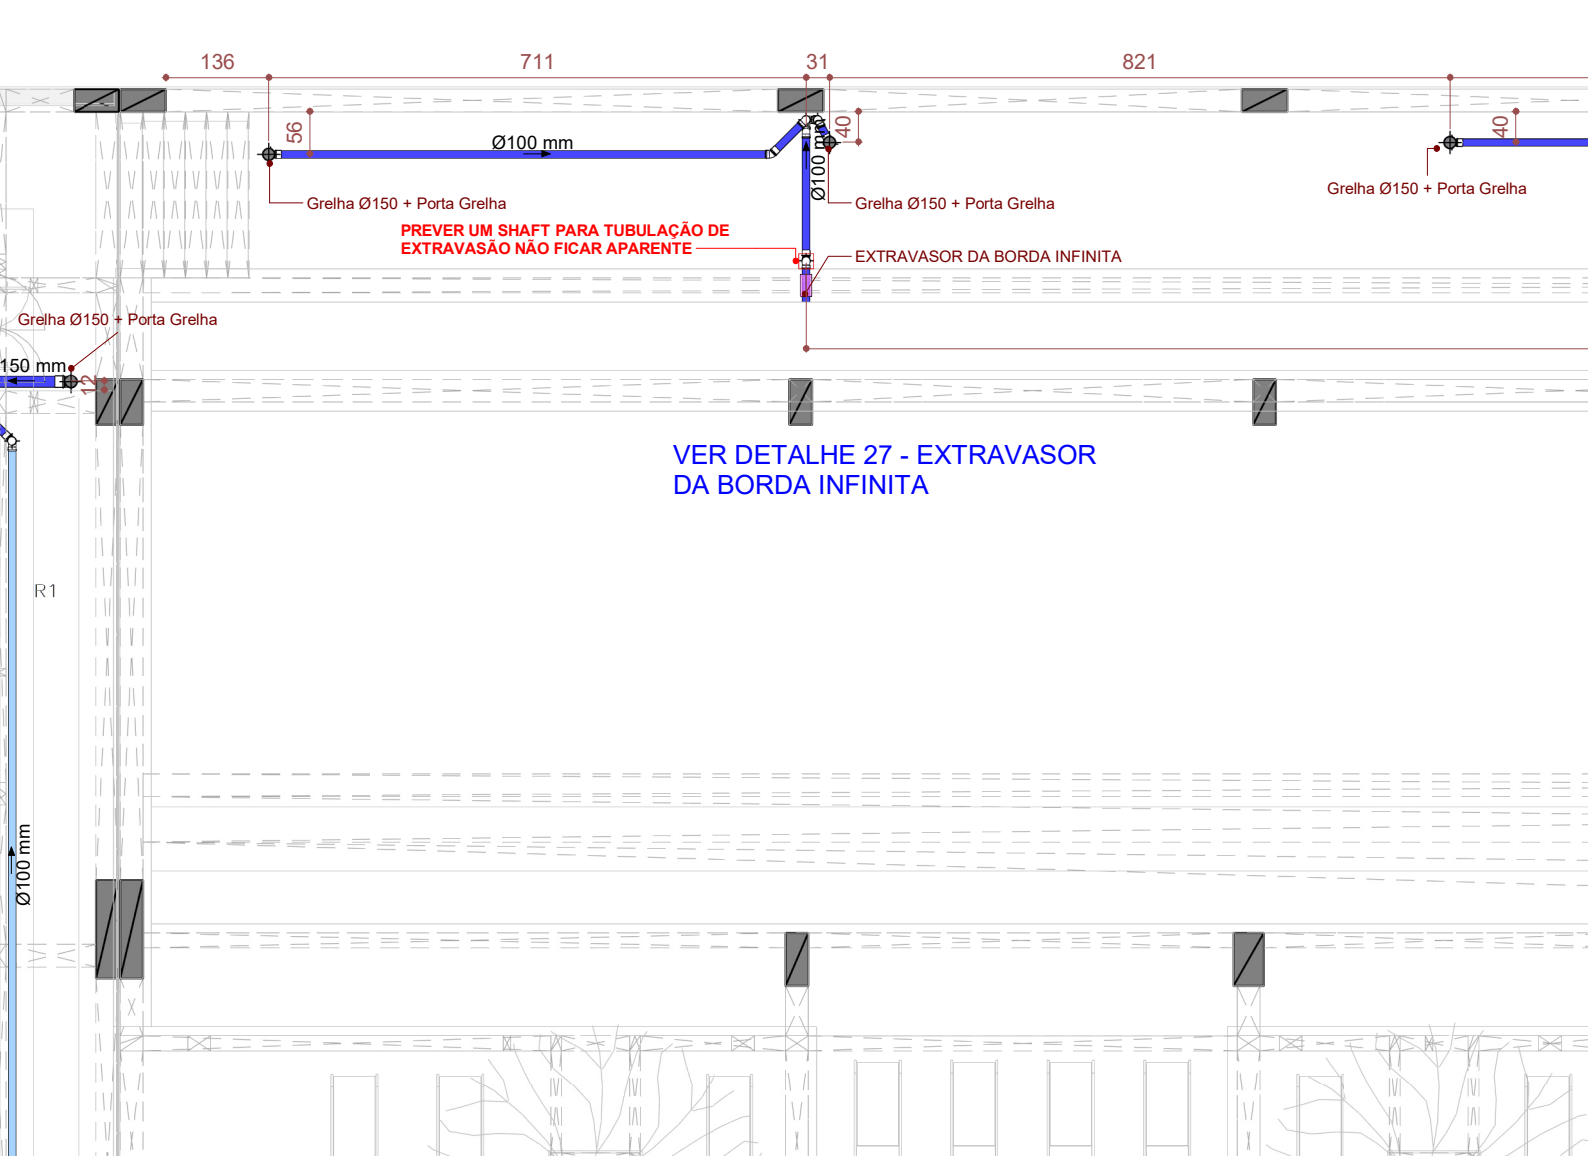
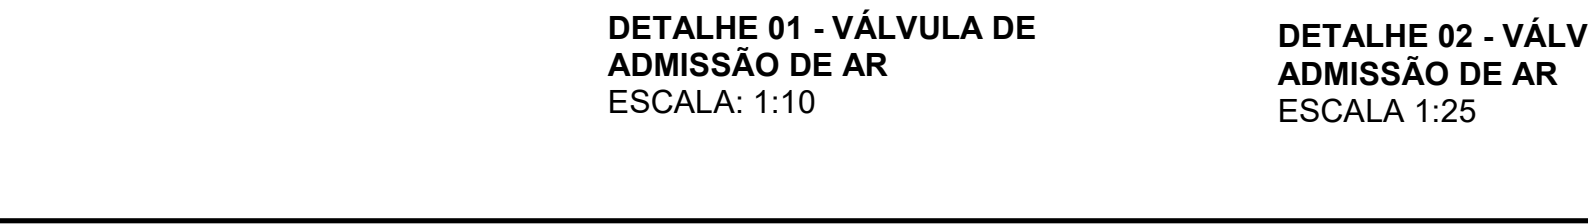
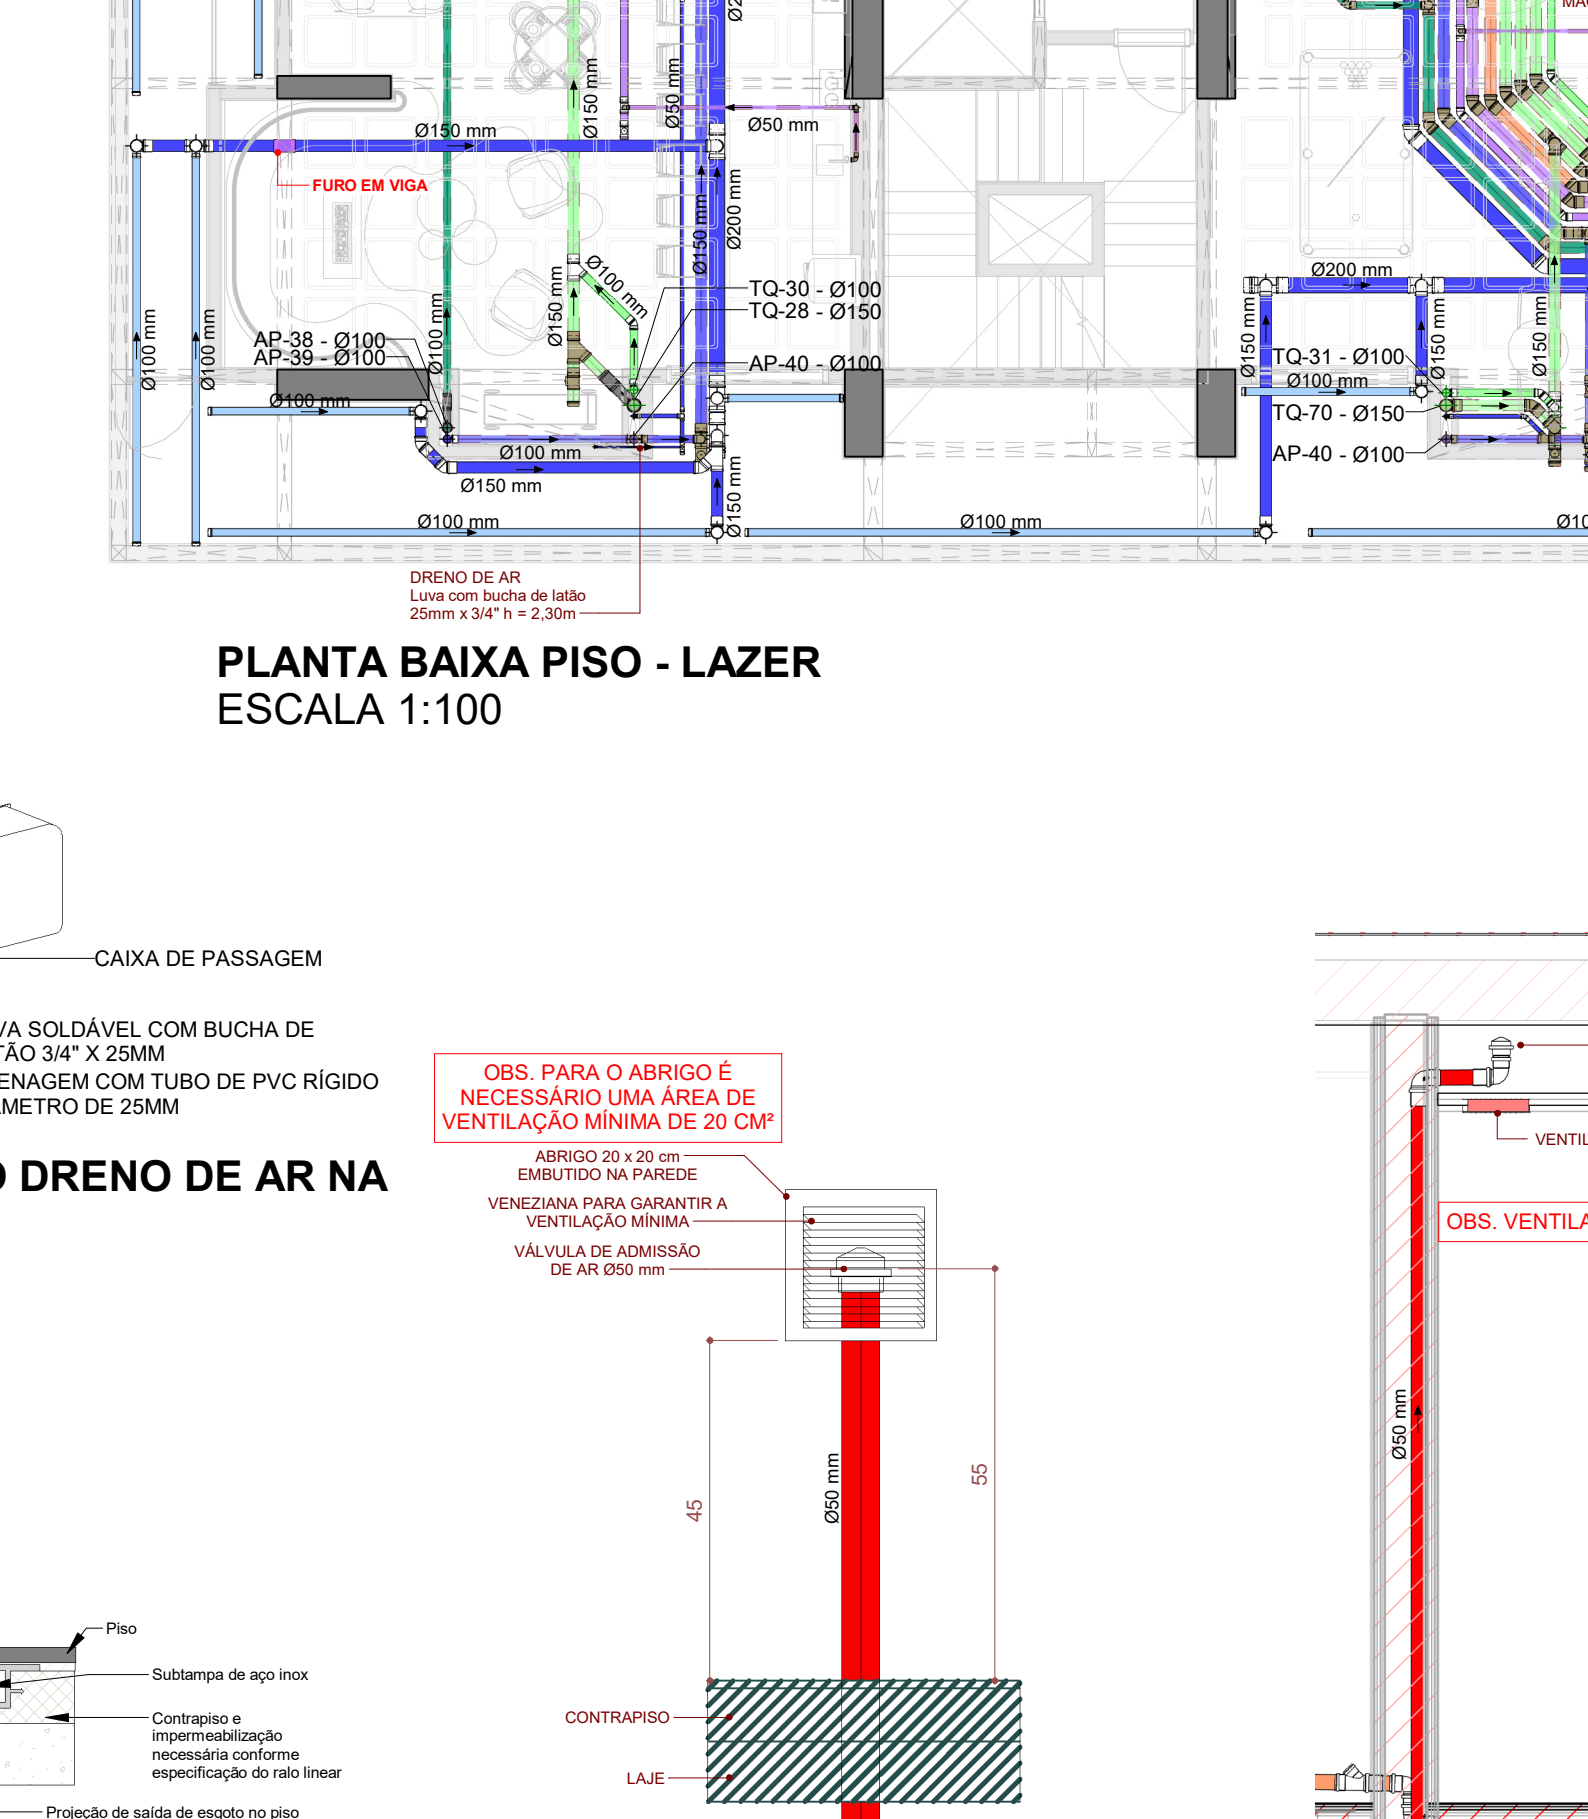
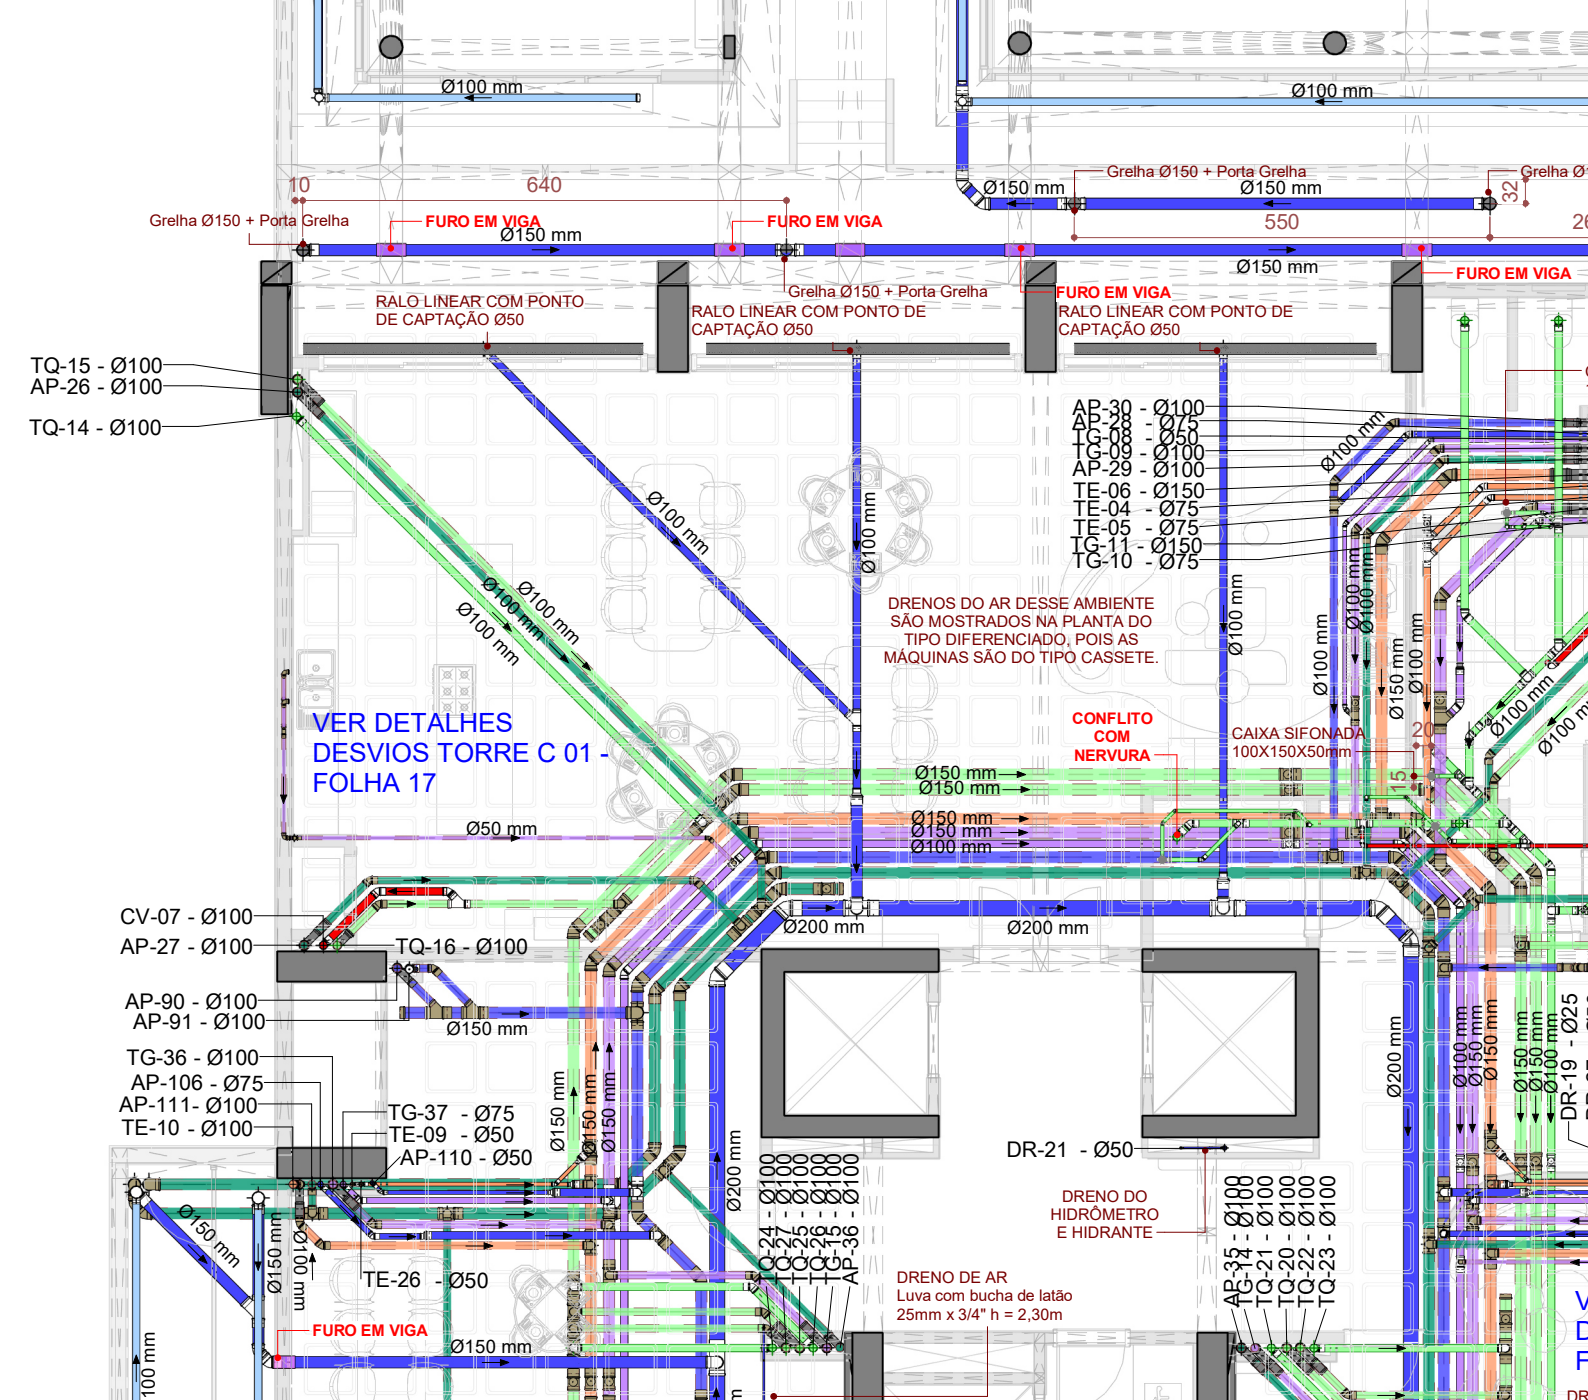
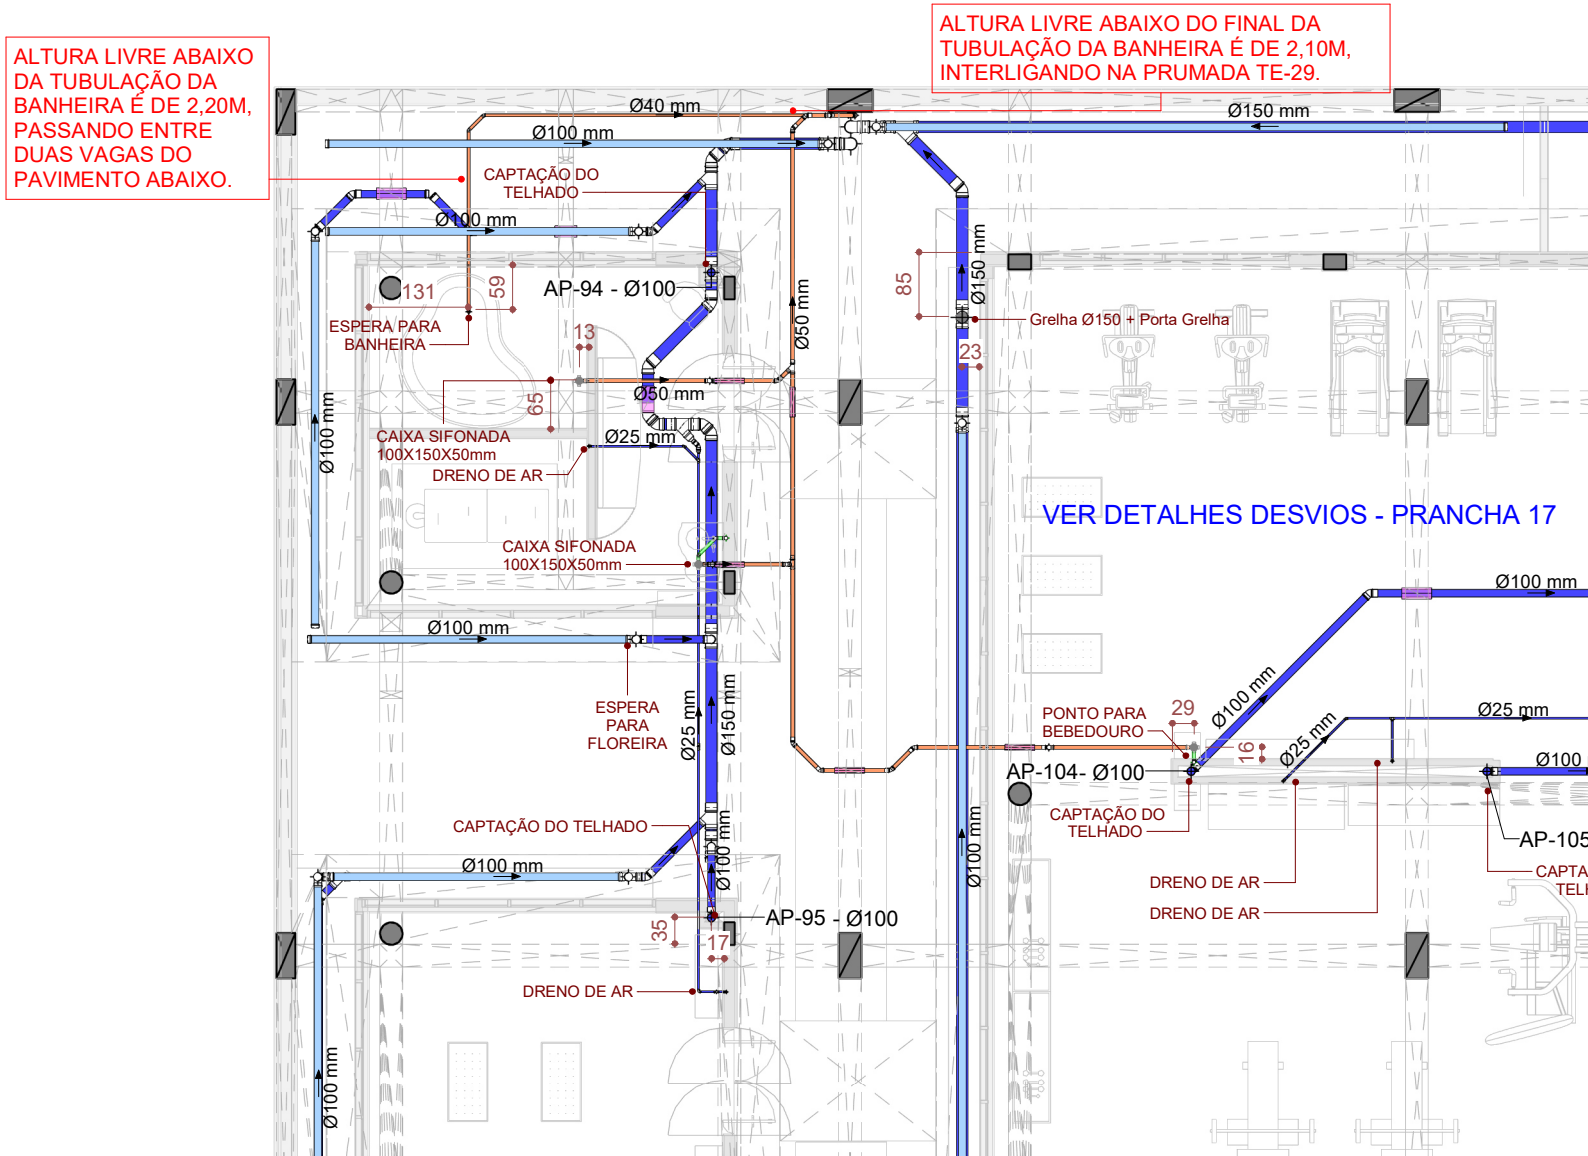
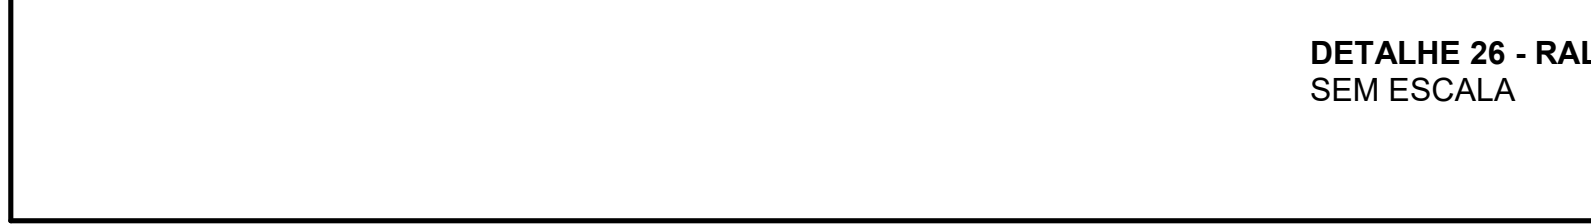
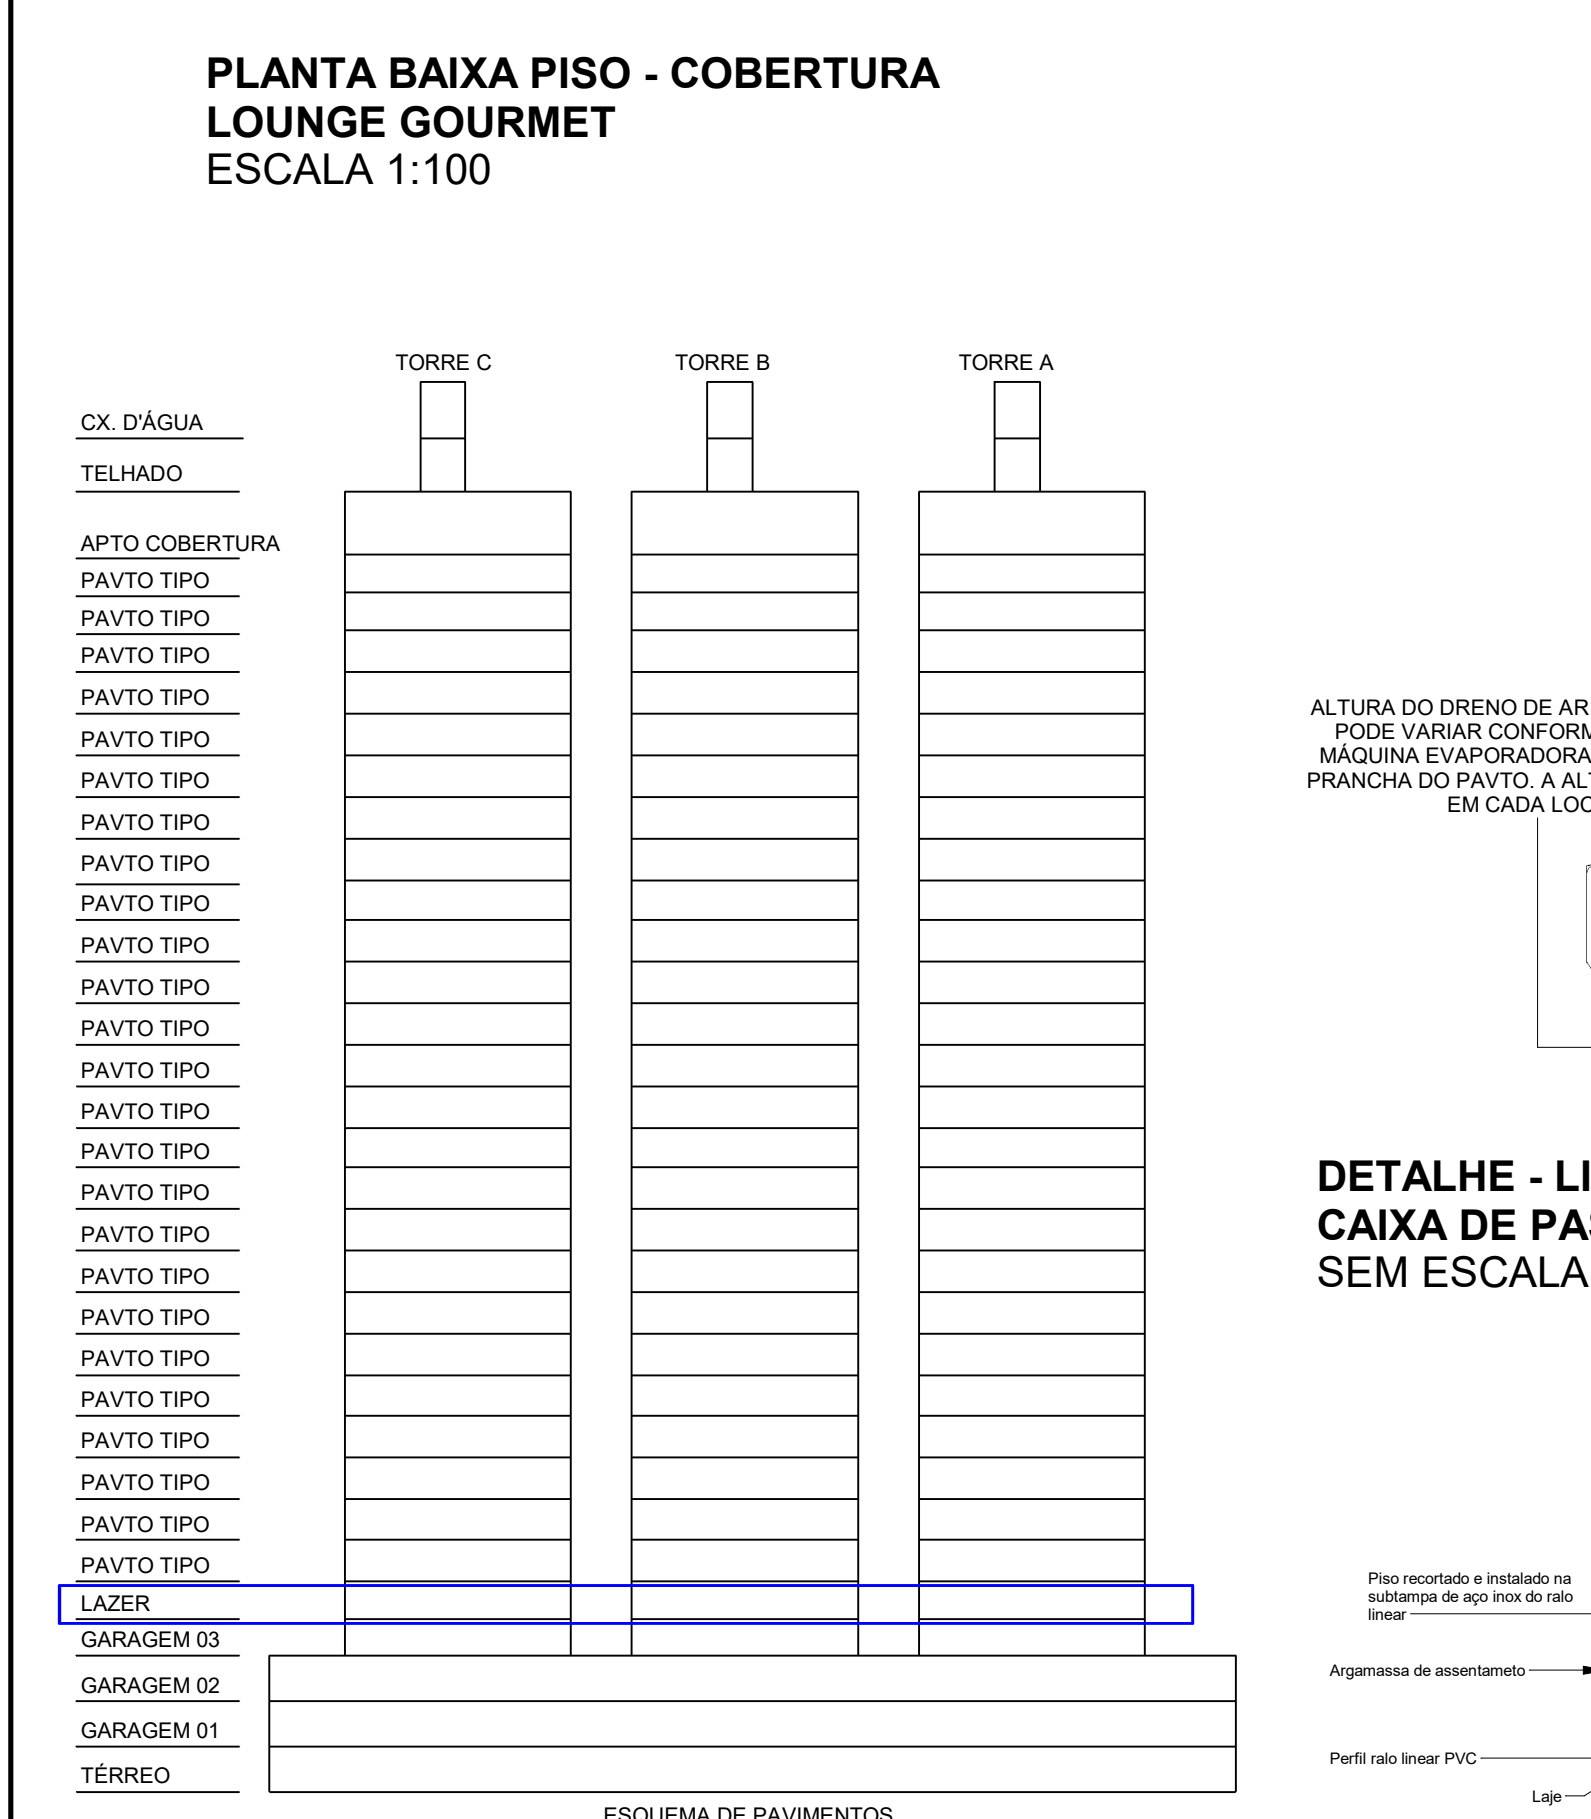
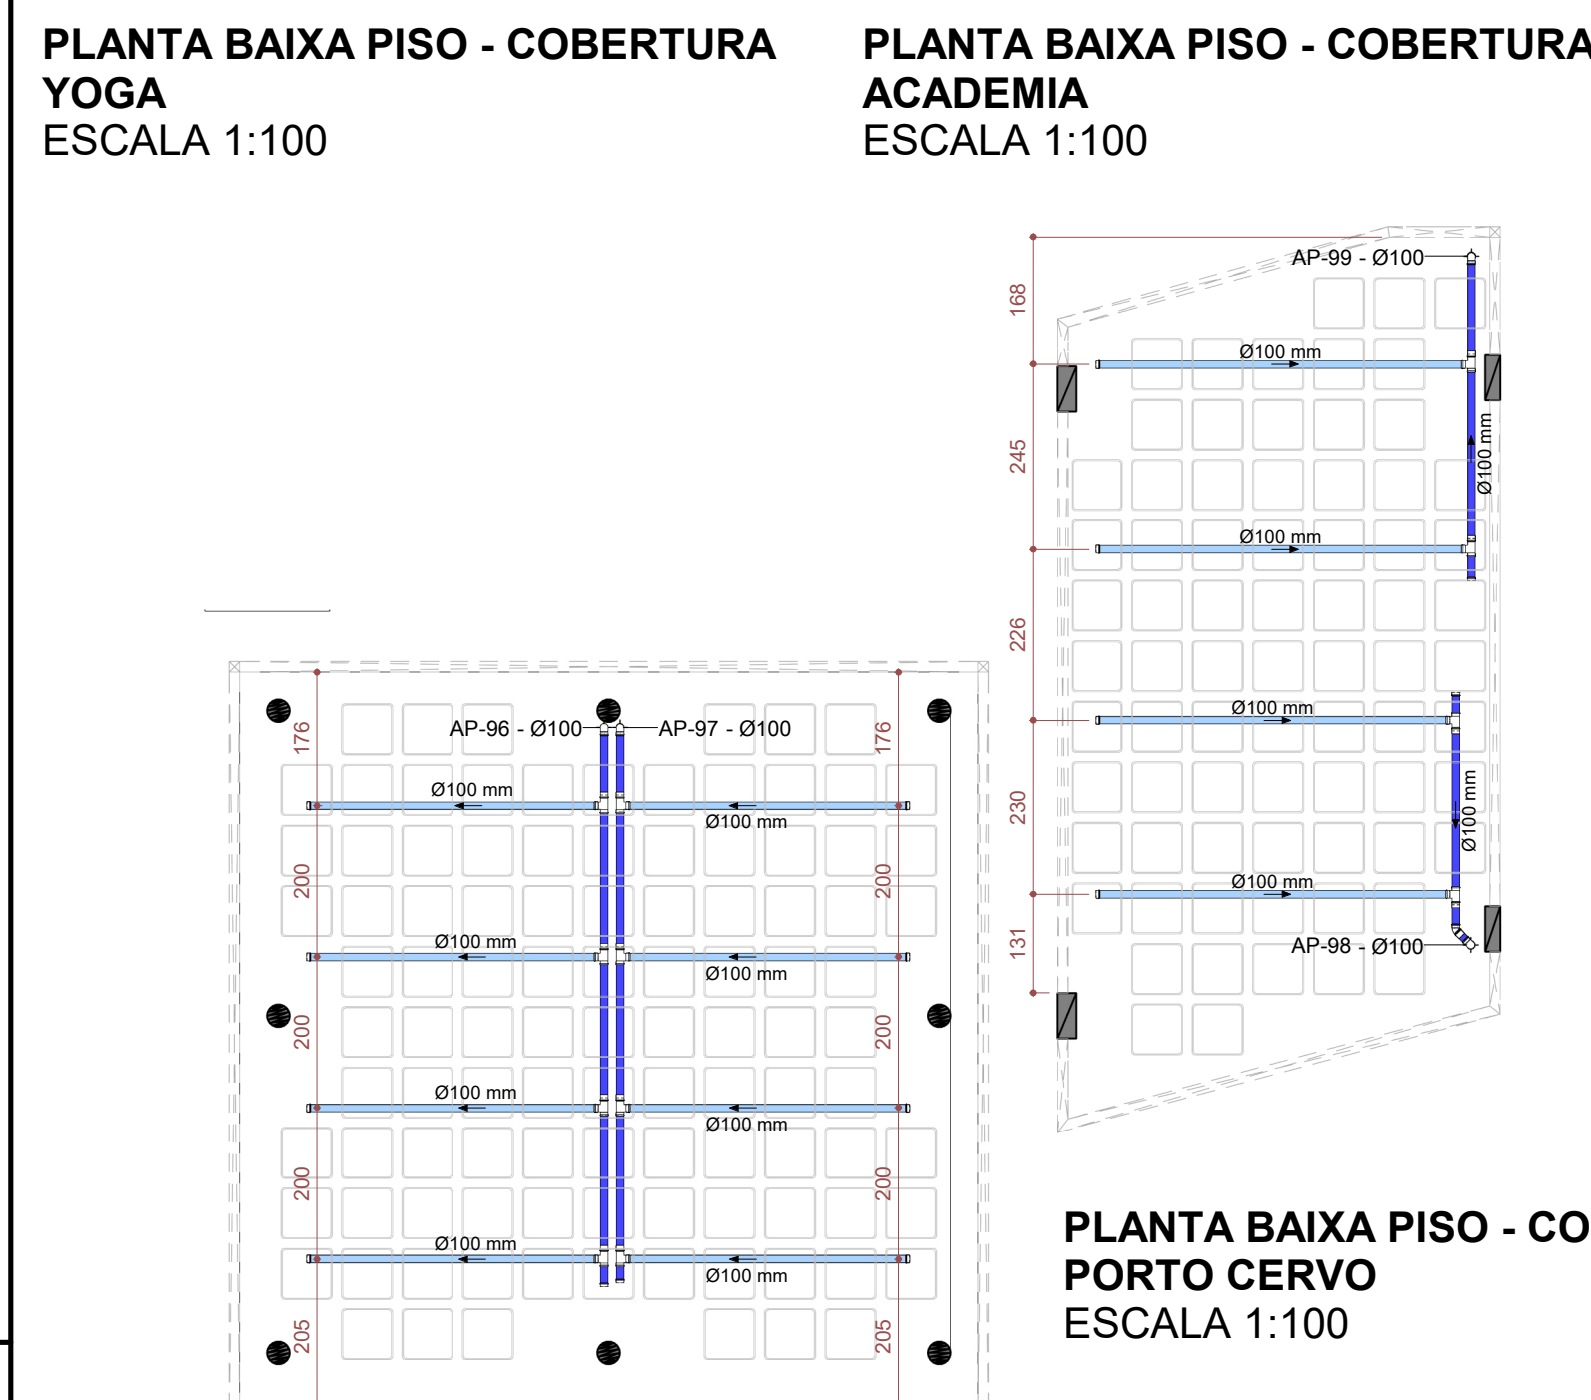
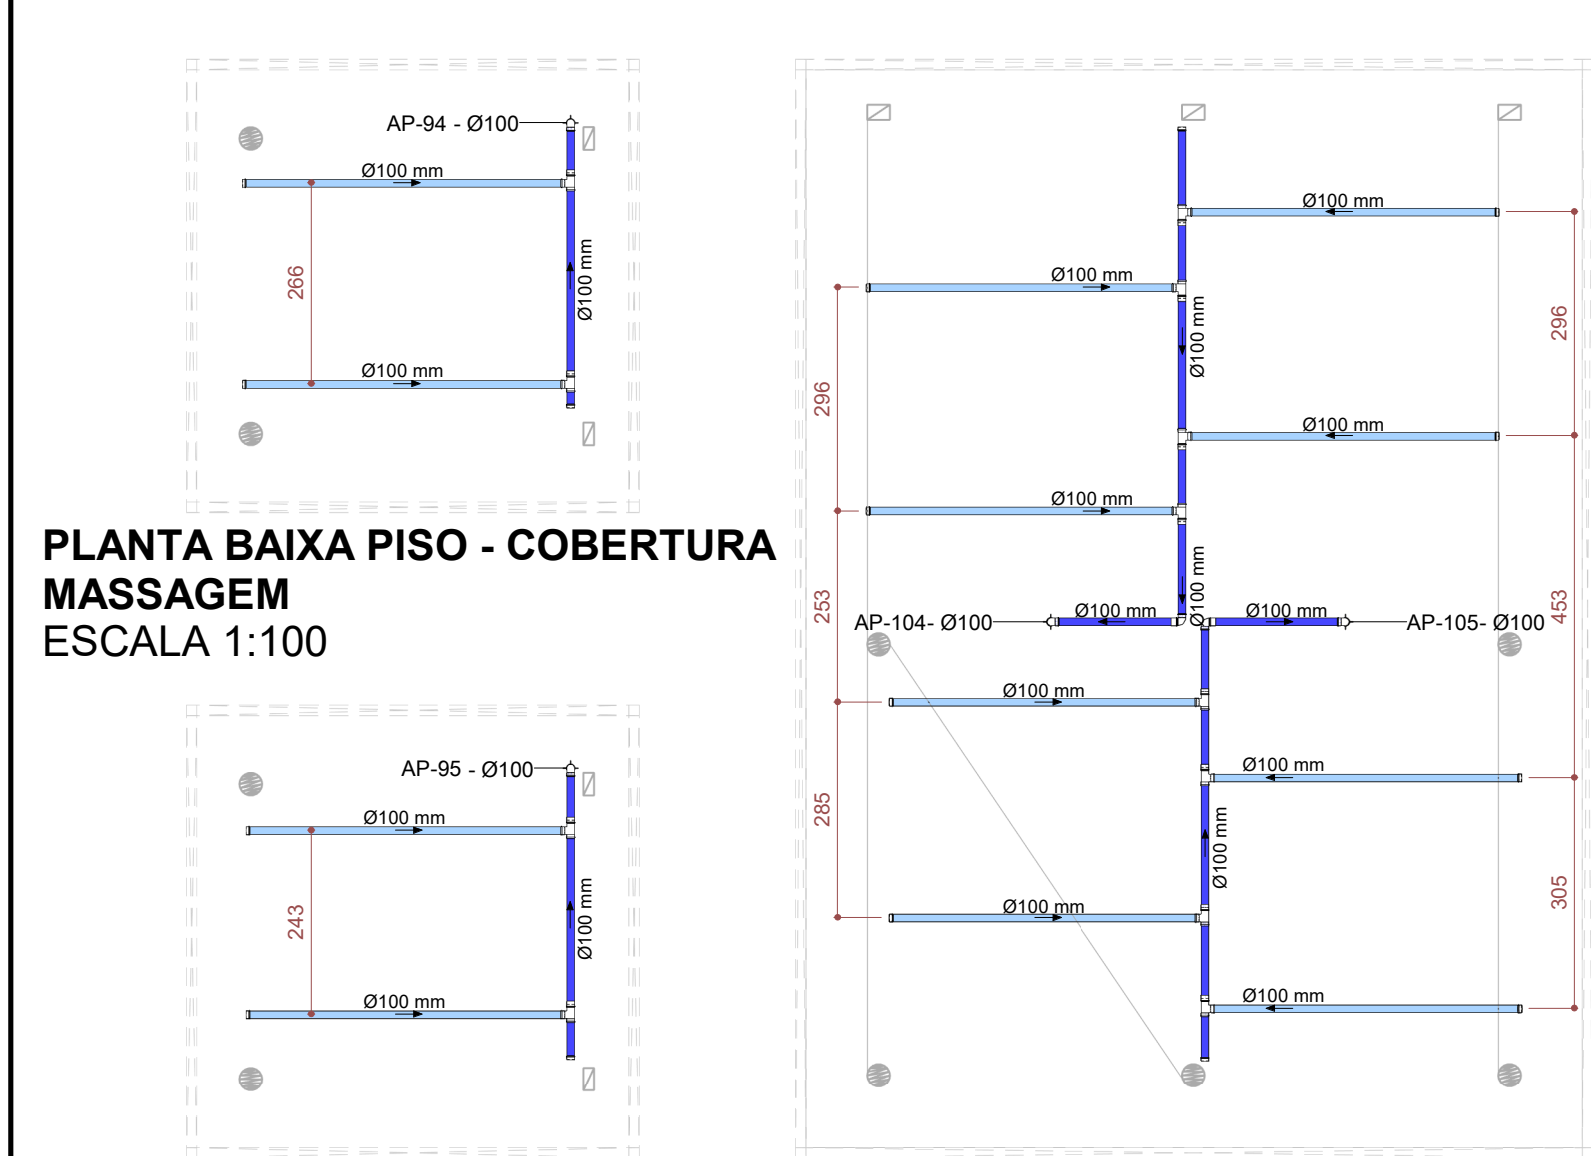


LEGENDA	
TUPO DE ESGOTO PVC - DIÂMETRO INDICADO	TUPO DE DRENAGEM AR TIPO CASSETTE PVC - DIÂMETRO INDICADO
TUPO DE VENTILAÇÃO PVC - DIÂMETRO INDICADO	CONEXÕES Linha Silenciosa - DIÂMETRO INDICADO
TUPO DE DRENAGEM PVC - DIÂMETRO INDICADO	CONEXÕES Série Reforçada - DIÂMETRO INDICADO
TUPO DE ESPUMA PVC - DIÂMETRO INDICADO	CURVA LONCA SÉRIE REFORÇADA C/FIBRA DE VIDRO - DIÂMETRO INDICADO
TUPO DE GORDURA PVC - DIÂMETRO INDICADO	TUBO DRENO FLEXÍVEL PVC - DIÂMETRO INDICADO
TUPO (SISTEMA CONFORME CORES ACIMA) Linha Silenciosa - DIÂMETRO INDICADO	CG CAIXA DE GORDURA
TUPO (SISTEMA CONFORME CORES ACIMA) Linha Reforçada - DIÂMETRO INDICADO	CS CAIXA DE SABÃO
AP-00	PRUMADA DE CAPTAÇÃO DE ÁGUA PLUVIAL - NUMERAÇÃO
TQ-00	PRUMADA DE CAPTAÇÃO DE ESGOTO - NUMERAÇÃO
CV-00	PRUMADA DE VENTILAÇÃO SECUNDÁRIA - NUMERAÇÃO
PIA	PIA DE COZINHA
MLR	MÁQUINA DE LAVAR ROUPA
LV	LAVATÓRIO
FURTO EM VIGA	VER PROJETO DE FURAÇÃO
CA	CAIXA DE DRENAGEM/ARMAZENAMENTO

OBSERVAÇÕES DE PROJETO:
NOTA 01: AO FINAL DE TODAS AS COLUNAS DE VENTILAÇÃO DEVERÁ TER UM TERMINAL DE VENTILAÇÃO, UM TÉ OU OUTRO DISPOSITIVO QUE IMPEÇA A ENTRADA DE ÁGUAS PLUVIAIS NA TUBULAÇÃO.
NOTA 02: AS CAIXAS DE INSPEÇÃO E GORDURA DEVERÃO SER EXECUTADAS CONFORME DETALHES E PERMITIR LIMPEZA E MANUTENÇÃO.
NOTA 03: A LIMPEZA DA CAIXA DE GORDURA DEVERÁ SER FEITA A CADA SEIS MESES.
NOTA 04: A LIMPEZA DAS CALHAS E DE TODAS AS CAIXAS DO SISTEMA DE TRATAMENTO DE ESGOTO DEVERÁ SER FEITA A CADA UM ANO.
NOTA 05: INCLINAÇÕES DA TUBULAÇÃO: PVC Ø250 mm a PVC Ø200mm = 0,5%
PVC Ø150mm; Ø100mm = 1,0%
PVC Ø75mm; PVC Ø60mm; PVC Ø40mm; PVC Ø20mm = 2,0%
NOTA 06: ESTE PROJETO FOI PROJETADO E DIMENSIONADO COM UMA VIDA ÚTIL DE PROJETO DE 20 ANOS DE FORMA QUE ATENDA OS REQUISITOS MÍNIMOS DE DESEMPENHO DA NORMA NBR 15709, SUPONDO O ATENDIMENTO DA PERIODICIDADE E CORRETA EXECUÇÃO DOS PROCESSOS DE MANUTENÇÃO.
NOTA 07: O RALO OU CAIXA SIFONADA QUE ATENDE A MÁQUINA DE LAVAR POSSUI DISPOSITIVO ANTI-ESPUMA.

Nessa planta se encontram os detalhes A4 do número 24 ao 27.		
ARQUIVO BASE	NOME DO ARQUIVO	RECEBIDO EM
PROJETO ARQUITETÔNICO	BOC-EXE-ARQ-EMB	20-04-2023
PROJETO ESTRUTURAL - IFC	BOC-EST-PRF	20-04-2023
PROJETO ESTRUTURAL - DWG		
PROJETO INTERIORES		
PROJETO PAISAGISMO		
PROJETO LUMINOTÉCNICO		
PROJETO TOPOGRÁFICO		
PROJETO AUTOMAÇÃO		
LISTA DE DEFINIÇÕES	RESPONSÁVEL PELA RESPOSTA	RECEBIDO EM
FUROS APROVADOS	20035-HSL-DEFINIÇÕES-11-03-2022	11-02-2022

RV03 01-12-2022 DRENAGEM DE FLOREIRA REMOVIDA DE ACORDO COM O RELATÓRIO RECEBIDO NO DIA 19-09-2023 DANIEL

RV02 26-04-2023 AJUSTES CONFORME RELATÓRIO DE ANÁLISE 03-04-23, RELATÓRIO DE FURAÇÃO 19-04-23 E ITENS DO CONSTRUÇÃO LETICIA

RV01 08-03-2023 AJUSTES CONFORME RELATÓRIO DE ANÁLISE RECEBIDO DIA 13-02-2023 LETICIA

RV00 16-12-2022 FASE 03 - EMISSÃO INICIAL LETICIA

REVISÃO DATA DESCRIÇÃO RESPONSÁVEL

thórus
engenharia

PROJETO SANITÁRIO E PLUVIAL

OBRA
BRAVA OCEAN

PROPRIETÁRIO
RUA CAPO - POLÍCIA MILITAR ANTÔNIO RUDOLF, 155, PRAIA BRAVA, ITAJAÍ

CONSTRUTORA
CN CONSTRUTORA E INCORP. LTDA

CONTATO
PLANTA BAIXA PISO - LAZER

05/21

EQUIPE TÉCNICA
AMANDA LARENTIS
GUILHERME LARENTIS
RAIL PEDRO ESKELSEN

OUTRO RESPONSÁVEL
RUA DO CARVALHO, 1555
BARRIO CENTRO - BALNEARIO CAMBOREUI
FONE (47) 3333-1111
FAX (47) 3333-1111