


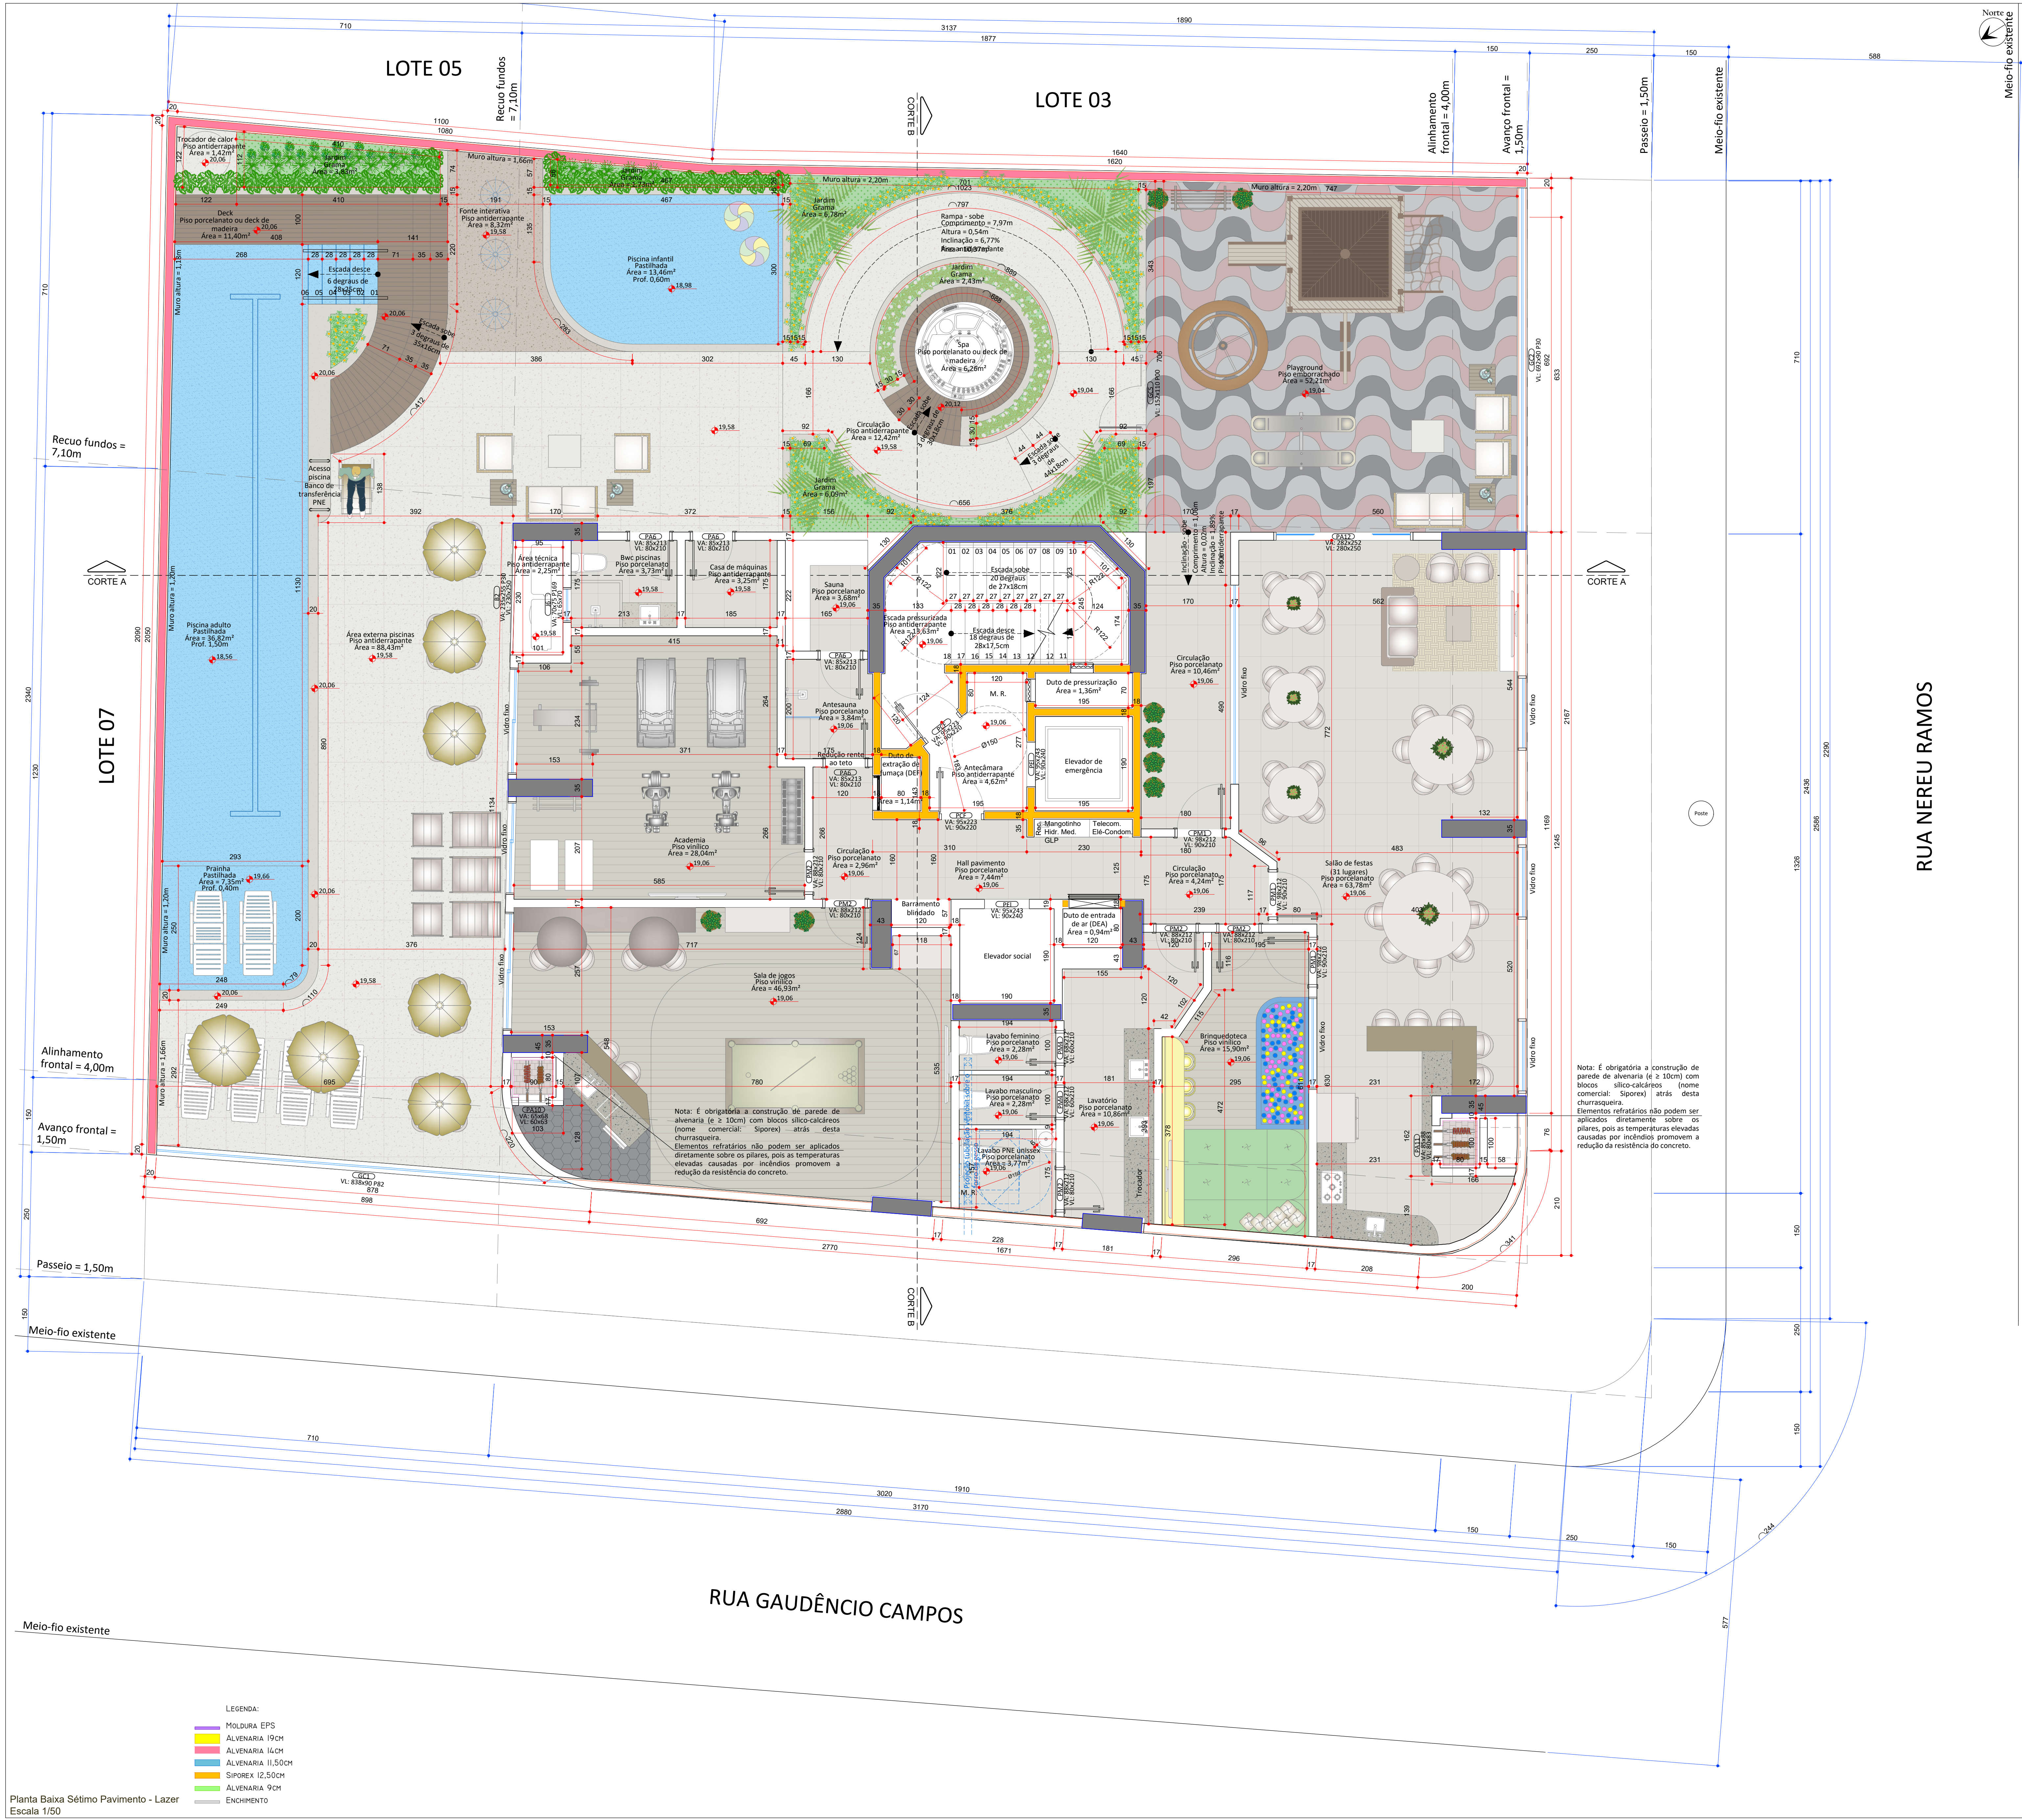

OBSERVAÇÕES:			
- CASO DIVIRJA COTA E ESCALA, PREVALECE A COTA.			
02	AJUSTES DE COMPATIBILIZAÇÃO: ALTERAÇÃO DA POSIÇÃO DA PORTA DA ANTECÂMARA DEVIDO AJUSTE DO DEF. AJUSTES DE PILARES NO ENTORNO DO ELEVADOR SOCIAL/ RETORNO DE SELO EM PRANCHA	17/05/2023	GRAYCE/IGNACIO
01	AUMENTO DAS FONTES DOS TEXTOS E COTAS	06/12/2022	GRAYCE/IGNACIO
REVISÃO	DISCRIMINAÇÃO	DATA	AUTOR

CARIMBOS:

PROPRIETÁRIO: GAUDÊNCIO CAMPOS EMPREENDIMENTOS IMOBILIÁRIOS LTDA Avenida Senador Atilio Fontana, nº 1159, Sala 01, Balastrado Perequê, Porto Belo/ SC CEP 88.210-000 Telefone: (47) 3369-6859	
	PROJETO ARQUITETÔNICO GRAYCE SUELEN ARQUITETURA E URBANISMO EIRELI Rua Benjamin Franklin Pereira, nº 377, Sala 103, Bairro São João, Itajaí/ SC CEP 88.304-070 Telefone: (47) 99985-0082
Prefeitura de Porto Belo - SC Secretaria de Planejamento Urbano	ASSINATURAS IVAN BUHLER-97028380025 Assinado de forma digital por IVAN BUHLER-97028380025 Dados: 2023.05.18 11:25:19 -03'00' PROPRIETÁRIO: Gaudêncio Campos Empreendimentos Imobiliários LTDA CNPJ 43.338.805/0001-08 GRAYCE SUELEN DE LIMA-05908244902 Assinado de forma digital por GRAYCE SUELEN DE LIMA-05908244902 Dados: 2023.05.17 22:35:57 -03'00' RESP. TÉCNICO PELO PROJETO: Grayce Suelen de Lima CAU/SC: 968076-0 ANNE ELZA GEREMIAS-05335808977 Assinado de forma digital por ANNE ELZA GEREMIAS-05335808977 Dados: 2023.05.18 13:15:59 -03'00' RESP. TÉCNICO PELO PROJETO: Anne Elza Geremias CAU/SC: A115914-3
Protocolo nº	
Data:	
FUNCIONÁRIO RESPONSÁVEL	

PROJETO ARQUITETÔNICO LEGAL	
CATEGORIA Edifício Comercial e Residencial Multifamiliar	DATA 25/04/2023
NOME/OBRA Mirador de Alicante	DESENHO Grayce/Ignacio/ Anne
ASSUNTO Planta Baixa Sétimo Pavimento - Lazer	ESCALA indicada
EMPREENHEO DA OBRA Rua Nereu Ramos, esquina com a Rua Gaudêncio de Campos, Perequê, Porto Belo/ SC.	FOLHA 09/15