


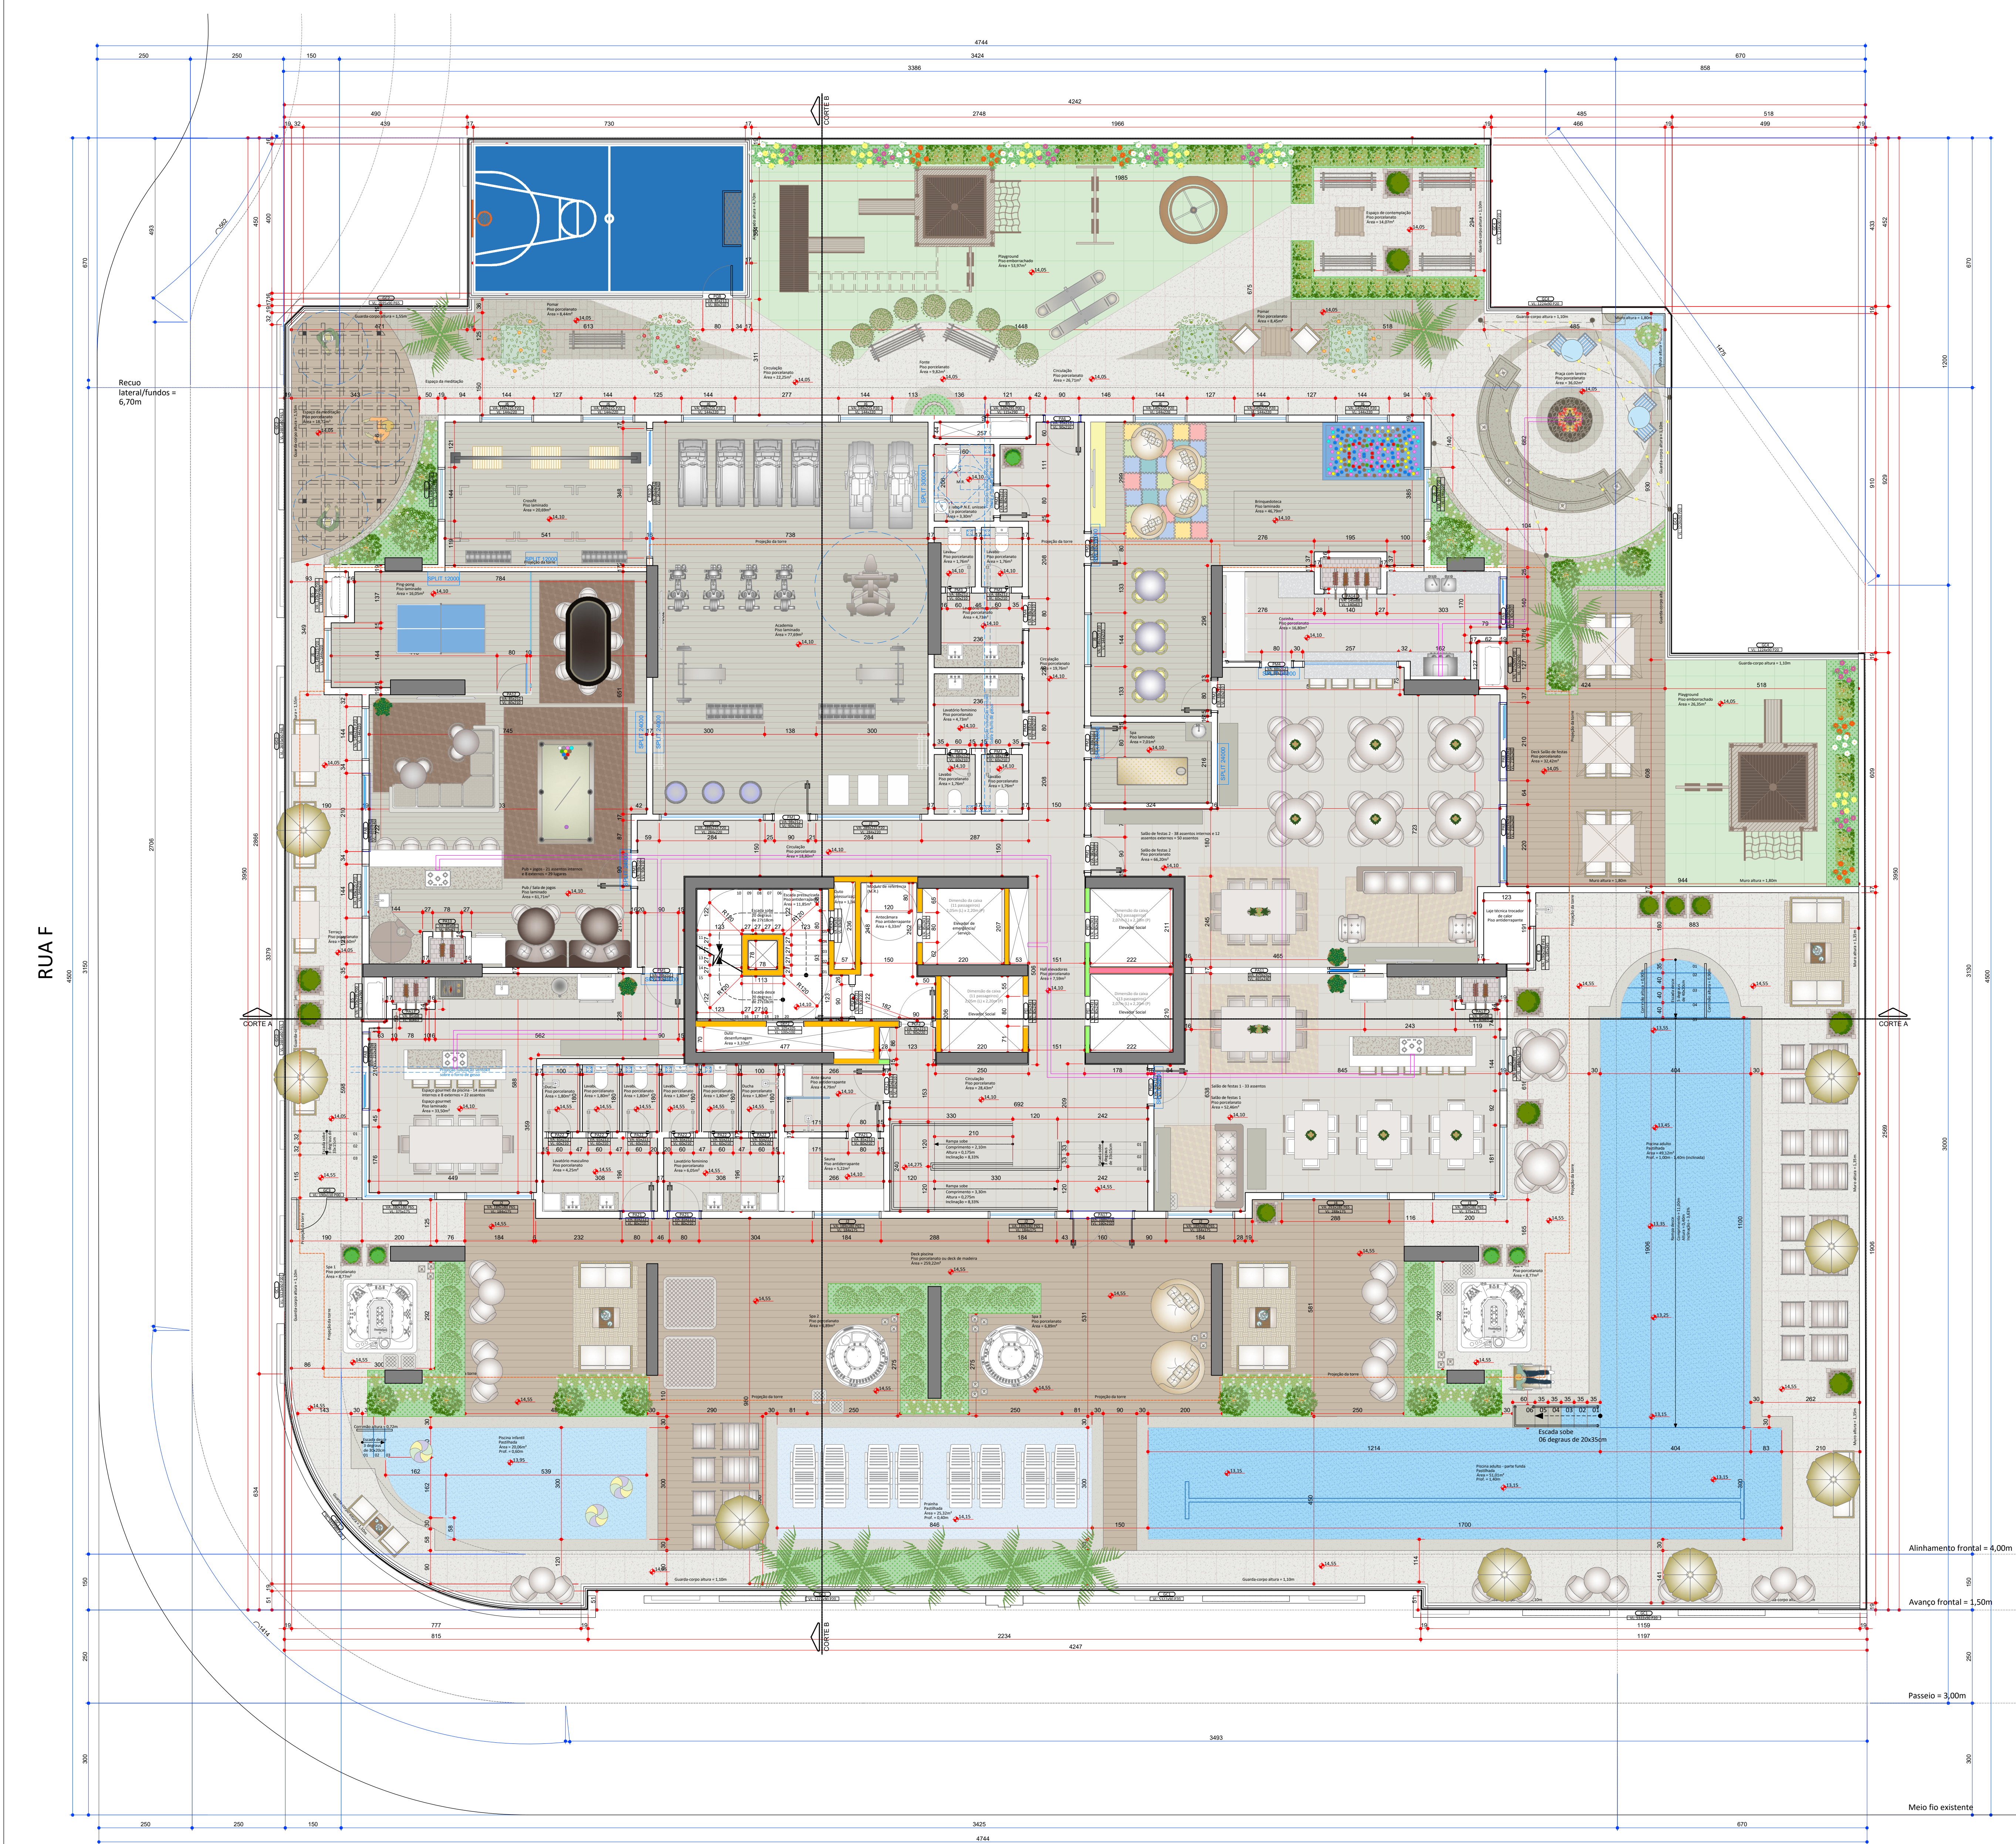

Planta Baixa Pavimento diferenciado (Lazer)
Escala 1/75

AVENIDA TABELIÃO NOMI JACÓ CRUZ



TABELA DE REVISÕES DOS PROJETOS FINAIS (PARA ALTERAÇÕES APÓS DIVULGAÇÃO OFICIAL NA LISTA MESTRA)			
Revisão	Discriminação	Data	Desenho
00	Emissão inicial do projeto para obra - Alterações pós aprovação do projeto: Terço: espelhamento dos vasos nos lavabos comerciais para alinhamento à norma PNE; inserção de pias para cuba nas salas comerciais; aumento da subestação e redução do bioclimatário.	24/08/2022	Grayce/ Ignácio
01	Todas pranchas: alteração para sete executivo e tabela de revisões Lista Mestra. Terço: alteração na disposição dos boxes de praia; inclusão pilaretes subestação; acréscimo de porta entry Garagem e acesso Boxes de praia conforme PPCI.	08/11/2022	Grayce/ Ignácio
02	Ajuste na representação de 6 floreiras, transformando 3 para vegetação em vasos, e 3 floreiras com alvenaria no entorno devido não terem sido nobilissimas.	09/04/2024	Grayce/ Ignácio

TABELA DE REVISÕES DOS PROJETOS EM DESENVOLVIMENTO (PARA ALTERAÇÕES ANTES DA DIVULGAÇÃO OFICIAL NA LISTA MESTRA)			
Revisão	Discriminação	Data	Desenho

Proprietário
JARDINS DE VERSALHES EMPREENDIMENTOS SPE
LTDA 42.614.928/0001-06 - CNPJ
Obras/ Endereço
EDIFICAÇÃO MULTIFAMILIAR E COMERCIAL
JARDINS DE VERSALHES
Av. Tabeião Nomi Jacó Cruz, esq. com a Rua F, Bairro Perequê,
Porto Belo - SC.
Conteúdo
PROJETO ARQUITETÔNICO EXECUTIVO
Planta Baixa Pavimento diferenciado (Lazer)

Autor
Grayce Suelen de Lima/ Ignácio Azzolini Junior
Arquivo
JV-3° Prot_EXE R01
Observações
- CASO DIVERJA COTA E ESCALA, PREVÁLECE A COTA.



EXE-ARQ
07-17