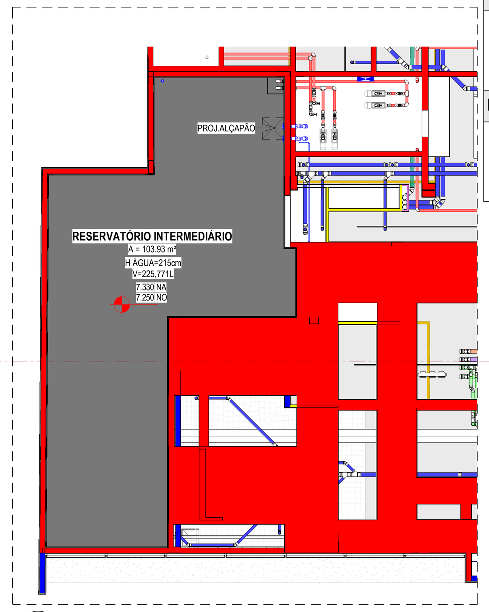


PB.06 A — PLANTA RESERVATÓRIO INTERMEDIÁRIO +7,25
ESCALA 1 : 150

LEGENDA NOMENCLATURA CORTES E ELEVAÇÕES

XX.YY / FL.ZZZ
XX = TIPO DESENHO (PLANTA, CORTE, ELEVAÇÃO)
YY = NUMERO DESENHO
ZZZ = NUMERO DA FOLHA DO DESENHO

LEGENDA NOMENCLATURA DETALHES

XX.YY / FL.ZZZ
XX = TIPO DESENHO: DAM (DETALHE ÁREA MOLHADA) - DET (DETALHES GERAIS) - CP (COMPATIBILIZAÇÃO)
YY = NUMERO DESENHO
ZZZ = NUMERO DA FOLHA DO DESENHO

LEGENDA NÍVEIS

NÍVEL NA = NÍVEL PISO ACABADO
NÍVEL NO = NÍVEL PISO OSSO
OBS.: NÍVEL ENC = NÍVEL TOPO ENCHIMENTO

LEGENDA PAREDES

ESTRUTURA DE CONCRETO MOLDADO "IN LOCO"	BLOCO DE CONCRETO CELULAR 15cm.
BLOCO CERÂMICO DE VEDAÇÃO 5cm.	BLOCO DE CONCRETO CELULAR 20cm.
BLOCO CERÂMICO DE VEDAÇÃO 9cm.	PLACA DRY-WALL CHAPA TIPO ST 6cm.
BLOCO CERÂMICO DE VEDAÇÃO 14cm.	PLACA DRY-WALL CHAPA TIPO ST 9cm.
BLOCO CERÂMICO DE VEDAÇÃO 19cm.	PLACA DRY-WALL CHAPA TIPO RU 6cm.
BLOCO CERÂMICO DE VEDAÇÃO 24cm.	PLACA DRY-WALL CHAPA TIPO RU COM REFORÇO METÁLICO 6cm.
BLOCO CERÂMICO DE VEDAÇÃO 25cm.	PLACA DRY-WALL CHAPA TIPO RU 9cm.
BLOCO DE CONCRETO CELULAR 10cm.	

ARQUIVOS EM USO

NOME DO ARQUIVO	DISCIPLINA
OCE-CLI-EX-0001-MOD-T00-R11.rvt	CLIMATIZAÇÃO
OCE-COM-EX-0001-GER-T00-R07.rvt	COMUNICAÇÃO EMBASAMENTO
OCE-COM-EX-0002-TIP-T00-R08.rvt	COMUNICAÇÃO TORRE
OCE-ELE-EX-0001-GER-T00-R25.rvt	ELÉTRICO EMBASAMENTO
OCE-ELE-EX-0002-TIP-T00-R08.rvt	ELÉTRICO TORRE
OCE-EPR-EX-0001-BIM-T00-R11.rvt	ESCADA PRESSURIZADA
OCE-EST-EX-00001-RVT-SMT-R01.rvt	ESTRUTURA METÁLICA
OCE-EST-PE-00001-RVT-GER-R24.rvt	ESTRUTURA
OCE-HID-EX-0001-BIM-T00-R15.rvt	HIDRÁULICO
OCE-HID-EX-0002-BIM-T00-R08.rvt	HIDRÁULICO
OCE-PCI-EX-0001-BIM-T00-R15.rvt	PREVENTIVO
OCE-SDR-EX-0001-BIM-T00-R16.rvt	SANITÁRIO
OCE-SDR-EX-0002-BIM-T00-R06.rvt	SANITÁRIO

OBSERVAÇÕES - ACABAMENTOS

01 - REVESTIMENTOS DA FACHADA, VER PRANCHAS 0125, 0126, 0127 E 0128.
02 - ACABAMENTOS DAS ÁREAS MOLHADAS ESTÃO ESPECIFICADOS NAS PRANCHAS DE DETALHES DE ÁREAS MOLHADAS (PACOTE 04).
03 - EM DÚVIDA DOS ACABAMENTOS DE PISO E RODAPÉ, VER PRANCHAS DE PAGINAÇÃO DE PISO (PACOTE 02).

NOTAS - PELE DE VIDROS

NOTA 01: TODAS DEVERÃO CONTER FECHOS DUPLOS.
NOTA 02: TODAS DEVERÃO CONTER BRAÇOS E LIMITADORES EM INOX.
NOTA 03: TODAS DEVERÃO CONTER ACABAMENTO INFERIOR E SUPERIOR (PISO E VIGA).
NOTA 04: TODAS DEVERÃO CONTER VIDRO LAMINADO 4+4mm.
NOTA 05: O FORNECEDOR DE VIDRO DEVERÁ VALIDAR AS ESPESSURAS DOS VIDROS CONFORME O VÃO DA ESQUADRIA.
NOTA 06: PREVER ISOLAMENTO ACÚSTICO ENTRE OS PAVTOS QUANDO A PELE DE VIDRO FOR PASSANTE E ESTIVER EM DORMITÓRIOS

ACABAMENTOS


CÓDIGO	DESCRIÇÃO
GT.02	GRANITO SOLEIRAS (ÁREAS COMUNS) - CONFORME PROJETO DE INTERIORES
GT.03	GRANITO PINGADEIRAS FLOREIRAS/MURETAS - CONFORME MEMORIAL DE ACABAMENTOS
KIT.01	KIT CHURRASQUEIRA MFC-950 (SALÃO DE FESTAS)
KIT.02	KIT CHURRASQUEIRA MFC-550 (LOUNGE GRILL; BAR MOLHADO)
KIT.03	KIT CHURRASQUEIRA LOUNGE GRILL NORTE (MFC-550 SEM OS PÉS)
PI.04	PISO PORCELANATO 60x120 cm - CONFORME MEMORIAL DE ACABAMENTOS
PI.09	PORCELANATO AMADEIRADO - CONFORME PROJETO DE INTERIORES
PI.10	PISO PLAYGROUND (COR A) - CONFORME PROJETO DE INTERIORES
PI.11	PISO PLAYGROUND (COR B) - CONFORME PROJETO DE INTERIORES
PI.12	PISO PLAYGROUND (COR C) - CONFORME PROJETO DE INTERIORES
PI.15	PORCELANATO LAZER (INTERNO) - CONFORME PROJETO DE INTERIORES
PI.16	PORCELANATO LAZER (EXTERNO) - CONFORME PROJETO DE INTERIORES
PT.03	TEXTURA CONCRETO (BANCO FIRELOUNGE) - CONFORME PROJETO DE INTERIORES
PT.06	TINTA ACRÍLICA (PAREDES) - CONFORME PROJETO DE INTERIORES
PT.17	TEXTURA ACRÍLICA HIDROREPELENTE IBRATIN PERMALIT PROGETTATO (PAREDE) - ESCADA/ANTECAMARA
PT.19	LAJE DE CONCRETO COM PINTURA TINTA LÁTEX PARA PISO COR CINZA (PISO)
PV.01	VEGETAÇÃO (VER DETALHES PROJETO PAISAGISMO)
RS.03	RODAPÉ H=14,5cm CORTADO EM OBRA - PORCELANATO 60x120cm - CONFORME MEMORIAL DE ACABAMENTOS
RS.07	RODAPÉ HALL SOCIAL TORRE - CONFORME PROJETO DE INTERIORES
RS.10	RODAPÉ MADEIRA/POLIESTIRENO (ÁREA COMUM LAZER) - CONFORME PROJETO DE INTERIORES
RV.01	REBOCO INTERNO
RV.03	MASSA CORRIDA PVA (PAREDE)
RV.17	PASTILHA PISCINA (MODELO A) - CONFORME PROJETO DE INTERIORES
RV.18	PASTILHA PISCINA (MODELO B) - CONFORME PROJETO DE INTERIORES
RV.26	REVESTIMENTO MADEIRA - CONFORME PROJETO DE INTERIORES

NOTAS - ESQUADRIAS (PORTAS E JANELAS) E VIDROS


NOTA 01: TODAS AS PERSIANAS DE QUARTOS DEVEM SER MOTORIZADAS E ACIONADAS POR CONTROLE REMOTO.
NOTA 02: TODAS AS ESQUADRIAS INTERNAS DE VIDRO TEMPERADO DEVEM CONTER MOLA DE PISO.
NOTA 03: TODAS AS ESQUADRIAS INTERNAS: VIDRO TEMPERADO 10mm.
NOTA 04: VIDROS BANHEIROS: MINI-BOREAL 4mm.
NOTA 05: VIDROS JANELAS DE QUARTOS: FLOAT 6mm.
NOTA 06: VIDROS PORTAS JANELAS: LAMINADO 4+4mm.
NOTA 07: VIDROS PORTAS JANELAS COM PERFIL INTERMEDIÁRIO: PARTE INFERIOR = LAMINADO 4+4mm, PARTE SUPERIOR = FLOAT 6mm
NOTA 08: O FORNECEDOR DE VIDRO DEVERÁ VALIDAR AS ESPESSURAS DOS VIDROS CONFORME O VÃO DA ESQUADRIA.
NOTA 09: CORES DAS ESQUADRIAS CONFORME ESPECIFICAÇÕES DAS TABELAS, ANTES DA EXECUÇÃO É NECESSÁRIO DISPONIBILIZAR AMOSTRAS DE TAMANHOS MAIORES PARA VALIDAÇÃO POR PARTE DA ARQUITETURA.

NOTAS - BRISES


NOTA 01: PARA OS BRISES UTILIZAR VENEZIANA VZ060 INVERTIDA COM PASSO DE 70mm, NOS DESENHOS AO LADO O PERFIL É REPRESENTATIVO GENÉRICO, EXCETO QUANDO HÁ NECESSIDADE EM SEGUIR UM PERFIL ESPECÍFICO DEVIDO A PROPOSTA DE FACHADA, SENDO ASSIM DIMENSÕES SERÃO INFORMADAS NOS DESENHOS AO LADO.
NOTA 02: A ÁREA MÍNIMA DE VENTILAÇÃO DEVERÁ SER DEFINIDO PELO RESPONSÁVEL DO PROJETO DE CLIMATIZAÇÃO, VISTO QUE OS BRISES FAZEM O FECHAMENTO DA ÁREA TÉCNICA ONDE ABRIGA AS CONDENSADORAS.

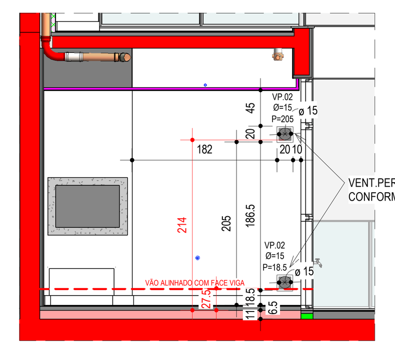


A — VP - VISTA A - FRIENDS & POOL
ESCALA 1 : 50

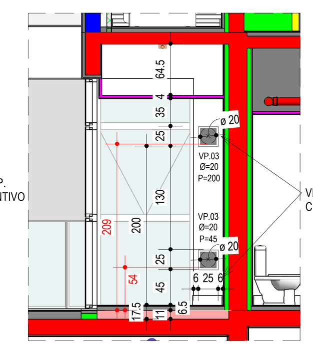


B — VP - VISTA B - PUB TEMÁTICO
ESCALA 1 : 50

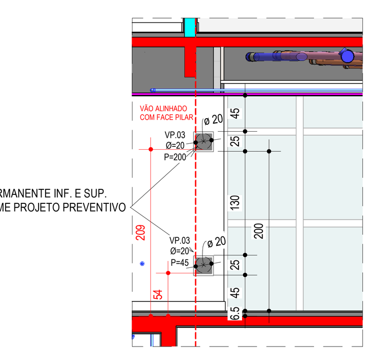


C — VP - VISTA C - SALÃO MASTERCHEF 01
ESCALA 1 : 50

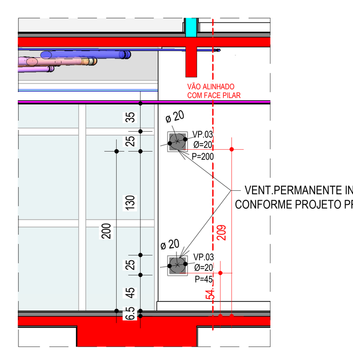

D — VP - VISTA D - SALÃO MASTERCHEF 02
ESCALA 1 : 50

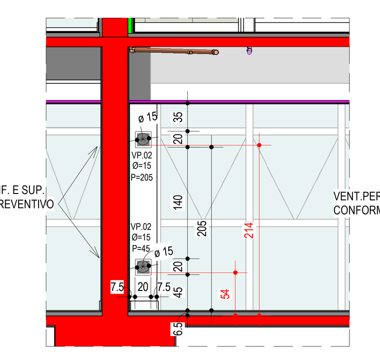

E — VP - VISTA E - SALÃO FESTAS 01
ESCALA 1 : 50

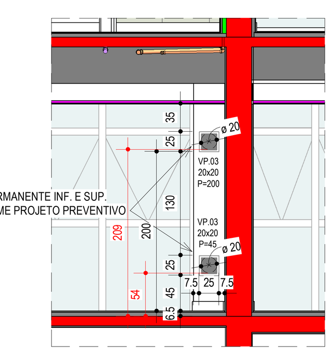

F — VP - VISTA F - SALÃO DE FESTAS 02
ESCALA 1 : 50

RELAÇÃO DE ESQUADRIAS - GUARDA-CORPO - LAZER

CÓDIGO	DESCRIÇÃO	QTD.	PERÍMETRO	ACABAMENTO
GC.14	GUARDA-CORPO ALUMÍNIO E VIDRO H=110cm + 01 PORTA DE GIRO DE 01FL.	1	3405	ALUMÍNIO COR BRANCA RAL9003 + VIDRO LAMINADO 4+4 SILVER 32 (GUARDIAN)
GC.15	GUARDA-CORPO ALUMÍNIO E VIDRO H=110cm + 01 PORTA DE GIRO DE 01FL.	1	2210.5	ALUMÍNIO COR BRANCA RAL9003 + VIDRO LAMINADO 4+4 SILVER 32 (GUARDIAN)
GC.16	GUARDA-CORPO ALUMÍNIO E VIDRO H=110cm + 01 PORTA DE GIRO DE 01FL.	1	322	ALUMÍNIO COR BRANCA RAL9003 + VIDRO LAMINADO 4+4 SILVER 32 (GUARDIAN)
GC.18	GUARDA-CORPO DE VIDRO COM PINÇA INOX H=110cm	1	981	VIDRO SILVER 32 + INOX
GC.19	GUARDA-CORPO DE VIDRO COM PINÇA INOX H=110cm COM 01 PORTA DE GIRO DE 01FL.	1	361	VIDRO SILVER 32 + INOX
GC.21	GUARDA-CORPO ALUMÍNIO E VIDRO H=110cm	1	2880.5	ALUMÍNIO COR BRANCA RAL9003 + VIDRO LAMINADO 4+4 SILVER 32 (GUARDIAN)
GC.22	GUARDA-CORPO ALUMÍNIO E VIDRO H=110cm	1	2352.5	ALUMÍNIO COR BRANCA RAL9003 + VIDRO LAMINADO 4+4 SILVER 32 (GUARDIAN)
GC.23	GUARDA-CORPO ALUMÍNIO E VIDRO H=110cm	1	2481.5	ALUMÍNIO COR BRANCA RAL9003 + VIDRO LAMINADO 4+4 SILVER 32 (GUARDIAN)
GC.24	GUARDA-CORPO ALUMÍNIO E VIDRO H=110cm	1	1372.5	ALUMÍNIO COR BRANCA RAL9003 + VIDRO LAMINADO 4+4 SILVER 32 (GUARDIAN)
GC.25	GUARDA-CORPO DE VIDRO COM PINÇA INOX H=110cm COM 01 PORTA DE GIRO DE 01FL.	1	249	VIDRO SILVER 32 + INOX
GC.26	GUARDA-CORPO DE VIDRO COM PINÇA INOX H=110cm	1	153.5	VIDRO SILVER 32 + INOX
GC.28	GUARDA-CORPO DE VIDRO COM PINÇA INOX H=110cm	1	51	VIDRO SILVER 32 + INOX
GC.29	GUARDA-CORPO DE VIDRO COM PINÇA INOX H=110cm COM 01 PORTA DE GIRO DE 01FL.	1	47	VIDRO SILVER 32 + INOX
GC.43	CORRIMÃO TUBULAR DUPLO H=70 + 92cm	1	201.5	INOX ESCOVADO
GC.45	CORRIMÃO TUBULAR DUPLO H=70 + 92cm	1	278.5	INOX ESCOVADO

RELAÇÃO DE ESQUADRIAS - DIVISÓRIAS - LAZER

CÓDIGO	DESCRIÇÃO	QTD.	ESQUADRIA LARGURA	ESQUADRIA ALTURA	ACABAMENTO
DV.01	DIVISÓRIA DE VIDRO FIXO	1	364.5	260	DIVISÓRIA DE VIDRO TEMPERADO 10mm ALUMÍNIO COR BRANCA RAL9003 + VIDRO INCOLOR
DV.02	DIVISÓRIA DE VIDRO FIXO COM 01 PORTA PIVOTANTE DE GIRO 01 FOLHA COM PERFIL PARA CONTROLE DE ACESSO	1	463	260	DIVISÓRIA DE VIDRO TEMPERADO 10mm ALUMÍNIO COR BRANCA RAL9003 + VIDRO INCOLOR
DV.03	DIVISÓRIA DE VIDRO FIXO	1	364.5	260	DIVISÓRIA DE VIDRO TEMPERADO 10mm ALUMÍNIO COR BRANCA RAL9003 + VIDRO INCOLOR
DV.04	DIVISÓRIA DE VIDRO FIXO COM 01 PORTA PIVOTANTE DE GIRO 01 FOLHA COM PERFIL PARA CONTROLE DE ACESSO	1	378.5	260	DIVISÓRIA DE VIDRO TEMPERADO 10mm ALUMÍNIO COR BRANCA RAL9003 + VIDRO INCOLOR
DV.05	DIVISÓRIA DE VIDRO FIXO COM 01 PORTA PIVOTANTE DE GIRO 01 FOLHA COM PERFIL PARA CONTROLE DE ACESSO	1	250	260	DIVISÓRIA DE VIDRO TEMPERADO 10mm ALUMÍNIO COR BRANCA RAL9003 + VIDRO INCOLOR
DV.06	DIVISÓRIA DE VIDRO FIXO COM 01 PORTA PIVOTANTE DE GIRO 01 FOLHA COM PERFIL PARA CONTROLE DE ACESSO	1	265	260	DIVISÓRIA DE VIDRO TEMPERADO 10mm ALUMÍNIO COR BRANCA RAL9003 + VIDRO INCOLOR
DV.07	DIVISÓRIA DE VIDRO COM PORTA DE CORRER 09 FOLHAS, RECOLHIMENTO TODAS AS FOLHAS PARA AS LATERAIS	1	849.5	262	DIVISÓRIA DE VIDRO TEMPERADO 10mm ALUMÍNIO COR BRANCA RAL9003 + VIDRO INCOLOR
DV.08	DIVISÓRIA DE VIDRO FIXO COM 01 PORTA PIVOTANTE DE GIRO 01 FOLHA COM PERFIL PARA CONTROLE DE ACESSO	1	573	260	DIVISÓRIA DE VIDRO TEMPERADO 10mm ALUMÍNIO COR BRANCA RAL9003 + VIDRO INCOLOR
DV.09	DIVISÓRIA DE VIDRO FIXO COM 01 PORTA PIVOTANTE DE GIRO 01 FOLHA	1	94	260	DIVISÓRIA DE VIDRO TEMPERADO 10mm ALUMÍNIO COR BRANCA RAL9003 + VIDRO INCOLOR
DV.10	DIVISÓRIA CONFORME PROJETO INTERIORES	1	367	260	DIVISÓRIA CONFORME PROJETO INTERIORES
DV.11	DIVISÓRIA DE VIDRO FIXO COM 01 PORTA PIVOTANTE DE GIRO 01 FOLHA COM PERFIL PARA CONTROLE DE ACESSO	1	373	260	DIVISÓRIA DE VIDRO TEMPERADO 10mm ALUMÍNIO COR BRANCA RAL9003 + VIDRO INCOLOR
DV.12	DIVISÓRIA DE VIDRO FIXO COM 01 PORTA PIVOTANTE DE GIRO 01 FOLHA COM PERFIL PARA CONTROLE DE ACESSO	1	502.5	260	DIVISÓRIA DE VIDRO TEMPERADO 10mm ALUMÍNIO COR BRANCA RAL9003 + VIDRO INCOLOR
DV.13	DIVISÓRIA DE VIDRO FIXO COM 01 PORTA PIVOTANTE DE GIRO 01 FOLHA COM PERFIL PARA CONTROLE DE ACESSO	1	461	260	DIVISÓRIA DE VIDRO TEMPERADO 10mm ALUMÍNIO COR BRANCA RAL9003 + VIDRO INCOLOR
DV.14	DIVISÓRIA DE VIDRO FIXO COM 01 PORTA PIVOTANTE DE GIRO 01 FOLHA COM PERFIL PARA CONTROLE DE ACESSO	1	265	260	DIVISÓRIA DE VIDRO TEMPERADO 10mm ALUMÍNIO COR BRANCA RAL9003 + VIDRO INCOLOR
DV.15	DIVISÓRIA DE VIDRO FIXO COM 01 PORTA PIVOTANTE DE GIRO 01 FOLHA COM PERFIL PARA CONTROLE DE ACESSO	1	256	260	DIVISÓRIA DE VIDRO TEMPERADO 10mm ALUMÍNIO COR BRANCA RAL9003 + VIDRO INCOLOR
DV.16	DIVISÓRIA DE VIDRO FIXO COM 01 PORTA PIVOTANTE DE GIRO 01 FOLHA	1	297	260	DIVISÓRIA DE VIDRO TEMPERADO 10mm ALUMÍNIO COR BRANCA RAL9003 + VIDRO INCOLOR
DV.17	DIVISÓRIA DE VIDRO FIXO COM 01 PORTA PIVOTANTE DE GIRO 01 FOLHA	1	303.5	260	DIVISÓRIA DE VIDRO TEMPERADO 10mm ALUMÍNIO COR BRANCA RAL9003 + VIDRO INCOLOR
DV.18	DIVISÓRIA DE VIDRO COM PORTA DE CORRER 05 FOLHAS, RECOLHIMENTO TODAS AS FOLHAS PARA AS LATERAIS	1	522.5	262	DIVISÓRIA DE VIDRO TEMPERADO 10mm ALUMÍNIO COR BRANCA RAL9003 + VIDRO INCOLOR

RELAÇÃO DE ESQUADRIAS - JANELAS - 4º PAVTO - LAZER (VER NOTA)

CÓDIGO	DESCRIÇÃO	QTD.	VÃO ALVENARIA (VO) LARGURA	VÃO ALVENARIA (VO) ALTURA	ESQUADRIA LARGURA	ESQUADRIA ALTURA	PEITORIL OSSO	PEITORIL ACAB.	ACABAMENTO
DAM.01	DUMPER	2	46	47.5	40	41.5	232.5	229	CONF. PROJETO EPR
DAM.02	DUMPER	2	106	67.5	100	61.5	23.5	20	CONF. PROJETO EPR
GRE.01	GRELHA INSUFLAMENTO DE AR	2	88.5	48.5	82.5	42.5		300	CONF. PROJETO EPR
VP.02	GRELHA DE VENTILAÇÃO PERMANENTE CONF.PROJ.PREVENTIVO	4	15	15	15	15	27.5/214 54/214	18.5/205 45/205	VP REDONDA (D=15cm) COM CAPA QUADRADA COR BRANCO RAL9003
VP.03	GRELHA DE VENTILAÇÃO PERMANENTE CONF.PROJ.PREVENTIVO	8	20	20	20	20	54/209	45/200	VP REDONDA (D=20cm) COM CAPA QUADRADA COR BRANCO RAL9003

RELAÇÃO DE ESQUADRIAS - PORTAS - LAZER (VER NOTA)


CÓDIGO	DESCRIÇÃO	QTD.	VÃO ALVENARIA (VO) LARGURA	VÃO ALVENARIA (VO) ALTURA	ESQUADRIA LARGURA	ESQUADRIA ALTURA	ACABAMENTO
PT.AL.01	PORTA DE GIRO 01 FOLHA	1	86	219.5	80	210	ALUMÍNIO - COR BRANCA RAL9003
PT.CF.01	PORTA DE GIRO 01 FOLHA - CORTA FOGO (CONF.PROJETO PCI)	4	96	215	89	210	PORTA CORTA-FOGO COR BRANCO
PT.MD.02	PORTA DE GIRO 01 FOLHA	11	78	221	70	210	MADEIRA - VISTA 7cm
PT.MD.03	PORTA DE GIRO 01 FOLHA	1	88	221	80	210	MADEIRA - VISTA 7cm
PT.MD.04	PORTA DE GIRO 01 FOLHA COM VENTILAÇÃO PERMANENTE CONF.PROJ.PCI.	2	88	221	80	210	MADEIRA - VISTA 7cm
PT.MD.05	PORTA DE GIRO 01 FOLHA	5	98	221	90	210	MADEIRA - VISTA 7cm
PT.MD.06	PORTA DE GIRO 01 FOLHA - PCD	2	98	221	90	210	MADEIRA - VISTA 7cm - BARRA DE APOIO HORIZONTAL - CHAPA DE INOX INFERIOR
PT.SH.02	PORTA DE GIRO 01 FOLHA - MANGOTINHO	1	84	94	80	90	ALUMÍNIO BRANCO RAL9003 + VIDRO INCOLOR
PT.VD.01	PORTA DE GIRO 01 FOLHA	1	106	219.5	100	210	ALUMÍNIO BRANCO RAL9003 + VIDRO NEUTRAL PLUS 50 (GUARDIAN)
PT.VZ.07	PORTA DE GIRO 01 FOLHA	4	86	219.5	80	210	ALUMÍNIO + VENEZIANA - COR BRANCO RAL9003
TP.01	TAMPA ALÇAPÃO DE PISO	5	60	60	60	60	PISO (MESMO PADRÃO DO ENTORNO)
TP.03	TAMPA ALÇAPÃO DE PISO - HERMÉTICA	1	80	80	80	80	TAMPA HERMÉTICA

RELAÇÃO DE ESQUADRIAS - PELE DE VIDRO - LAZER (VER NOTAS)

CÓDIGO	DESCRIÇÃO	QTD.	ESQUADRIA LARGURA	ESQUADRIA ALTURA	PEIT.	ACABAMENTO
PLV.07	PELE DE VIDRO 15cm	1	181.5	290	-4.5	PERFIL COR BRANCA RAL9003 + VIDRO LAMINADO 4+4mm SILVER 32 (GUARDIAN)
PLV.08	PELE DE VIDRO 15cm COM 02 MAXIM-AR POR PAVTO, 01 PORTA DE GIRO NO LAZER	1	223.5	6444.5	-4.5	PERFIL COR BRANCA RAL9003 + VIDRO LAMINADO 4+4mm SILVER 32 (GUARDIAN)
PLV.09	PELE DE VIDRO 15cm COM 03 MAXIM-AR	1	390	290	-4.5	PERFIL COR BRANCA RAL9003 + VIDRO LAMINADO 4+4mm SILVER 32 (GUARDIAN)
PLV.10	PELE DE VIDRO 15cm COM 01 PORTA DE GIRO 01 FOLHA + 01 MAXIM-AR	1	388	290	-4.5	PERFIL COR BRANCA RAL9003 + VIDRO LAMINADO 4+4mm SILVER 32 (GUARDIAN)
PLV.11	PELE DE VIDRO 15cm	1	80.5	290	-4.5	PERFIL COR BRANCA RAL9003 + VIDRO LAMINADO 4+4mm SILVER 32 (GUARDIAN)
PLV.12	PELE DE VIDRO 15cm COM 01 MAXIM-AR	1	121	290	-4.5	PERFIL COR BRANCA RAL9003 + VIDRO LAMINADO 4+4mm SILVER 32 (GUARDIAN)
PLV.13	PELE DE VIDRO 15cm COM 01 MAXIM-AR	1	302.5	290	-4.5	PERFIL COR BRANCA RAL9003 + VIDRO LAMINADO 4+4mm SILVER 32 (GUARDIAN)
PLV.14	PELE DE VIDRO 15cm	1	85.5	290	-4.5	PERFIL COR BRANCA RAL9003 + VIDRO LAMINADO 4+4mm SILVER 32 (GUARDIAN)
PLV.15	PELE DE VIDRO 15cm	1	57	290	-4.5	PERFIL COR BRANCA RAL9003 + VIDRO LAMINADO 4+4mm SILVER 32 (GUARDIAN)
PLV.16	PELE DE VIDRO 15cm COM 01 PORTA DE GIRO 01 FOLHA + 03 MAXIM-AR	1	371	290	-4.5	PERFIL COR BRANCA RAL9003 + VIDRO LAMINADO 4+4mm SILVER 32 (GUARDIAN)
PLV.17	PELE DE VIDRO - PAINEL FIXO	1	124	290	-4.5	PERFIL COR BRANCA RAL9003 + VIDRO LAMINADO 4+4mm SILVER 32 (GUARDIAN)
PLV.18	PELE DE VIDRO 15cm COM 03 MAXIM-AR	1	282.5	290	-4.5	PERFIL COR BRANCA RAL9003 + VIDRO LAMINADO 4+4mm SILVER 32 (GUARDIAN)
PLV.19	PELE DE VIDRO 15cm	1	143	259	26.5	PERFIL COR BRANCA RAL9003 + VIDRO LAMINADO 4+4mm SILVER 32 (GUARDIAN)
PLV.20	PELE DE VIDRO 15cm	1	285	290	-4.5	PERFIL COR BRANCA RAL9003 + VIDRO LAMINADO 4+4mm SILVER 32 (GUARDIAN)
PLV.21	PELE DE VIDRO 15cm	1	285	290	-4.5	PERFIL COR BRANCA RAL9003 + VIDRO LAMINADO 4+4mm SILVER 32 (GUARDIAN)
PLV.22	PELE DE VIDRO 15cm	1	142	290	-4.5	PERFIL COR BRANCA RAL9003 + VIDRO LAMINADO 4+4mm SILVER 32 (GUARDIAN)
PLV.23	PELE DE VIDRO 15cm COM 01 MAXIM-AR	1	282.5	290	-4.5	PERFIL COR BRANCA RAL9003 + VIDRO LAMINADO 4+4mm SILVER 32 (GUARDIAN)
PLV.24	PELE DE VIDRO - PAINEL FIXO	1	124	290	-4.5	PERFIL COR BRANCA RAL9003 + VIDRO LAMINADO 4+4mm SILVER 32 (GUARDIAN)
PLV.25	PELE DE VIDRO 15cm COM 03 MAXIM-AR	1	371	290	-4.5	PERFIL COR BRANCA RAL9003 + VIDRO LAMINADO 4+4mm SILVER 32 (GUARDIAN)
PLV.26	PELE DE VIDRO 15cm	1	57	290	-4.5	PERFIL COR BRANCA RAL9003 + VIDRO LAMINADO 4+4mm SILVER 32 (GUARDIAN)
PLV.27	PELE DE VIDRO 15cm COM 01 MAXIM-AR	1	85.5	290	-4.5	PERFIL COR BRANCA RAL9003 + VIDRO LAMINADO 4+4mm SILVER 32 (GUARDIAN)
PLV.28	PELE DE VIDRO 15cm COM 01 PORTA DE GIRO 01 FOLHA	1	125	285.5	0	PERFIL COR BRANCA RAL9003 + VIDRO LAMINADO 4+4mm SILVER 32 (GUARDIAN)
PLV.29	PELE DE VIDRO 15cm COM 01 PORTA DE GIRO 01 FOLHA	1	146	285.5	0	PERFIL COR BRANCA RAL9003 + VIDRO LAMINADO 4+4mm SILVER 32 (GUARDIAN)
PLV.30	PELE DE VIDRO 15cm COM 03 MAXIM-AR	1	383.5	290	-4.5	PERFIL COR BRANCA RAL9003 + VIDRO LAMINADO 4+4mm SILVER 32 (GUARDIAN)
PLV.31	PELE DE VIDRO 15cm COM 03 MAXIM-AR E 01 PORTA DE GIRO 01 FOLHA	1	1133.5	290	-4.5	PERFIL COR BRANCA RAL9003 + VIDRO LAMINADO 4+4mm SILVER 32 (GUARDIAN)
PLV.32	PELE DE VIDRO 15cm COM 02 MAXIM-AR	1	275.5	290	-4.5	PERFIL COR BRANCA RAL9003 + VIDRO LAMINADO 4+4mm SILVER 32 (GUARDIAN)
PLV.33	PELE DE VIDRO 15cm COM 01 PORTA DE GIRO 01 FOLHA	1	304.5	285.5	0	PERFIL COR BRANCA RAL9003 + VIDRO LAMINADO 4+4mm SILVER 32 (GUARDIAN)
PLV.34	PELE DE VIDRO 15cm COM 02 MAXIM-AR	1	280	290	-4.5	PERFIL COR BRANCA RAL9003 + VIDRO LAMINADO 4+4mm SILVER 32 (GUARDIAN)
PLV.35	PELE DE VIDRO 15cm	1	212	248	37.5	PERFIL COR BRANCA RAL9003 + VIDRO LAMINADO 4+4mm SILVER 32 (GUARDIAN)
PLV.36	PELE DE VIDRO 15cm COM 01 MAXIM-AR POR PAVTO	1	138	6402.5	37.5	PERFIL COR BRANCA RAL9003 + VIDRO LAMINADO 4+4mm SILVER 32 (GUARDIAN)
PLV.37	PELE DE VIDRO 15cm COM 03 MAXIM-AR	1	389.5	248	37.5	PERFIL COR BRANCA RAL9003 + VIDRO LAMINADO 4+4mm SILVER 32 (GUARDIAN)
PLV.38	PELE DE VIDRO 15cm COM 03 MAXIM-AR	1	381	290	-4.5	PERFIL COR BRANCA RAL9003 + VIDRO LAMINADO 4+4mm SILVER 32 (GUARDIAN)
PLV.39	PELE DE VIDRO 15cm COM 01 PORTA DE GIRO 01 FOLHA	1	127.5	285.5	0	PERFIL COR BRANCA RAL9003 + VIDRO LAMINADO 4+4mm SILVER 32 (GUARDIAN)
PLV.40	PELE DE VIDRO 15cm	1	85.5	290	-4.5	PERFIL COR BRANCA RAL9003 + VIDRO LAMINADO 4+4mm SILVER 32 (GUARDIAN)
PLV.41	PELE DE VIDRO 15cm	1	55	290	-4.5	PERFIL COR BRANCA RAL9003 + VIDRO LAMINADO 4+4mm SILVER 32 (GUARDIAN)
PLV.42	PELE DE VIDRO 15cm COM 04 MAXIM-AR	1	371	290	-4.5	PERFIL COR BRANCA RAL9003 + VIDRO LAMINADO 4+4mm SILVER 32 (GUARDIAN)
PLV.43	PELE DE VIDRO - PAINEL FIXO	1	124	290	-4.5	PERFIL COR BRANCA RAL9003 + VIDRO LAMINADO 4+4mm SILVER 32 (GUARDIAN)
PLV.44	PELE DE VIDRO 15cm COM 03 MAXIM-AR	1	282.5	290	-4.5	PERFIL COR BRANCA RAL9003 + VIDRO LAMINADO 4+4mm SILVER 32 (GUARDIAN)
PLV.45	PELE DE VIDRO 15cm	1	142	290	-4.5	PERFIL COR BRANCA RAL9003 + VIDRO LAMINADO 4+4mm SILVER 32 (GUARDIAN)
PLV.46	PELE DE VIDRO 15cm COM 03 MAXIM-AR	1	463	290	-4.5	PERFIL COR BRANCA RAL9003 + VIDRO LAMINADO 4+4mm SILVER 32 (GUARDIAN)
PLV.47	PELE DE VIDRO 15cm	1	248.5	290	-4.5	PERFIL COR BRANCA RAL9003 + VIDRO LAMINADO 4+4mm SILVER 32 (GUARDIAN)
PLV.48	PELE DE VIDRO 15cm	1	248.5	290	-4.5	PERFIL COR BRANCA RAL9003 + VIDRO LAMINADO 4+4mm SILVER 32 (GUARDIAN)
PLV.49	PELE DE VIDRO 15cm COM 03 MAXIM-AR	1	458	290	-4.5	PERFIL COR BRANCA RAL9003 + VIDRO LAMINADO 4+4mm SILVER 32 (GUARDIAN)
PLV.50	PELE DE VIDRO 15cm	1	142	290	-4.5	PERFIL COR BRANCA RAL9003 + VIDRO LAMINADO 4+4mm SILVER 32 (GUARDIAN)
PLV.51	PELE DE VIDRO 15cm COM 03 MAXIM-AR	1	282.5	290	-4.5	PERFIL COR BRANCA RAL9003 + VIDRO LAMINADO 4+4mm SILVER 32 (GUARDIAN)
PLV.52	PELE DE VIDRO - PAINEL FIXO	1	124	290	-4.5	PERFIL COR BRANCA RAL9003 + VIDRO LAMINADO 4+4mm SILVER 32 (GUARDIAN)
PLV.53	PELE DE VIDRO 15cm COM 01 PORTA DE GIRO 01 FOLHA + 02 MAXIM-AR	1	371	290	-4.5	PERFIL COR BRANCA RAL9003 + VIDRO LAMINADO 4+4mm SILVER 32 (GUARDIAN)
PLV.54	PELE DE VIDRO 15cm	1	49	290	-4.5	PERFIL COR BRANCA RAL9003 + VIDRO LAMINADO 4+4mm SILVER 32 (GUARDIAN)
PLV.55	PELE DE VIDRO 15cm	1	85.5	290	-4.5	PERFIL COR BRANCA RAL9003 + VIDRO LAMINADO 4+4mm SILVER 32 (GUARDIAN)
PLV.56	PELE DE VIDRO 15cm COM 02 MAXIM-AR	1	220.5	290	-4.5	PERFIL COR BRANCA RAL9003 + VIDRO LAMINADO 4+4mm SILVER 32 (GUARDIAN)
PLV.57	PELE DE VIDRO 15cm COM 02 MAXIM-AR	1	163	290	-4.5	PERFIL COR BRANCA RAL9003 + VIDRO LAMINADO 4+4mm SILVER 32 (GUARDIAN)
PLV.58	PELE DE VIDRO 15cm	1	81.5	290	-4.5	PERFIL COR BRANCA RAL9003 + VIDRO LAMINADO 4+4mm SILVER 32 (GUARDIAN)
PLV.59	PELE DE VIDRO 15cm COM 01 PORTA DE GIRO 01 FOLHA + 02 MAXIM-AR	1	388	290	-4.5	PERFIL COR BRANCA RAL9003 + VIDRO LAMINADO 4+4mm SILVER 32 (GUARDIAN)
PLV.60	PELE DE VIDRO 15cm COM 01 PORTA DE GIRO 01 FOLHA + 02 MAXIM-AR	1	390	290	-4.5	PERFIL COR BRANCA RAL9003 + VIDRO LAMINADO 4+4mm SILVER 32 (GUARDIAN)
PLV.61	PELE DE VIDRO 15cm COM 01 MAXIM-AR POR PAVTO	1	107.5	6444.5	-4.5	PERFIL COR BRANCA RAL9003 + VIDRO LAMINADO 4+4mm SILVER 32 (GUARDIAN)
PLV.62	PELE DE VIDRO 15cm	1	197.5	290	-4.5	PERFIL COR BRANCA RAL9003 + VIDRO LAMINADO 4+4mm SILVER 32 (GUARDIAN)
PLV.63	PELE DE VIDRO 15cm COM 03 MAXIM-AR	1	503.5	290	-4.5	PERFIL COR BRANCA RAL9003 + VIDRO LAMINADO 4+4mm SILVER 32 (GUARDIAN)
PLV.64	PELE DE VIDRO 15cm COM 03 MAXIM-AR	1	398.5	290	-4.5	PERFIL COR BRANCA RAL9003 + VIDRO LAMINADO 4+4mm SILVER 32 (GUARDIAN)
PLV.65	PELE DE VIDRO 15cm COM 02 MAXIM-AR	1	271	290	-4.5	PERFIL COR BRANCA RAL9003 + VIDRO LAMINADO 4+4mm SILVER 32 (GUARDIAN)

RELAÇÃO DE ESQUADRIAS - BRISES - LAZER (VER NOTA)

CÓDIGO	DESCRIÇÃO	QTD.	ESQUADRIA LARGURA	ESQUADRIA ALTURA	ACABAMENTO
BR.20A	BRISE HORIZONTAL VENEZIANA VZ060 INVERTIDA COM PASSO DE 70mm	1	212	350	ALUMÍNIO COR BRANCA RAL9003
BR.20B	BRISE HORIZONTAL VENEZIANA VZ060 INVERTIDA COM PASSO DE 70mm	1	44.5	350	ALUMÍNIO COR BRANCA RAL9003
BR.21A	BRISE HORIZONTAL VENEZIANA VZ060 INVERTIDA COM PASSO DE 70mm	1	190	350	ALUMÍNIO COR BRANCA RAL9003
BR.21B	BRISE HORIZONTAL VENEZIANA VZ060 INVERTIDA COM PASSO DE 70mm	1	44.5	350	ALUMÍNIO COR BRANCA RAL9003
BR.22A	BRISE HORIZONTAL VENEZIANA VZ060 INVERTIDA COM PASSO DE 70mm	1	57.5	50	ALUMÍNIO COR BRANCA RAL9003
BR.22B	BRISE HORIZONTAL VENEZIANA VZ060 INVERTIDA COM PASSO DE 70mm	1	436	50	ALUMÍNIO COR BRANCA RAL9003
BR.22C	BRISE HORIZONTAL VENEZIANA VZ060 INVERTIDA COM PASSO DE 70mm	1	57.5	50	ALUMÍNIO COR BRANCA RAL9003
BR.23	BRISE HORIZONTAL VENEZIANA VZ060 INVERTIDA COM PASSO DE 70mm	1	251.5	120	ALUMÍNIO COR BRANCA RAL9003
BR.24	BRISE HORIZONTAL VENEZIANA VZ060 INVERTIDA COM PASSO DE 70mm COM 1 PORTA DE GIRO DE 1FL.	1	137.5	120	ALUMÍNIO COR BRANCA RAL9003

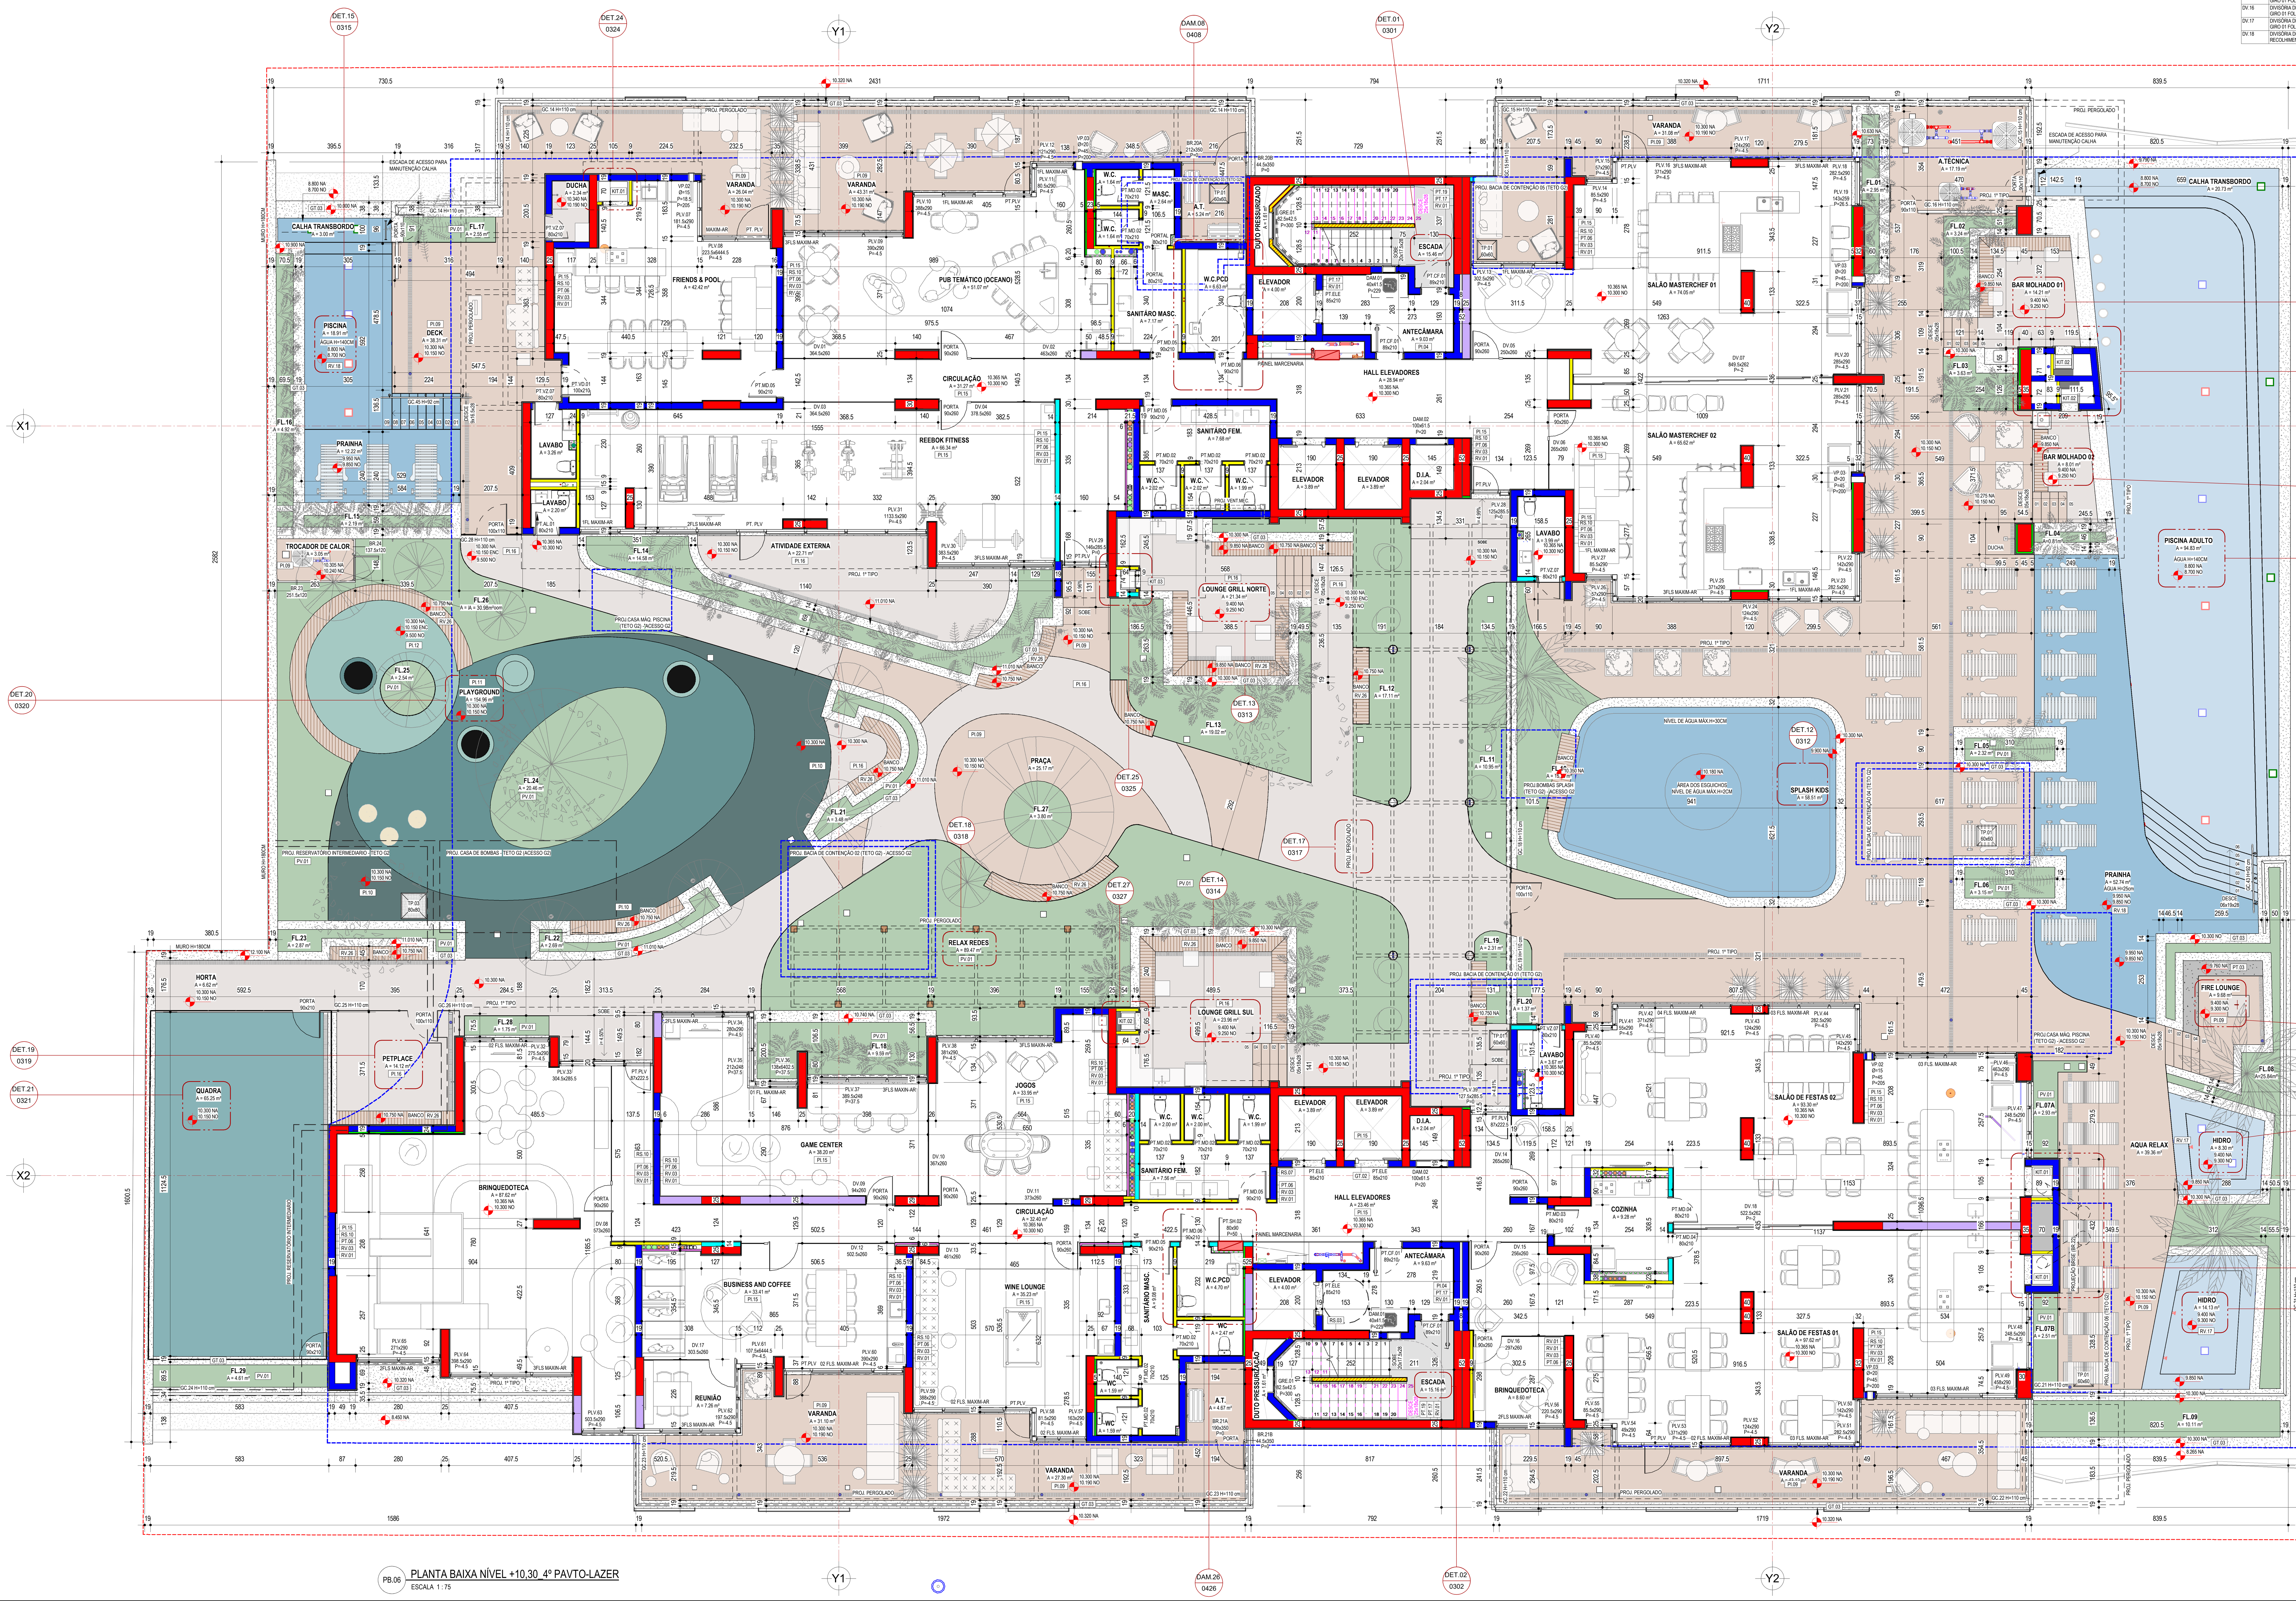

PB.06 — PLANTA BAIXA NÍVEL +10,30_4º PAVTO-LAZER
ESCALA 1 : 75

Nº	DATA	REVISÃO	RESPONSÁVEL
R23	14/06/2024	REVISÃO EXECUTIVO: INSERIDO DUCHA E FIRE PLACE NO FRIENDS & POOL; SUPRESSÃO DAS PAREDES INTERNAS DOS LAVABOS EXTERNOS; ALTERADO ESQUADRIAS PLV.08, PLV.31, PLV.51, PLV.53, DV.12, DV.18; ALTERAÇÃO LAYOUT	JULIA MATTOS
R22	19/04/2024	REVISÃO EXECUTIVO: AJUSTADO COMPRIMENTO GC.14 E GC.21 / ATUALIZADAS DIMENSÕES DA PT.CF.01 (ID1147) / SUBSTITUIÇÃO DO GC.27 PELOS BRISES BR.23 E BR.24 / ATUALIZADA GEOMETRIA DAS FLOREIRAS 15 E 16 (ID3299) - ATUALIZADO MATERIAL DA PAREDE CENTRAL DA ESCADA DE EMERGÊNCIA (ID9542)	PAULA OLIVO
R21	08/02/2024	REVISÃO EXECUTIVO: ALTERADO POSIÇÃO CHURRASQUEIRA SALÃO DE FESTAS 01 E 02	CAROLINE DUARTE
R20	25/01/2024	REVISÃO EXECUTIVO: INSERIDO ABERTURAS NAS PELES CONFORME SOLICITAÇÃO DE INTERIORES	CAROLINE DUARTE
R19	19/01/2024	REVISÃO EXECUTIVO: CORREÇÃO DESCRIÇÃO DV.02, DV.06, DV.18, DV.19; ALTERADO DESCRIÇÃO DV.08, 11, 12, 13 CONFORME SOLICITAÇÃO VETTER ID6029	CAROLINE DUARTE
R18	20/12/2023	REVISÃO EXECUTIVO: ADICIONADO RAL TABELA, ALTERADO NUMERAÇÃO VP'S, INCLUSO INFORMAÇÕES TABELA PELE DE VIDRO, INSERIDO PORTA E ESCADA DE ACESSO PARA MANUTENÇÃO CALHA DE TRANSBORDO, ALTERADO ESPESSURA PAREDE ENTRE SANITÁRIO E WINE LOUNGE; ALTERAÇÃO DE PREMISSA DIMENSÕES PORTAS E JANELAS; ALTERADO PORTA COZINHA SALÃO 01 TSU; INSERIDO TABELA GC E DIVISÓRIAS; ALTERADO MODELO GC.18, 19, 25, 26, 28, 29; ELIMINADO DEGRAU HIDROMASSAGEM; INSERIDO BR.22	CAROLINE DUARTE
R17	15/06/2023	REVISÃO EXECUTIVO: CONFORME SOLICITADO PELO ENG.JOSÉ NO DIA 29/05 - AJUSTE NA INCLINAÇÃO, GEOMETRIA E BANCO DO SPLASH KIDS; ALTERADO ALVENARIAS DA CHURRASQUEIRA (CONSIDERADO KIT PRÉ MOLDADO); AJUSTE CORES DRYWALL RU	CAROLINE DUARTE
R16	28/04/2023	REVISÃO EXECUTIVO: INSERIDO CORRIMÃO NAS ESCADAS DAS PISCINAS, FIRE LOUNGE, BAR MOLHADO 01 E 02; INSERIDO NOMENCLATURA E ÁREA EM FLOREIRAS FALTANTES; AJUSTES CORES PLAYGROUND CONFORME IMAGEM DE VENDA	CAROLINE DUARTE
R15	18/04/2023	REVISÃO EXECUTIVO: INCLUSO ENCHIMENTO PARA PONTO DE GÁS DO GRILL NO SALÃO MASTERCHEF 02, AJUSTES VP	CAROLINE DUARTE
R14	24/03/2023	REVISÃO EXECUTIVO: CORRIGIDO QUANTIDADE VP.02, VP.03; ADICIONADO PT.SH.02 NO QUADRO DE ESQUADRIA	CAROLINE DUARTE
R13	07/03/2023	REVISÃO EXECUTIVO: REVISÃO GERAL ESQUADRIAS, INSERIDO ABERTURAS DIVISÓRIA SALÃO DE FESTAS 01 E 02; ATUALIZAÇÃO ARQUIVOS EM USO	CAROLINE DUARTE
R12	10/01/2023	REVISÃO EXECUTIVO: ADICIONADO PROJEÇÃO BACIA DE CONTENÇÃO 06	CAROLINE DUARTE
R11	10/01/2023	REVISÃO EXECUTIVO: ELIMINADO TORNEIRA DE ÁGUA POTÁVEL; ADICIONADO PROJEÇÃO BACIA DE CONTENÇÃO 06	CAROLINE DUARTE
R10	21/12/2022	EMISSÃO INICIAL EXECUTIVO CIVIL	EQUIPE TÉCNICA
R9	01/12/2022	AUMENTO LARGURA CHURRASQUEIRA SALÃO DE FESTAS 01, 02 E FRIENDS&POOL (CONFORME SOLICITADO NO ID6715)	CAROLINE DUARTE
R8	21/10/2022	ATUALIZAÇÃO LAYOUT SALÃO MASTERCHEF 02	CAROLINE DUARTE
R7	11/08/2022	REVISÃO ETAPA EXECUTIVO PARCIAL: ENTREGA INTERMEDIÁRIA	CAROLINE DUARTE
R6	30/06/2022	REVISÃO ETAPA EXECUTIVO PARCIAL	CAROLINE DUARTE
R5	16/05/2022	EMISSÃO INICIAL ETAPA EXECUTIVO PARCIAL	GIULIA P TACHINI
R4	31/03/2022	INCLUÍDAS COTAS TELAS METÁLICAS	GIULIA P TACHINI
R3	23/03/2022	INCLUÍDOS CORTES E ELEVAÇÕES	GIULIA P TACHINI
R2	16/03/2022	INCLUÍDO LAYOUT DE INTERIORES	GIULIA P TACHINI
R1	04/03/2022	EMISSÃO INICIAL ETAPA PRÉ-EXECUTIVO	GIULIA P TACHINI
R0	19/01/2022	EMISSÃO INICIAL ETAPA PRÉ-EXECUTIVO PARCIAL	GIULIA P TACHINI

EMPREENDIMENTO: 198

OCEAN PARK
EDIFICIO MULTIFAMILIAR EM ALVENARIA

AVENIDA NEREU RAMOS, Nº 3477 - CENTRO - PIÇARRAS - SANTA CATARINA

CONTEÚDO:
PLANTA BAIXA NÍVEL +10,30 (4º PAVTO - LAZER)

@MANNZ
MANNZ.ARQ.BR
+55 47 3322 3690
PROJETOS@MANNZ.COM.BR

MANNZ ARQUITETOS ASSOCIADOS
R. NEREU RAMOS, 942 | SALA 701
JARDIM BLUMENAU. BLUMENAU, SC/BR

ATIVE A ARQUITETURA

MANNZ Arquitetos Associados

PROPRIETÁRIO: VETTER EMPREENDIMENTOS

ETAPA: EX — EXECUTIVO
REVISÃO: R23

ENGENHEIRO RESPONSÁVEL EXECUÇÃO:

DATA: 14/06/2024
ESCALA: As indicated

RESPONSÁVEIS TÉCNICOS:
Jonas Eduardo Franz — CAU/SC A26279-0
Marcelo Mannrich — CAU/SC A32511-2

EQUIPE TÉCNICA:
Caroline Duarte — CAU/SC A109526-9
Mariana Maass — CAU/SC A158230-5

DESENHO No. 0106

14/06/2024 13:56:53